

THESE DRAWINGS ARE FREE FOR YOU TO SHARE, MODIFY, AND DUPLICATE. THIS WORK DOES NOT REPRESENT A LEGAL CONTRACT OR CONSTITUTE ARCHITECTURAL SERVICES. NO PERSON OR ORGANIZATION MAKES ANY WARRANTY REGARDING THE INFORMATION PROVIDED. THE CREATOR DISCLAIMS LIABILITY FOR ANY DAMAGES RESULTING FROM ITS USE. THIS WORK IS AVAILABLE UNDER A CREATIVE COMMONS ATTRIBUTION SHARE-A-LIKE LICENSE. SOME RIGHTS RESERVED.

AMERICAN FARMHOUSE



OPEN-SOURCE
ARCHITECTURAL
DRAWING SET

A DESIGN BY JAY OSBORNE
AMERICAN FARMHOUSE
FREE FILES AVAILABLE AT FREEFARMHOUSE.COM

REVISIONS
02-14-2015
FIRST ONLINE RELEASE
12-31-2019
MINOR GRAPHIC EDITS
12-25-2020
RENAMED & REFINED

DATE
12-25-2020




SHEET TITLE
COVER PAGE

SHEET NO.

A0.0

SYMBOLS LEGEND			
	SECTION MARKER		SOIL
	ELEVATION MARKER		CONCRETE
	INT ELEVATIONS		BRICK
	DETAIL CALLOUT		CMU BLOCK
	COMPASS (TRUE)		RIGID INSULATION
	DATUM MARKER		BATT INSULATION
	WINDOW CALLOUT		ELECTRIC OUTLET
	DOOR CALLOUT		SWITCH
	FIXTURE CALLOUT		CEILING LIGHT
	FINISH CALLOUT		RECESSED LIGHT
	CONTOURS (FEET)		WALL-HUNG LIGHT
			CEILING FAN
			SMOKE DETECTOR

ABBREVIATIONS			
#	POUNDS OR NUMBER	INT	INTERIOR
AC	AIR CONDITIONING	MAX	MAXIMUM
B.O.	BOTTOM OF	MIN	MINIMUM
B/T	BETWEEN	(N)	NEW
BD	BOARD	NTS	NOT TO SCALE
BM	BEAM	OC	ON CENTER
CLG	CEILING	PERF	PERFORATED
CLR	CLEAR	PT	PRESSURE-TREATED
CMU	CONC MASONRY UNIT	QTY	QUANTITY
CONC	CONCRETE	R	RADIUS OR RISER
CONT	CONTINUOUS	RCP	REFLECTED CEILING PLAN
D	DRYER	REF	REFRIGERATOR
DEMO	DEMOLISH	SD	SMOKE DETECTOR
DIA	DIAMETER	SF	SQUARE FEET
DIM	DIMENSION	SPEC	SPECIFICATION
DM	DIMMER	SYM	SYMMETRICAL
DN	DOWN	T.O.	TOP OF
DW	DISHWASHER	T&G	TONGUE & GROOVE
(E)	EXISTING	TYP	TYPICAL
EL	ELEVATION	W	WASHER OR WATT
ELEC	ELECTRICAL	W/	WITH
EQ	EQUAL	W/D	WASHER & DRYER
EXT	EXTERIOR	W/O	WITHOUT
FIN	FINISH	WC	WATER CLOSET
FT	FOOT	WD	WOOD
GALV	GALVANIZED	WH	WATER HEATER
GFCI	CIRCUIT INTERRUPTER	WP	WEATHERPROOF
GYP	GYPSUM		

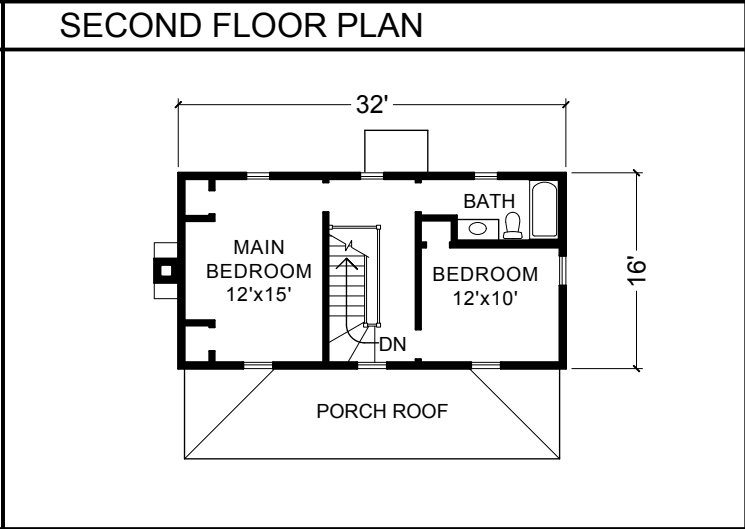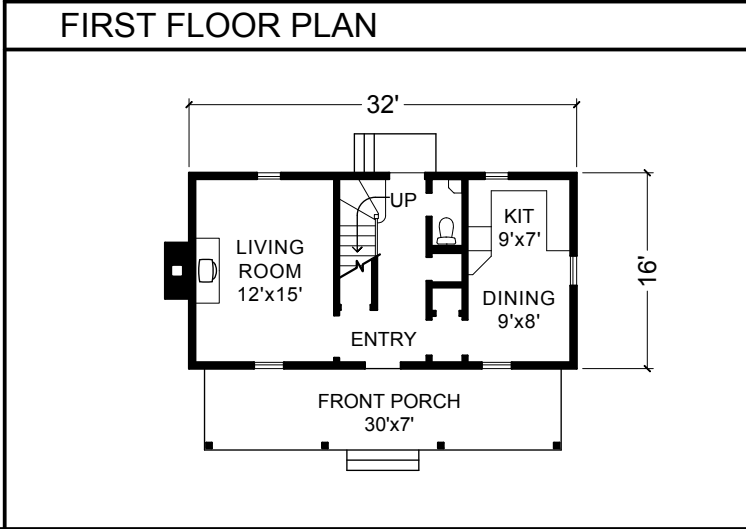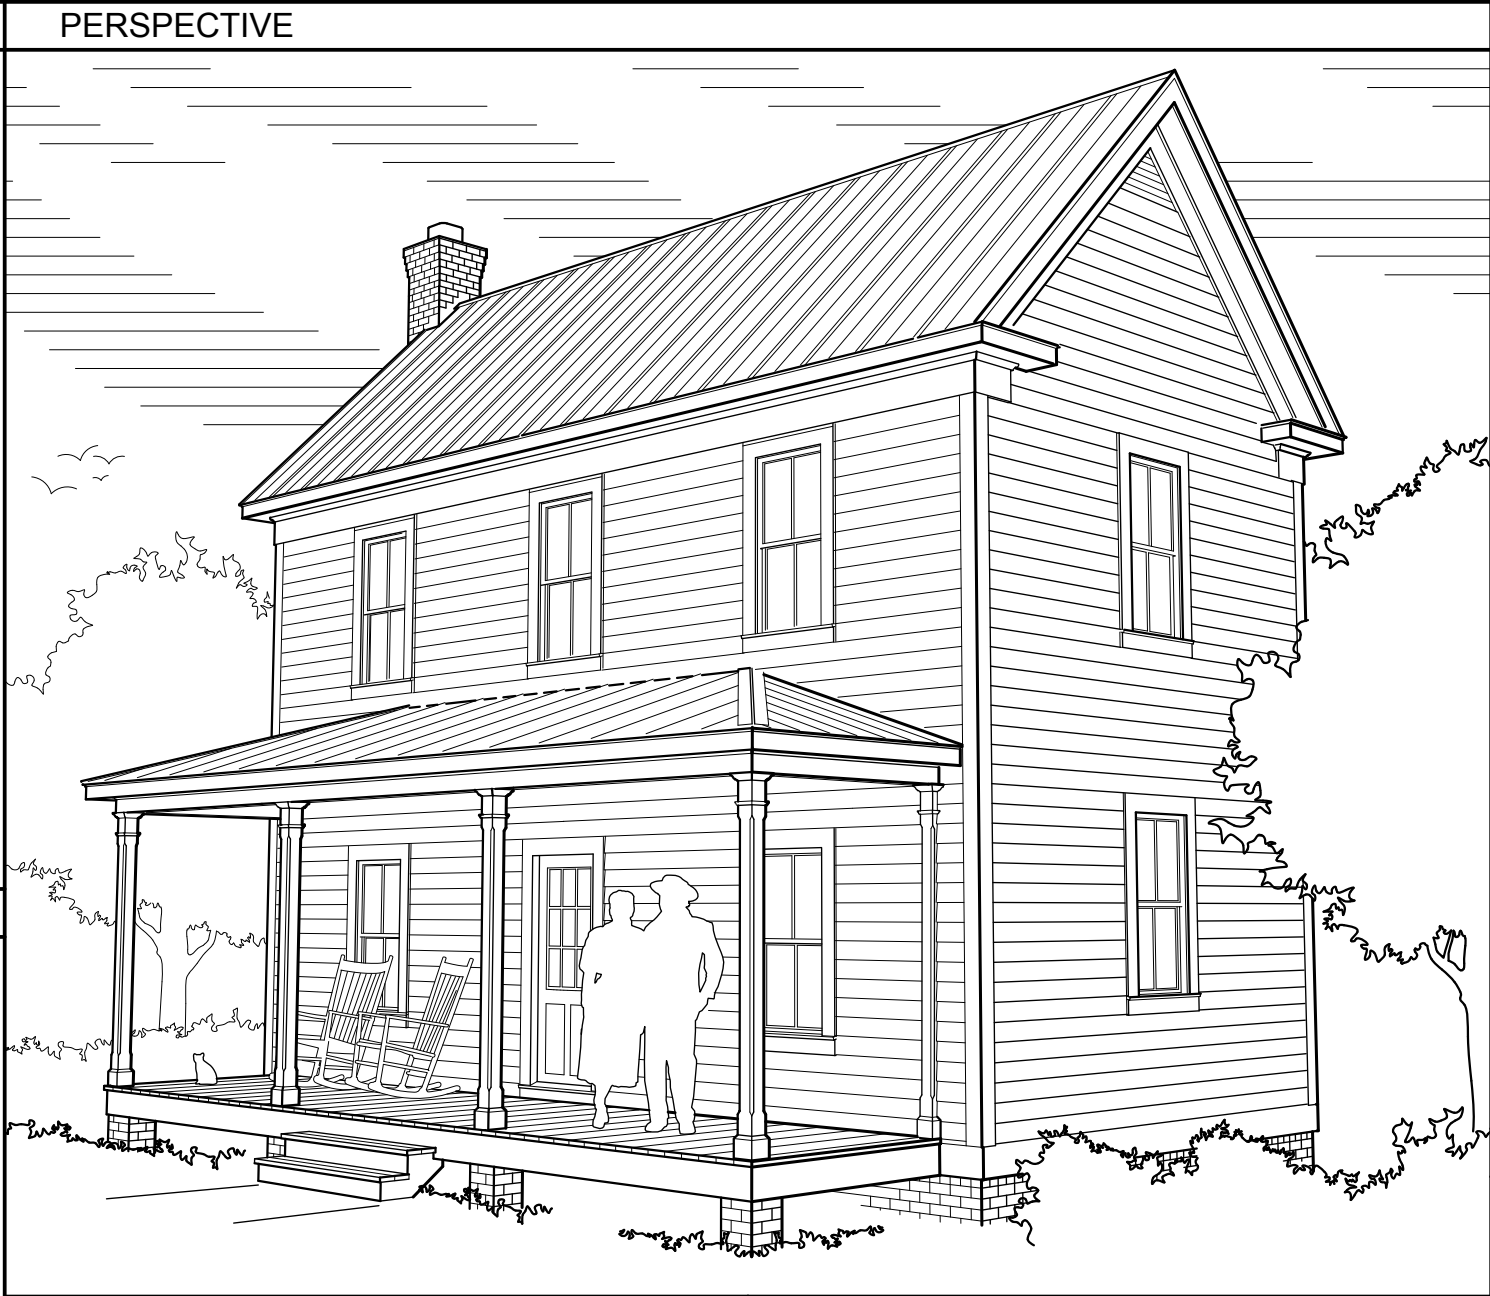

SHEET INDEX	
A0.0	COVER PAGE
A0.1	PROJECT INFORMATION
A0.2	GENERAL NOTES
A1.0	SITE PLAN
A1.1	FOUNDATION PLAN
A1.2	1ST FLOOR PLAN
A1.3	2ND FLOOR PLAN
A1.4	ROOF PLAN
A1.5	1ST RCP/ELECTRICAL
A1.6	2ND RCP/ELECTRICAL
A1.7	DETAIL PLANS
A2.0	SOUTH ELEVATION
A2.1	WEST ELEVATION
A2.2	NORTH ELEVATION
A2.3	EAST ELEVATION
A2.4	INTERIOR ELEVATIONS
A2.5	INTERIOR ELEVATIONS
A3.0	LONGITUDINAL SECTION
A3.1	TRANSVERSE SECTION
A3.2	TRANSVERSE SECTION
A4.0	TYPICAL DETAILS
A4.1	DECORATIVE DETAILS
A4.2	EXTERIOR DETAILS
A4.3	DOORS & WINDOWS
A5.0	SCHEDULES

IMPORTANT NOTE

You are encouraged to share, reprint, modify, and improve these drawings. Open-source CAD files may be downloaded from various websites.

The work included in these drawings does not represent a legal contract; nor does it constitute architectural services. No person or organization makes any warranty, express or implied, regarding the information provided. The creator disclaims liability for any damages that may result from the use of these drawings.

This work is openly licensed under Creative Commons Attribution Share-Alike. See www.creativecommons.org/licenses/by-sa/3.0 for more details.

THESE DRAWINGS ARE FREE FOR YOU TO SHARE, MODIFY, AND DUPLICATE. THIS WORK DOES NOT REPRESENT A LEGAL CONTRACT OR CONSTITUTE ARCHITECTURAL SERVICES. NO PERSON OR ORGANIZATION MAKES ANY WARRANTY REGARDING THE INFORMATION PROVIDED. THE CREATORS DISCLAIM LIABILITY FOR ANY DAMAGES RESULTING FROM ITS USE. THIS WORK IS AVAILABLE UNDER A CREATIVE COMMONS ATTRIBUTION SHARE-A-LIKE LICENSE. SOME RIGHTS RESERVED.



OPEN-SOURCE
ARCHITECTURAL
DRAWING SET

A DESIGN BY JAY OSBORNE
AMERICAN FARMHOUSE
FREE FILES AVAILABLE AT [FREEFARMHOUSE.COM](https://freefarmhouse.com)


REVISIONS
02-14-2015
FIRST ONLINE RELEASE
12-31-2019
MINOR GRAPHIC EDITS
12-25-2020
RENAMED & REFINED

DATE
12-25-2020

SHEET TITLE
1ST FLOOR PLAN

SHEET NO.

A1.2

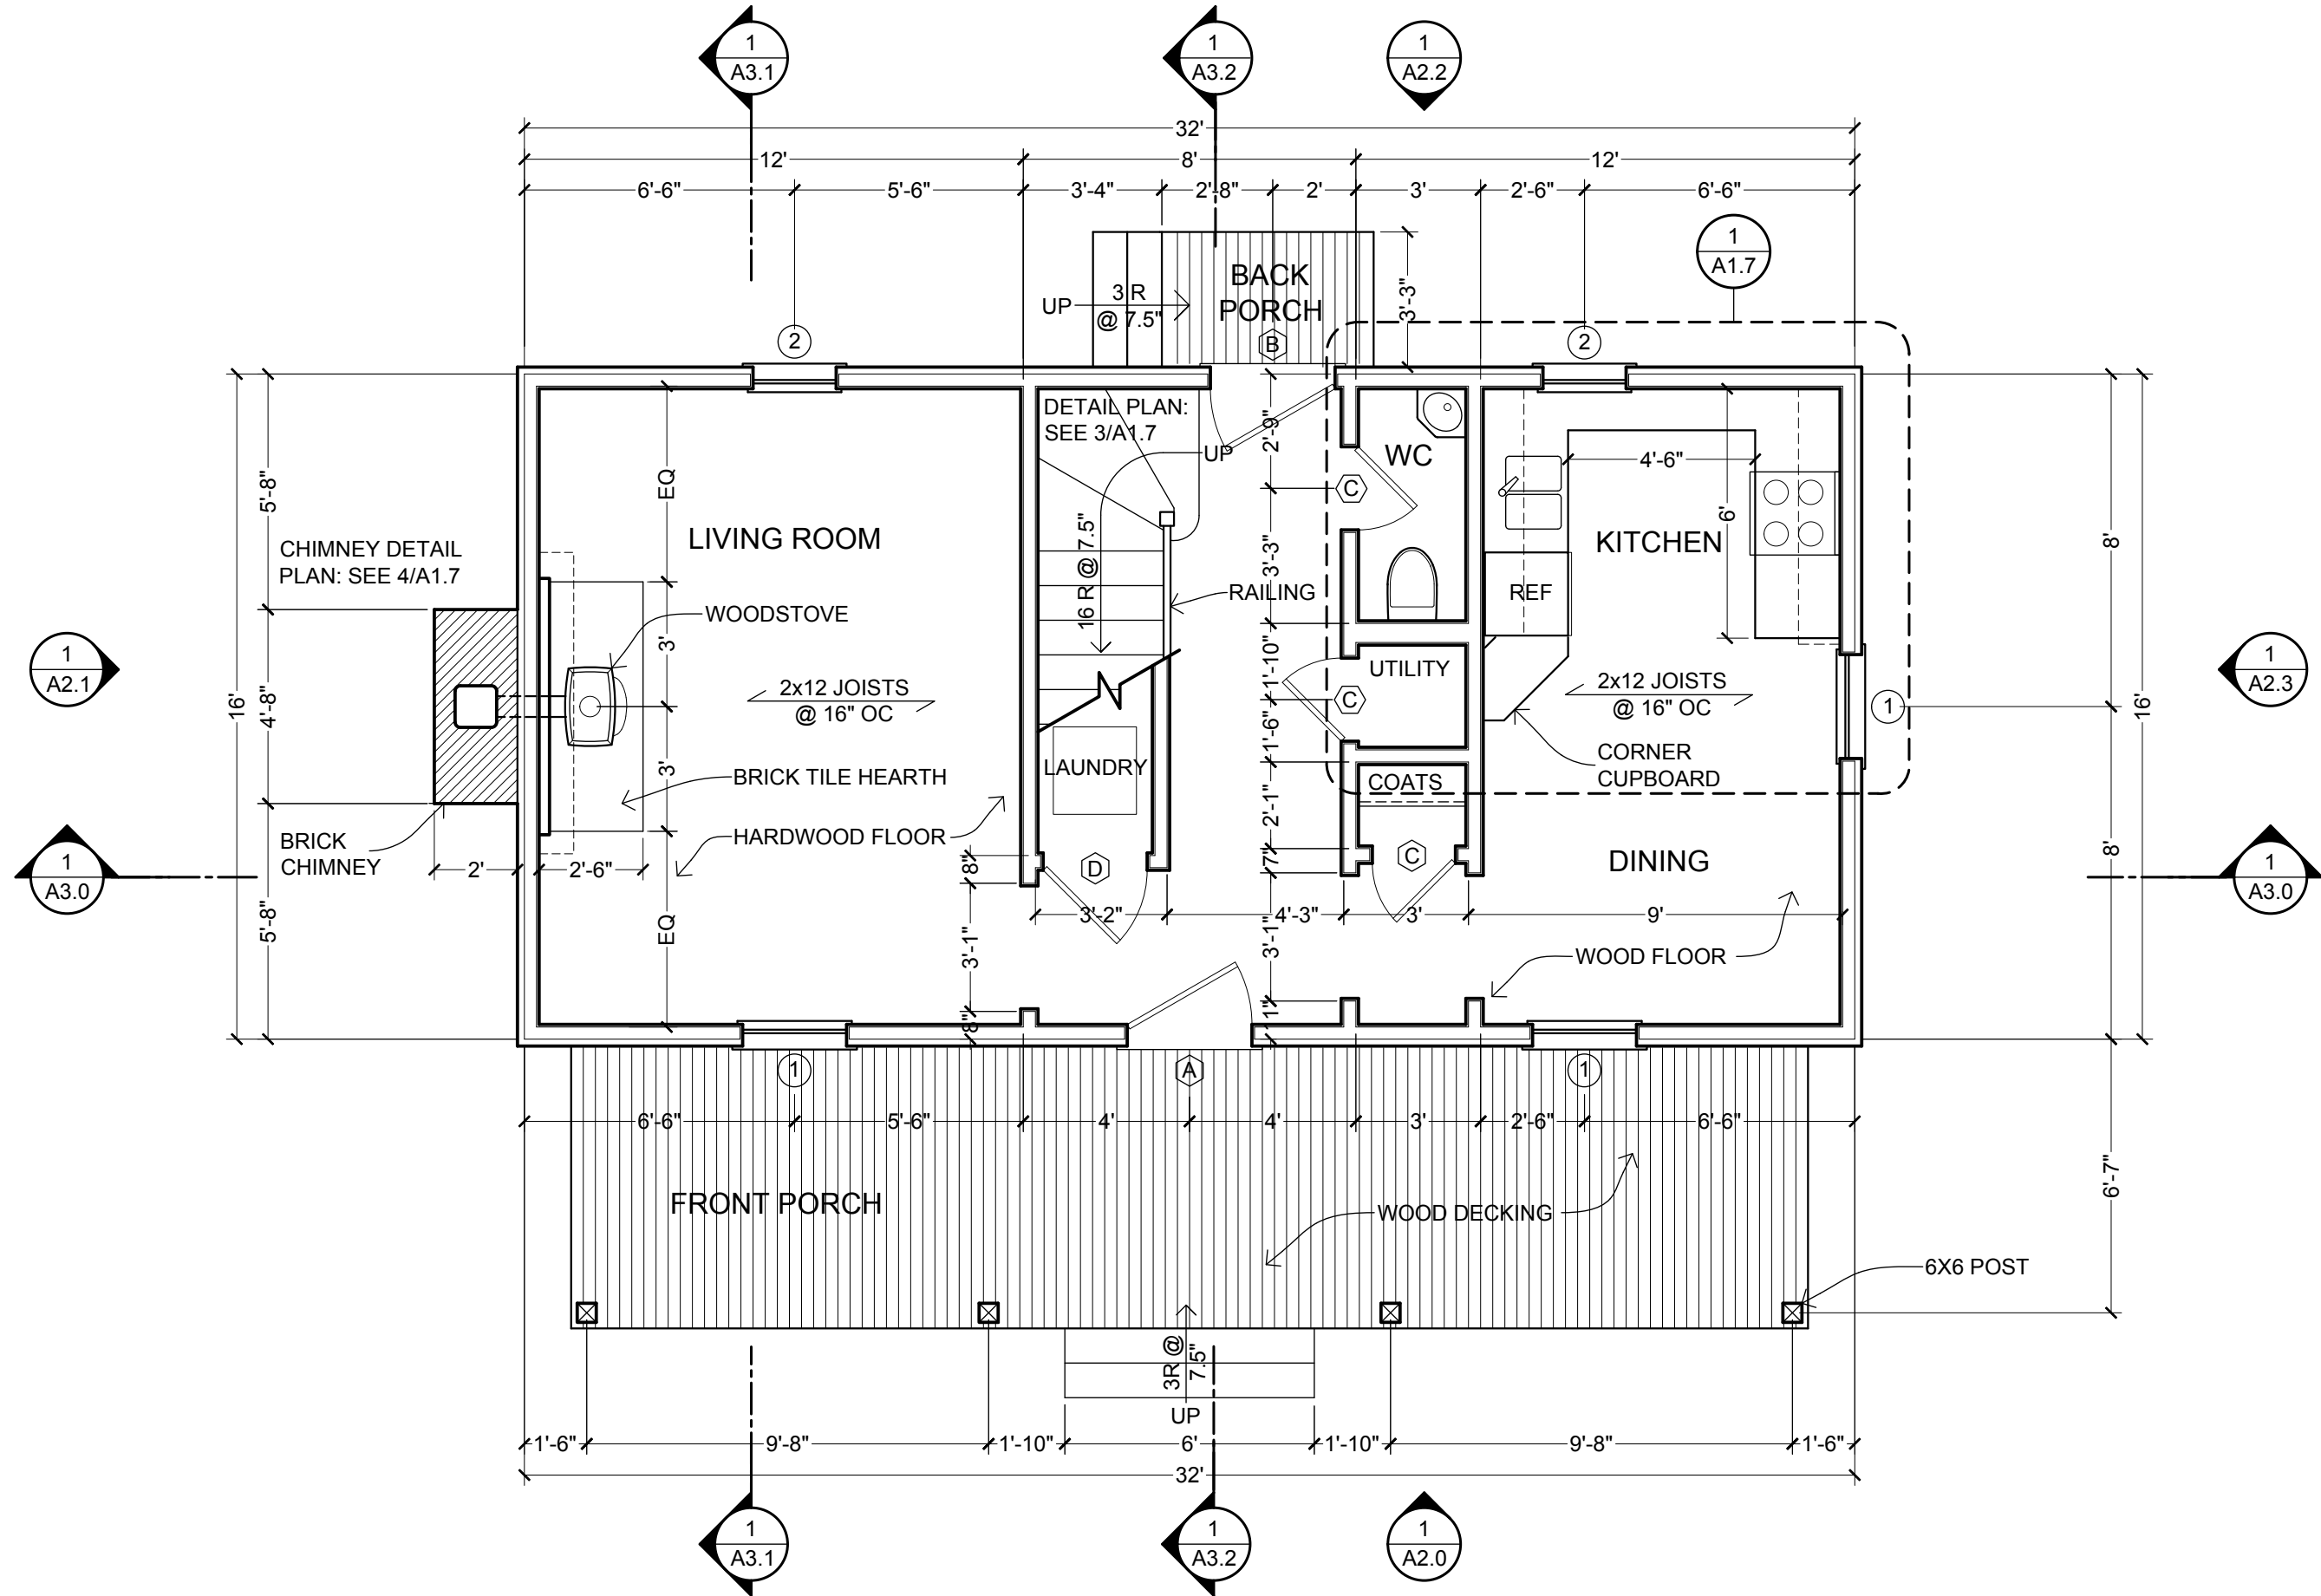

1 1ST FLOOR PLAN
SCALE: 1/4" = 1'-0"



THESE DRAWINGS ARE FREE FOR YOU TO SHARE, MODIFY, AND DUPLICATE. THIS WORK DOES NOT REPRESENT A LEGAL CONTRACT OR CONSTITUTE ARCHITECTURAL SERVICES. NO PERSON OR ORGANIZATION MAKES ANY WARRANTY REGARDING THE INFORMATION PROVIDED. THE CREATORS DISCLAIM LIABILITY FOR ANY DAMAGES RESULTING FROM ITS USE. THIS WORK IS AVAILABLE UNDER A CREATIVE COMMONS ATTRIBUTION SHARE-A-LIKE LICENSE. SOME RIGHTS RESERVED.



OPEN-SOURCE
ARCHITECTURAL
DRAWING SET

A DESIGN BY JAY OSBORNE
AMERICAN FARMHOUSE
FREE FILES AVAILABLE AT FREEFARMHOUSE.COM


REVISIONS	
02-14-2015	FIRST ONLINE RELEASE
12-31-2019	MINOR GRAPHIC EDITS
12-25-2020	RENAMED & REFINED

DATE
12-25-2020

SHEET TITLE
2ND FLOOR PLAN

SHEET NO.

A1.3

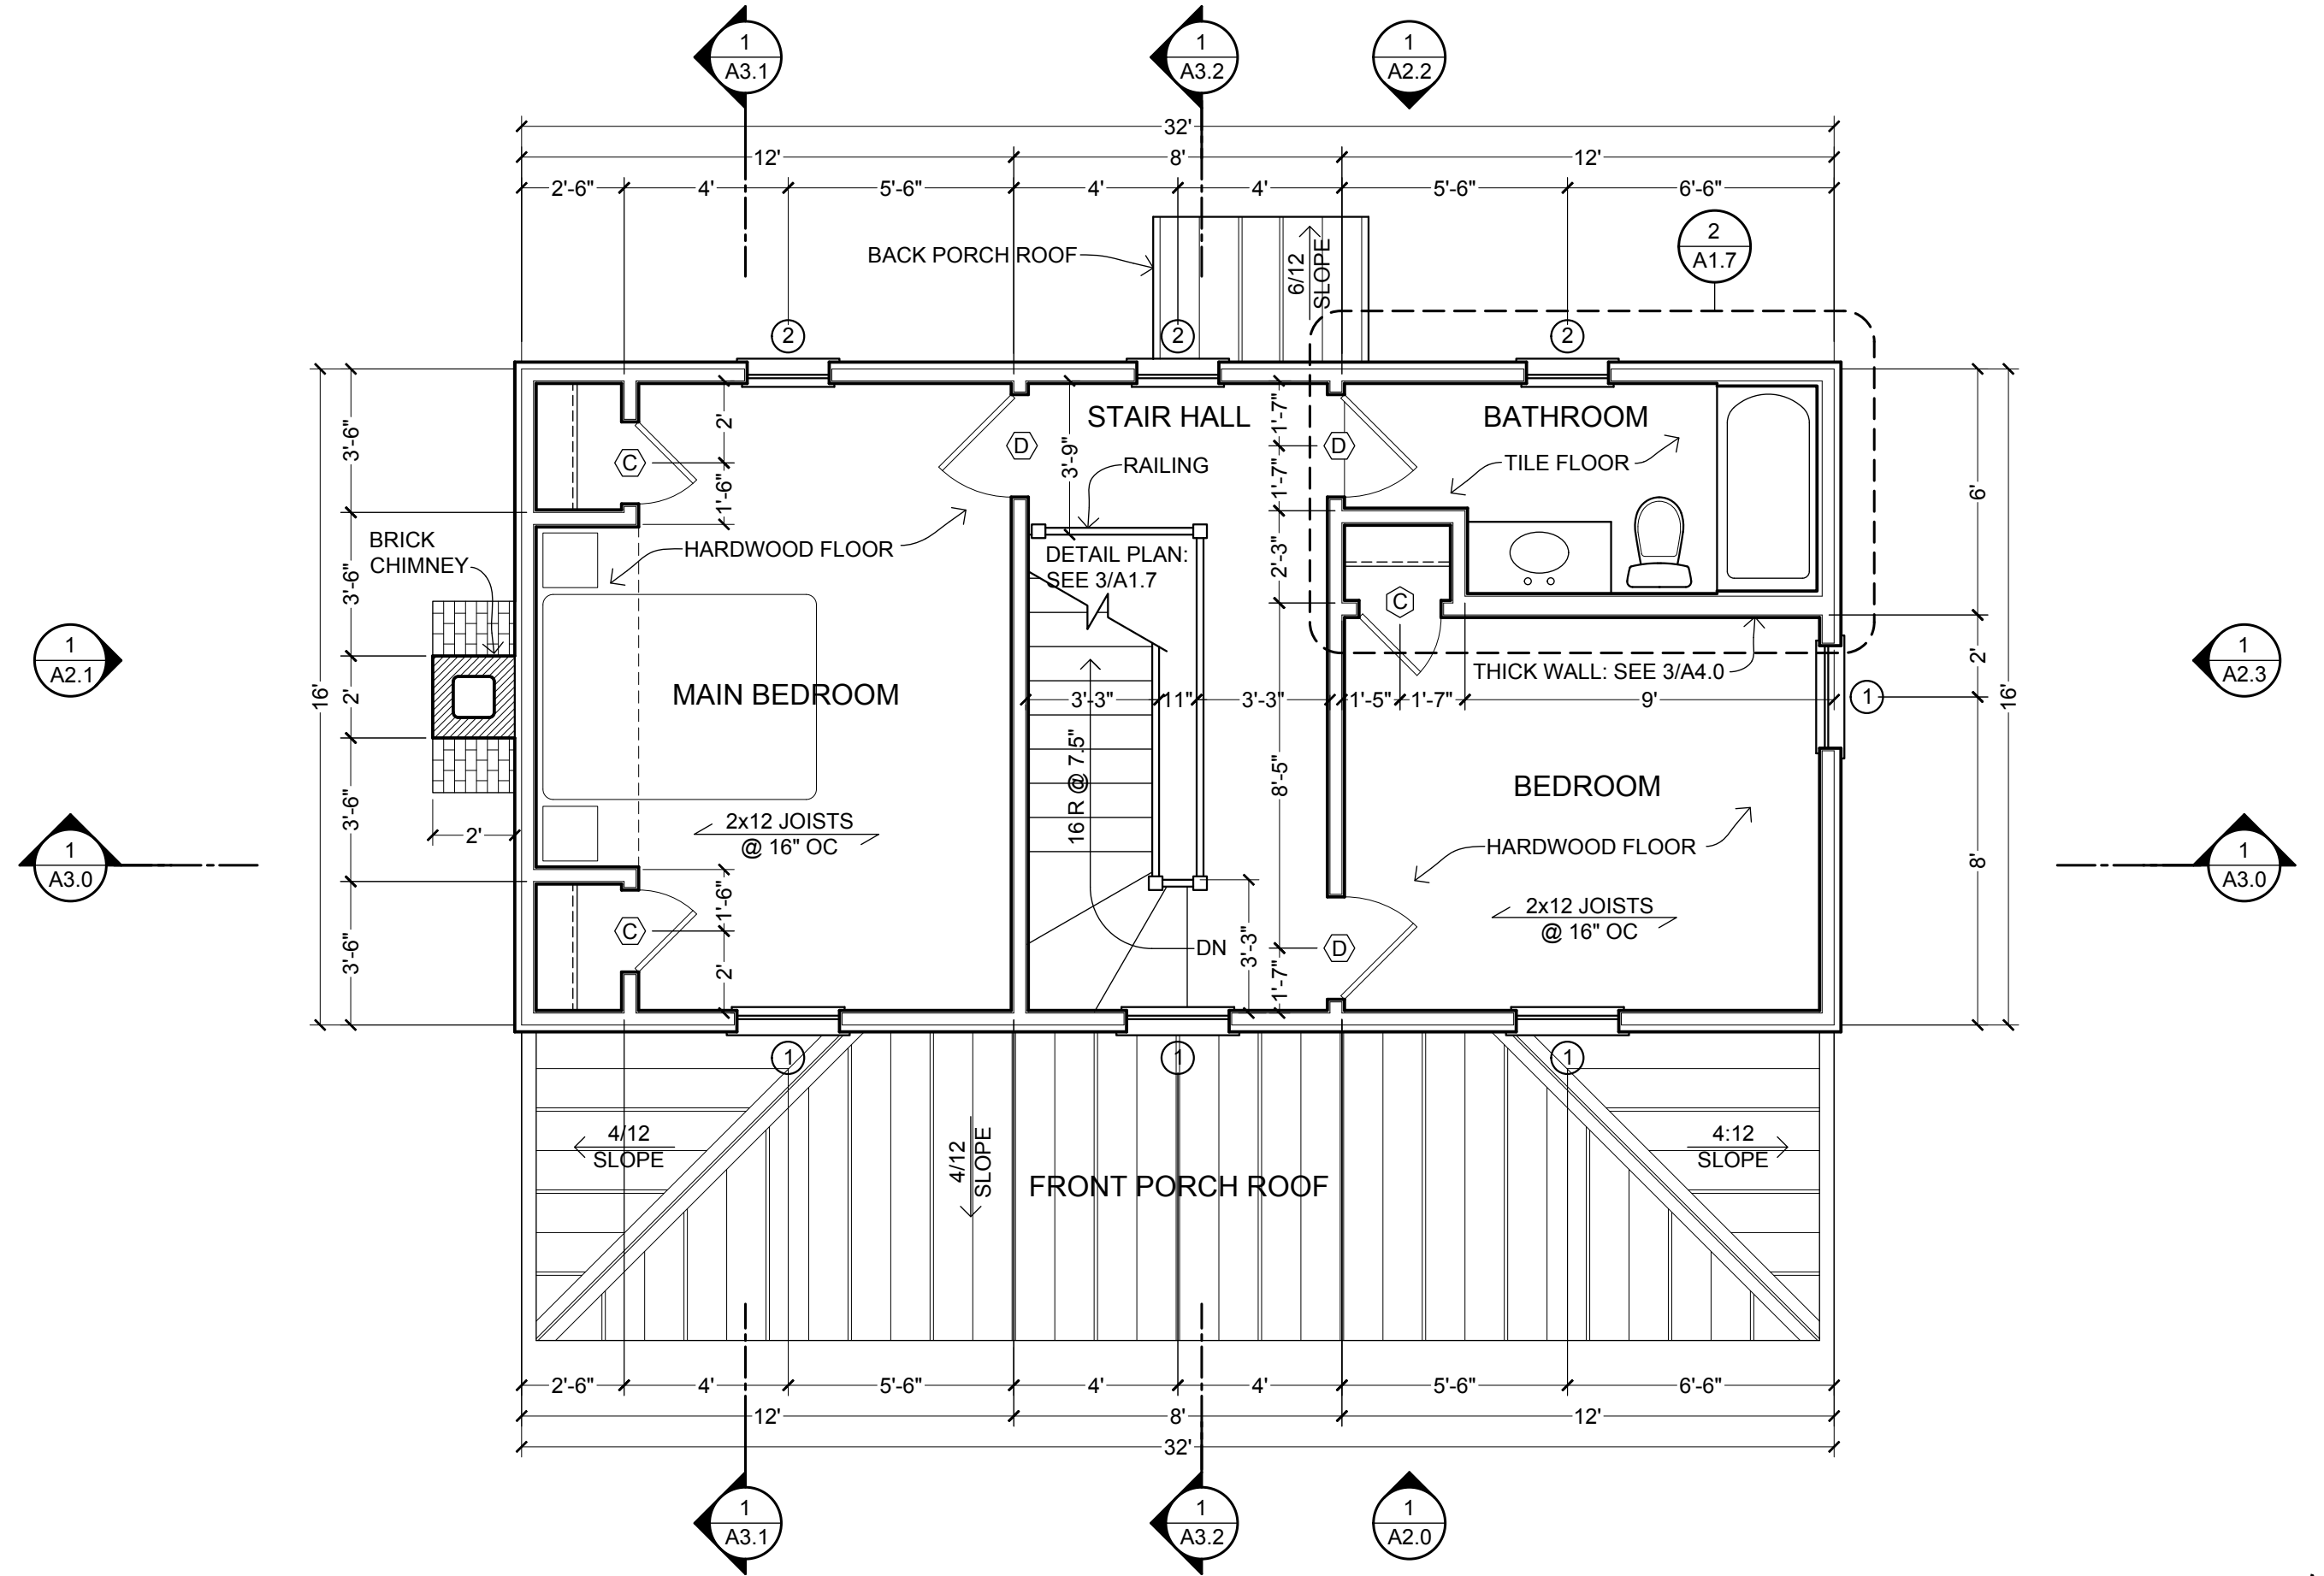

1 2ND FLOOR PLAN
SCALE: 1/4" = 1'-0"



THESE DRAWINGS ARE FREE FOR YOU TO SHARE, MODIFY, AND DUPLICATE. THIS WORK DOES NOT REPRESENT A LEGAL CONTRACT OR CONSTITUTE ARCHITECTURAL SERVICES. NO PERSON OR ORGANIZATION MAKES ANY WARRANTY REGARDING THE INFORMATION PROVIDED. THE CREATORS DISCLAIM LIABILITY FOR ANY DAMAGES RESULTING FROM ITS USE. THIS WORK IS AVAILABLE UNDER A CREATIVE COMMONS ATTRIBUTION SHARE-A-LIKE LICENSE. SOME RIGHTS RESERVED.


KEY NOTES

FIXTURES
(SEE SCHEDULE ON A5.0)


- X-00 REFRIGERATOR
- X-02 KITCHEN SINK
- X-04 RANGE / OVEN
- X-10 COUNTERTOP
- X-12 FLOOR CABINETS
- X-14 WALL CABINETS
- X-20 TOILET
- X-22 WC TOILET
- X-24 CORNER SINK
- X-26 VANITY
- X-28 BATHTUB
- X-40 WOODSTOVE
- X-42 CORNER CUPBOARD
- X-80 WATER HEATER

FINISHES
(SEE SCHEDULE ON A5.0)


- F-60 HARDWOOD FLOOR
- F-62 FLOOR TILE
- F-64 WALL TILE
- F-66 BRICK TILE
- F-68 BASE MOLDING
- F-72 OPENING CASING
- F-74 BEADBOARD
- F-76 WAINSCOT CAP
- F-78 HANDRAIL
- F-80 NEWEL POST

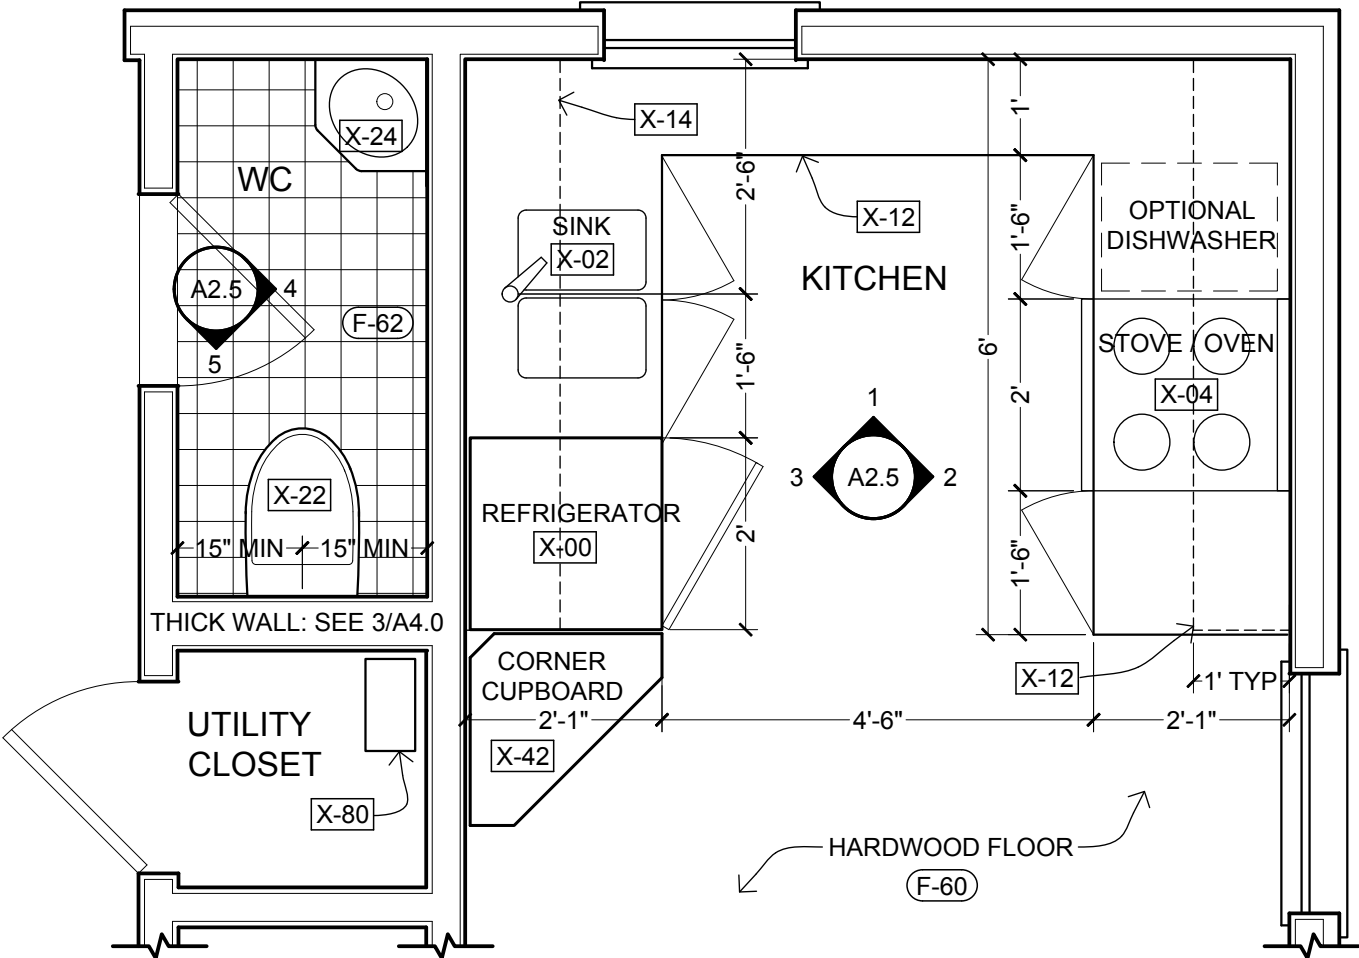


1 KITCHEN / WATER CLOSET - FLOOR PLAN DETAIL
SCALE: 1/2" = 1'-0" NOTE: DIMENSIONS ARE TO FINISHES

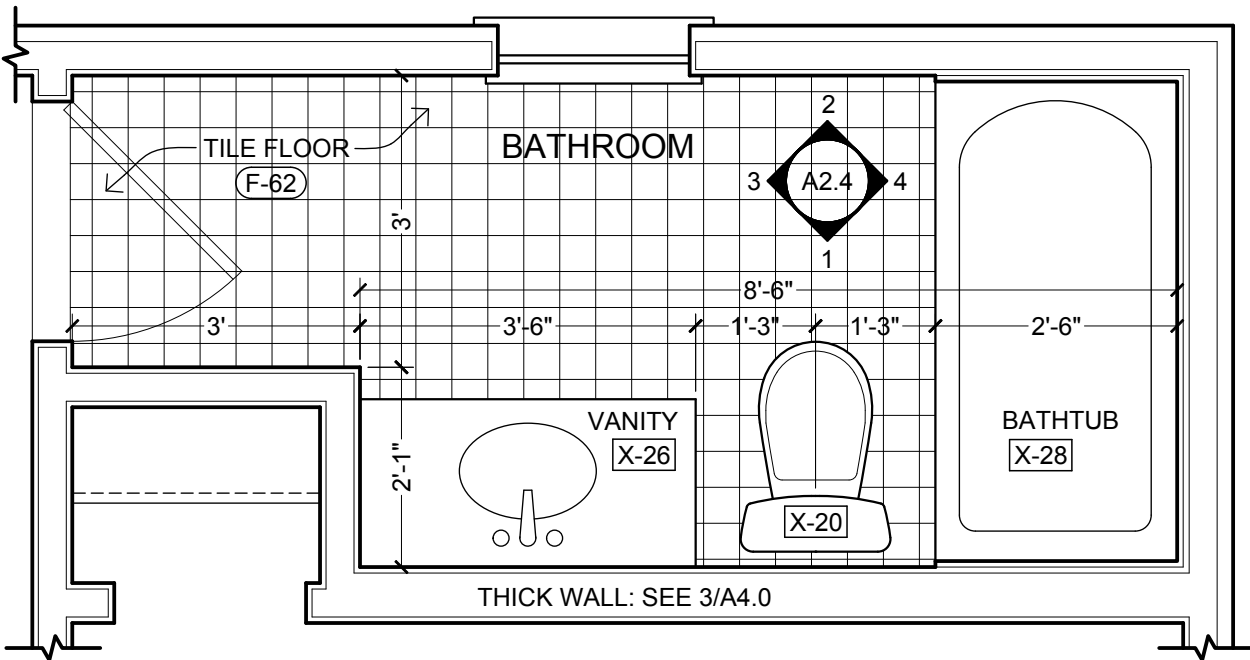

2 BATHROOM FLOOR PLAN DETAIL
SCALE: 1/2" = 1'-0" NOTE: DIMENSIONS ARE TO FINISHES

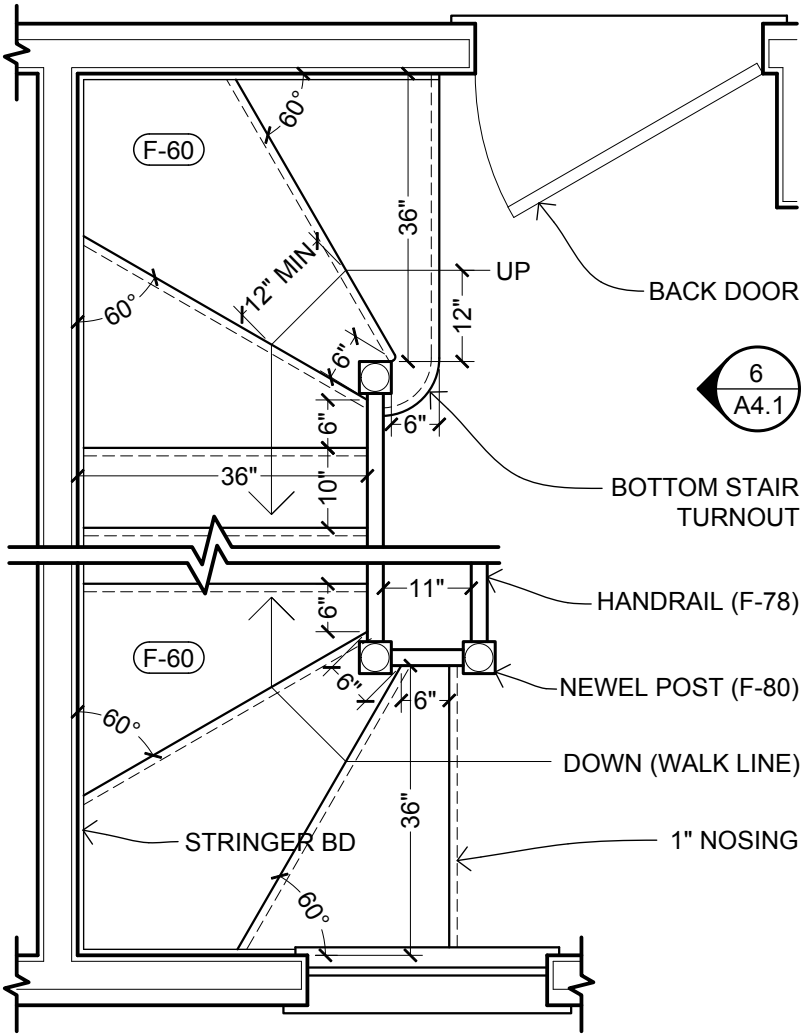

3 WINDER STAIRS - PLAN DETAIL
SCALE: 1/2" = 1'-0" NOTE: DIMENSIONS ARE TO FINISHES

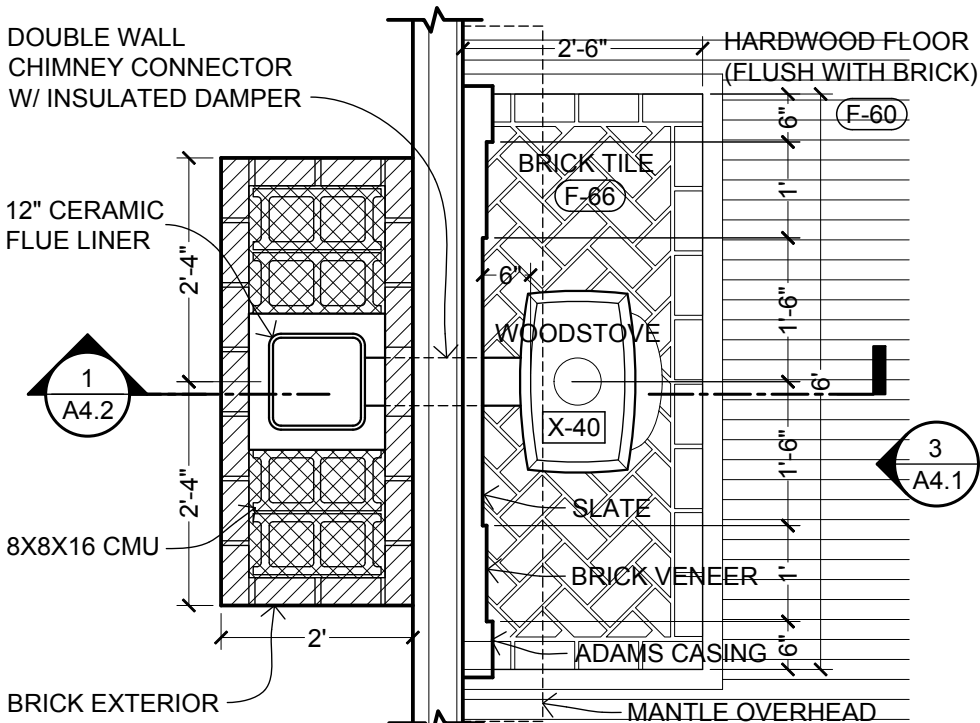

4 CHIMNEY / WOODSTOVE PLAN
SCALE: 1/2" = 1'-0" NOTE: DIMENSIONS ARE TO FINISHES



OPEN-SOURCE
ARCHITECTURAL
DRAWING SET

A DESIGN BY JAY OSBORNE
AMERICAN FARMHOUSE
FREE FILES AVAILABLE AT FREEFARMHOUSE.COM


REVISIONS
02-14-2015
FIRST ONLINE RELEASE
12-31-2019
MINOR GRAPHIC EDITS
12-25-2020
RENAMED & REFINED

DATE
12-25-2020

SHEET TITLE
DETAIL PLANS

SHEET NO.
A1.7

THESE DRAWINGS ARE FREE FOR YOU TO SHARE, MODIFY, AND DUPLICATE. THIS WORK DOESN'T REPRESENT A LEGAL CONTRACT OR CONSTITUTE ARCHITECTURAL SERVICES. NO PERSON OR ORGANIZATION MAKES ANY WARRANTY REGARDING THE INFORMATION PROVIDED. THE CREATORS DISCLAIM LIABILITY FOR ANY DAMAGES RESULTING FROM ITS USE. THIS WORK IS AVAILABLE UNDER A CREATIVE COMMONS ATTRIBUTION SHARE-A-LIKE LICENSE. SOME RIGHTS RESERVED.

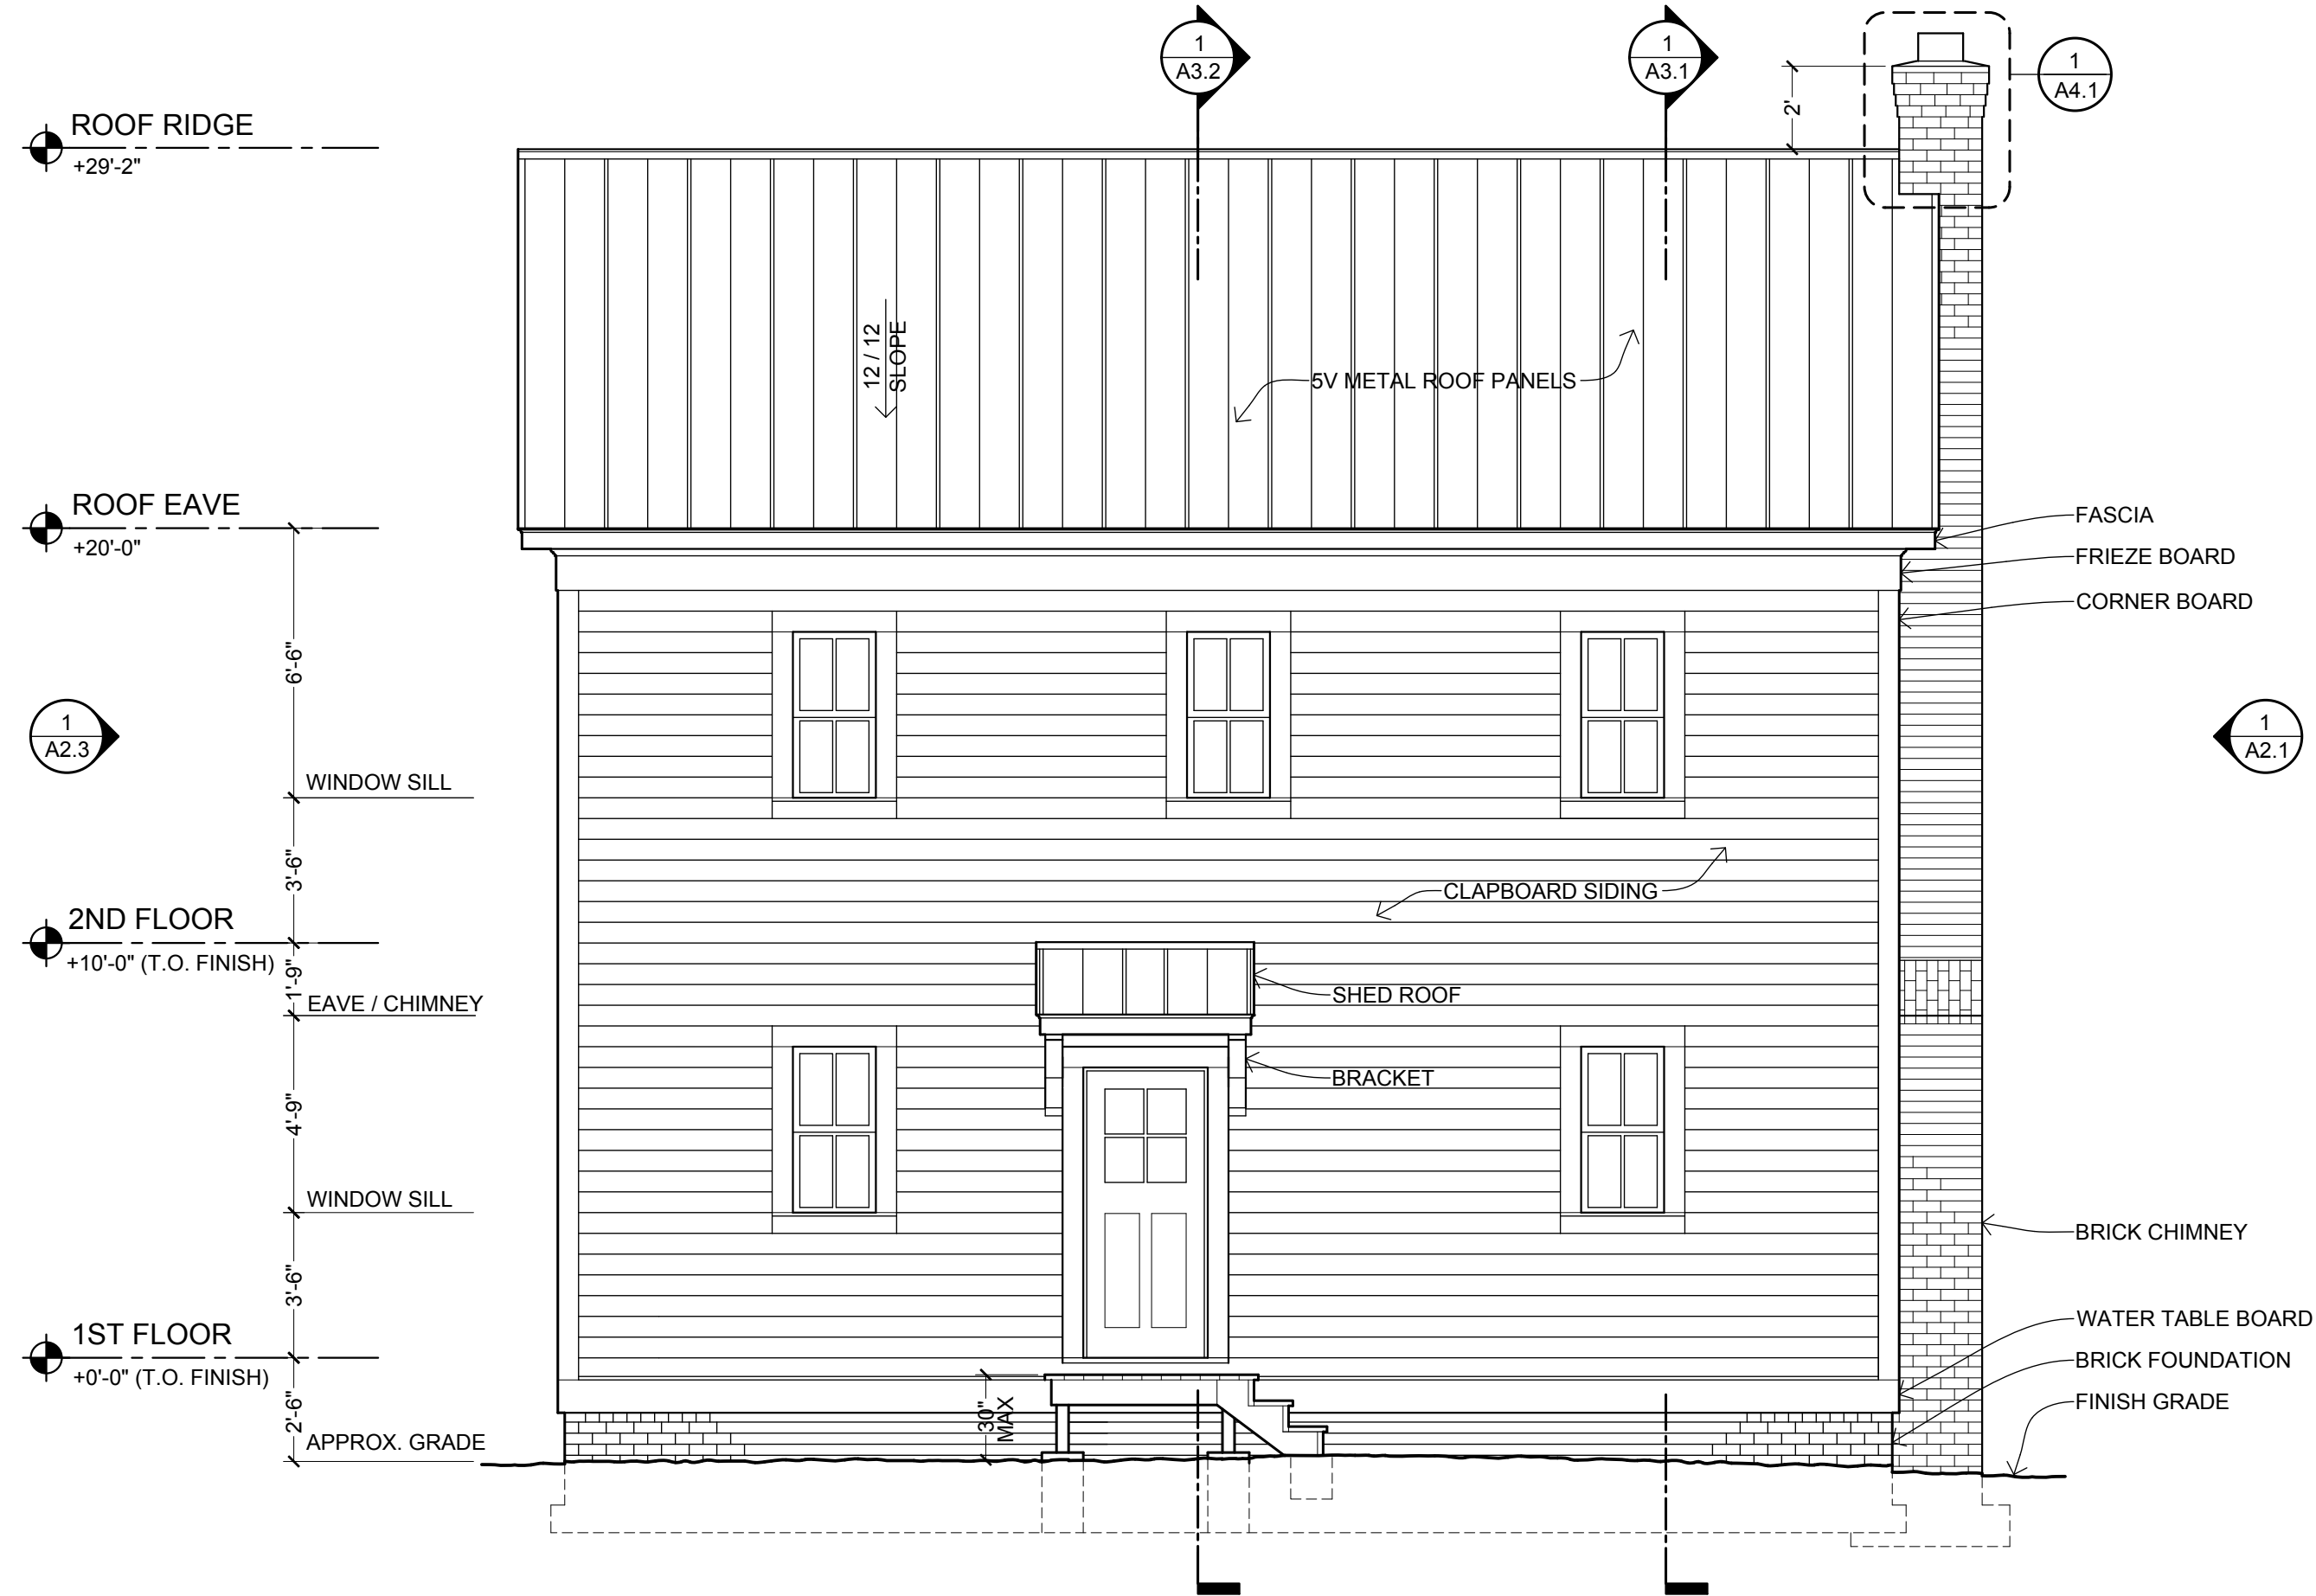

1 BACK ELEVATION (NORTH)
SCALE: 1/4" = 1'-0"



OPEN-SOURCE
ARCHITECTURAL
DRAWING SET

A DESIGN BY JAY OSBORNE
AMERICAN FARMHOUSE
FREE FILES AVAILABLE AT FREEFARMHOUSE.COM

REVISIONS
02-14-2015
FIRST ONLINE RELEASE
12-31-2019
MINOR GRAPHIC EDITS
12-25-2020
RENAMED & REFINED


DATE
12-25-2020

SHEET TITLE
**NORTH
ELEVATION**


SHEET NO.

A2.2


THESE DRAWINGS ARE FREE FOR YOU TO SHARE, MODIFY, AND DUPLICATE. THIS WORK DOES NOT REPRESENT A LEGAL CONTRACT OR CONSTITUTE ARCHITECTURAL SERVICES. NO PERSON OR ORGANIZATION MAKES ANY WARRANTY REGARDING THE INFORMATION PROVIDED. THE CREATORS DISCLAIM LIABILITY FOR ANY DAMAGES RESULTING FROM ITS USE. THIS WORK IS AVAILABLE UNDER A CREATIVE COMMONS ATTRIBUTION SHARE-A-LIKE LICENSE. SOME RIGHTS RESERVED.

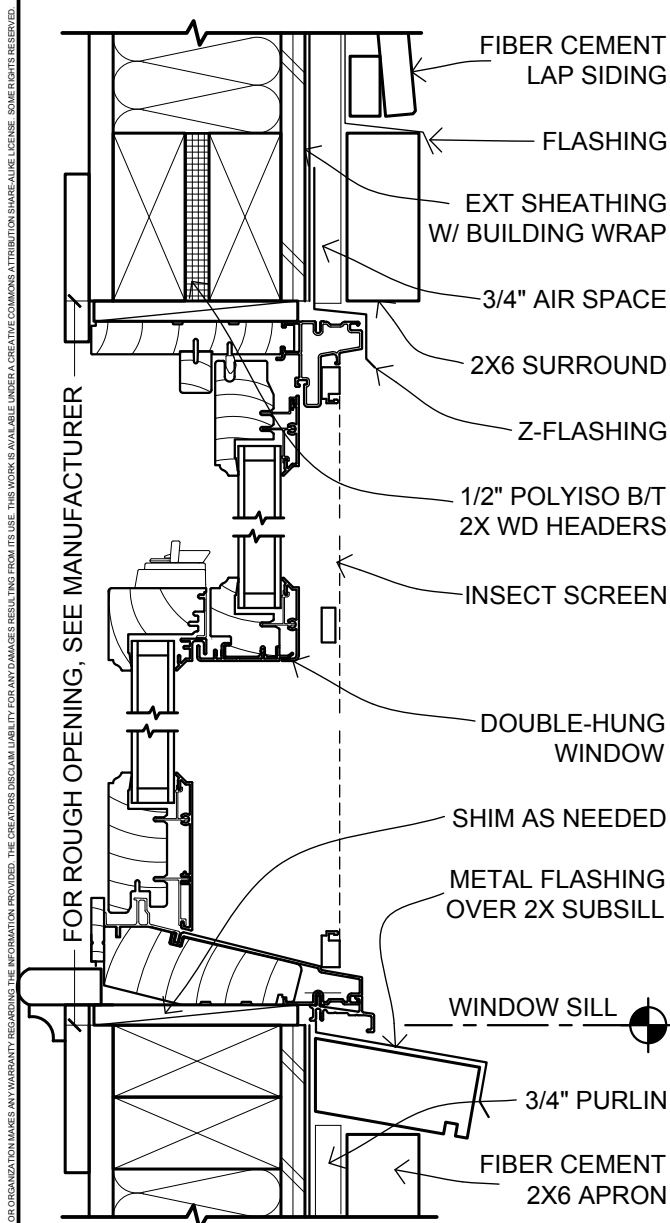


1 WINDOW DETAIL @ HEAD & SILL
SCALE: 3" = 1'-0"

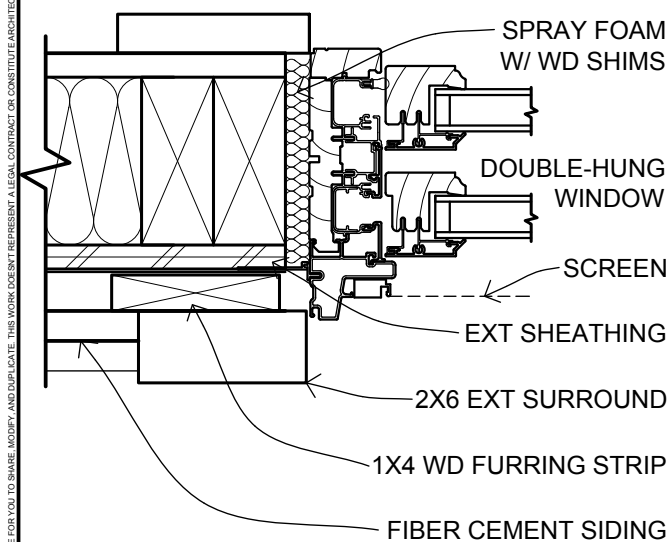


2 WINDOW DETAIL @ JAMB
SCALE: 3" = 1'-0"

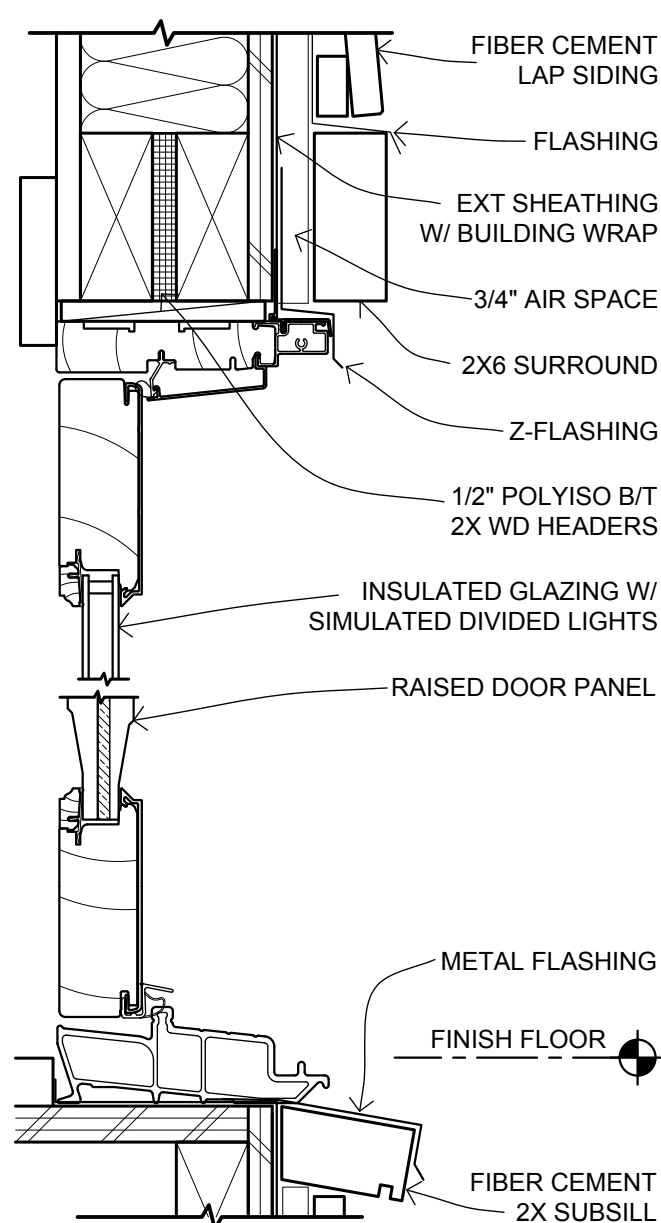


3 EXTERIOR DOOR HEAD & SILL
SCALE: 3" = 1'-0"

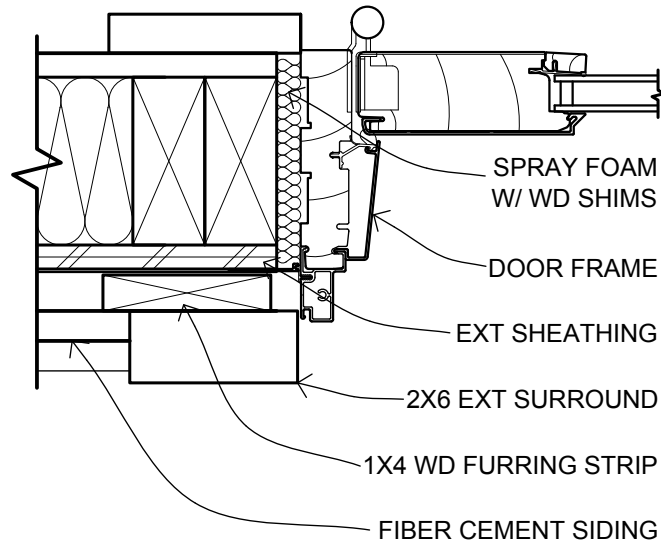


4 EXTERIOR DOOR DETAIL @ JAMB
SCALE: 3" = 1'-0"

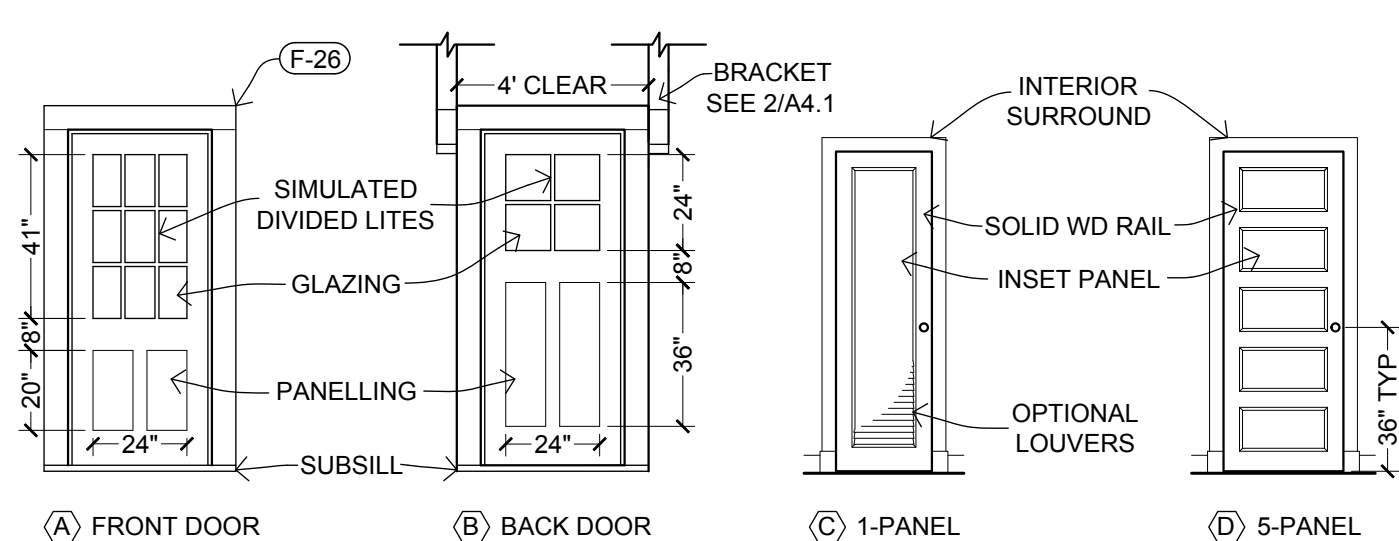

5 DOOR ELEVATION DETAILS
SCALE: 1/4" = 1'-0"

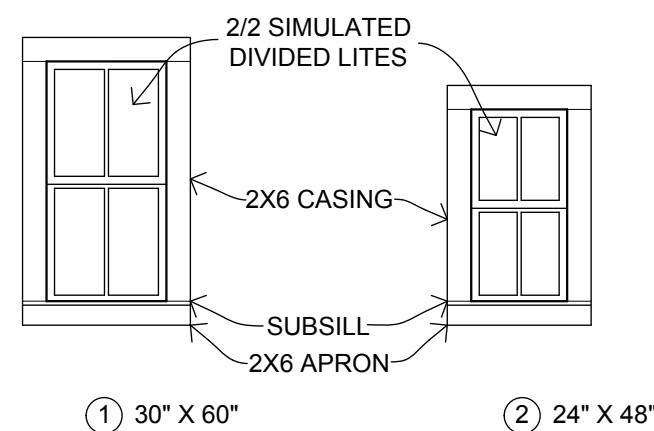

6 WINDOW ELEVATION DETAILS
SCALE: 1/4" = 1'-0"

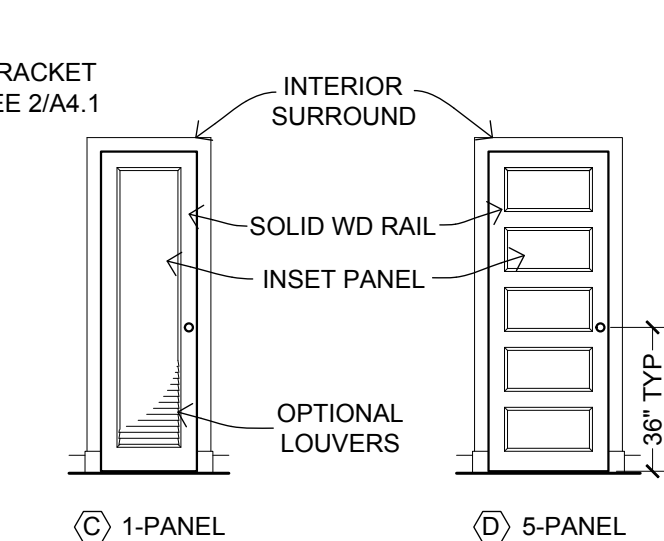

7 OPTIONAL WINDOW SHUTTERS
SCALE: 1/4" = 1'-0"

DOOR SCHEDULE

MARK	SIZE	MATERIAL	TYPE	NOTE	MAKE / MODEL
(A)	36"x84"	COMPOSITE	GLAZED, PANELLED	3/3 LITES	MARVIN / CLAD ULTIMATE
(B)	36"x84"	COMPOSITE	GLAZED, PANELLED	2/2 LITES	MARVIN / CLAD ULTIMATE
(C)	24"x80"	WOOD	1-PANEL	SOLID WOOD	ANTIQUE PREFERRED
(D)	30"x80"	WOOD	5-PANEL	OPT LOUVERS	ANTIQUE PREFERRED

WINDOW SCHEDULE

MARK	SIZE	MATERIAL	TYPE	NOTE	MAKE / MODEL
1	30"x60"	COMPOSITE	DOUBLE HUNG	2/2 LITES	MARVIN / ULTIMATE DH
2	24"x48"	COMPOSITE	DOUBLE HUNG	2/2 LITES	MARVIN / ULTIMATE DH

FOR RELATED TRIM AND ACCESSORIES: SEE FINISHES SCHEDULE A5.0



OPEN-SOURCE
ARCHITECTURAL
DRAWING SET

A DESIGN BY JAY OSBORNE
AMERICAN FARMHOUSE
FREE FILES AVAILABLE AT FREEFARMHOUSE.COM

REVISIONS
02-14-2015
FIRST ONLINE RELEASE
12-31-2019
MINOR GRAPHIC EDITS
12-25-2020
RENAMED & REFINED

DATE
12-25-2020

SHEET TITLE
DOORS & WINDOWS

SHEET NO.

A4.3

THESE DRAWINGS ARE FREE FOR YOU TO SHARE, MODIFY, AND DUPLICATE. THIS WORK DOESN'T REPRESENT A LEGAL CONTRACT OR CONSTITUTE ARCHITECTURAL SERVICES. NO PERSON OR ORGANIZATION MAKES ANY WARRANTY REGARDING THE INFORMATION PROVIDED. THE CREATORS DISCLAIM LIABILITY FOR ANY DAMAGES RESULTING FROM ITS USE. THIS WORK IS AVAILABLE UNDER A CREATIVE COMMONS ATTRIBUTION SHARE-A-LIKE LICENSE. SOME RIGHTS RESERVED.

MATERIALS SCHEDULE

MARK	ITEM	SIZE	MATERIAL	NOTES	MANUFACTURER / MODEL
F-00	BRICK	-	SMOOTH BRICK	RED COLOR, SAND-FACED, AVOID WIRE CUT OR "EXTRUDED" LOOK	-
F-20	FLOOR DECKING	1x4	PAINTED WOOD	TONGUE & GROOVE, UNPAINTED CEDAR PREFERRED	-
F-22	PORCH COLUMN	6x6	WOOD	CHAMFERED 1" FROM EDGES	-
F-24	CLAPBOARD SIDING	6"	FIBER CEMENT	JAMES HARDIE / ARTISAN LAP SIDING	-
F-26	EXT OPENING CASING	5-6"	FIBER CEMENT	.75" THICK HARDIPLANK	-
F-28	BED MOLDING	2.5"	ROT-RESISTANT	PAINTED	-
F-30	ASTRAGAL	1"	ROT-RESISTANT	PAINTED	-
F-32	CROWN MOLDING	3"	ROT-RESISTANT	PAINTED	-
F-40	5V METAL ROOF PANELS	24"OC	GALVALUME	OPTIONAL: STANDING SEAM METAL ROOF PANELS	-
F-42	BULBED RIDGE CAP	4"	GALVALUME	USE SAME SUPPLIER AND PRODUCT LINE AS 5V PANELS	-
F-44	HALF-ROUND GUTTER	5" DIA	GALV STEEL OR COPPER	DOWNSPOUTS TO FOLLOW CORNER BOARDS	-
F-52	CHIMNEY CAP	~2'X2'	CONCRETE	MINIMAL PROFILE, OPTIONAL: SPARK ARRESTOR OR CHIMNEY POT	-
F-60	HARDWOOD FLOOR	2-3" WIDE	FINISH WOOD	TONGUE & GROOVE, STAINED	-
F-62	FLOOR TILE	~2"	CERAMIC	HEXAGONAL PATTERN	-
F-64	WALL TILE	4" SQUARE	CERAMIC	WHITE OR LIGHT BLUE	-
F-66	BRICK TILE	1/2" THICK	RECLAIMED BRICK	THIN BRICK VENEER, NARROW (1/4") MORTAR JOINTS, SMOOTH RED COLOR	-
F-68	BASE MOLDING	.5"X4"	FINISH WOOD	INCLUDE DECORATIVE BASE CAP MOLDING	-
F-72	INT OPENING CASING	.5"X4"	WOOD	PAINTED, WITH .75"-THICK PLINTH BLOCK AT BASE	-
F-74	BEADBOARD	1/2"	COMPOSITE PANEL	EXTERIOR GRADE BEADBOARD TO BE USED AT PORCH	-
F-76	WAINSCOT CAP	-	WOOD	PAINTED	-
F-78	HANDRAIL	2"	FINISH WOOD	STAINED SAME COLOR AS FLOOR	-
F-80	NEWEL POST	4x4	WOOD	PAINTED, MODESTLY DECORATIVE	-
F-82	CROWN MOLDING	-	WOOD OR MDF	PAINTED	-
F-90	WINDOW SHUTTERS	15"x60"	WOOD	SHALL BE OPERABLE. LOUVERS PREFERRED.	-

FIXTURE & EQUIPMENT SCHEDULE

MARK	ITEM	SIZE	NOTES	MANUFACTURER / MODEL
X-00	REFRIGERATOR	25x25x69"	ENERGY STAR	BLOMBERG / BRFB1042SS
X-02	KITCHEN SINK	24"x18"	SINGLE BOWL, VITREOUS CHINA	HIGHPOINT COLLECTION / FIRECLAY
X-04	RANGE / OVEN	24"x24"x36"	-	-
X-10	KITCHEN COUNTERTOP	2" THICK	WHITE PORCELEIN TILE OVER COMPOSITE BOARD	IKEA / AKERBY
X-12	FLOOR CABINETS	12", 24" WIDE	PAINTED, STAT WHITE, BIRCH EFFECT, INCLUDE NON-STANDARD 12" SHELVES	IKEA / AKURUM
X-14	WALL CABINETS	12" WIDE	PAINTED, GLAZED DOORS PREFERRED	IKEA / AKURUM
X-20	TOILET	26"x18"	1.0 GPF	TOTO / ROWAN CST405MF OR EQUIVALENT
X-22	WC TOILET	2' MAX LENGTH	WALL HUNG, 1.6 GPF, SIZE IS CRITICAL FOR PROPER CLEARANCES	AQUIA / WALL HUNG DUAL FLUSH TOILET CT418F
X-24	CORNER SINK	16"x16" MAX	VITREOUS CHINA, WALL HUNG OR PEDESTAL, SIZE CRITICAL FOR CLEARANCES	ELIZABETHAN CLASSICS / ETCB CORNER BASIN
X-26	BATHROOM VANITY	21"x42"	CENTERED WITH MIRROR WALL CABINET	CHOICE BY OWNER
X-28	BATHTUB	30"x60"x18"	INSTALL LOW-FLOW SHOWER HEAD	KOHLER / STERLING 71091120 OR EQUIVALENT
X-30	MIRROR CABINET	25"x38"x6"	WHITE FRAME, OPTIONAL CASING SURROUND, CENTERED ON SINK	IKEA / HEMNES OR EQUIVALENT
X-40	WOODSTOVE	14"x19"x22"	USE DOUBLE WALL CONNECTOR PIPE	JOTUL / F3 CB
X-42	CORNER CUPBOARD	~24"x24"x80"	GLAZED DOORS, AVOID CHEAP VENEERS, A "BOOKEND" FOR THE KITCHEN	ANTIQUE PREFERRED
X-44	WASHER / DRYER COMBO	24"x34"x23"	VENTLESS, ENERGY STAR PREFERRED, FITS BELOW STAIRCASE	HAIER / HWD1600BW
X-80	WATER HEATER	8"x7"x3"	INSTANT, TANKLESS, UNDERCOUNTER	STIEBEL / ELTRON MINI
X-84	INTERIOR CEILING FAN	48" DIA MAX	INCLUDES LIGHTING	-
X-86	EXTERIOR CEILING FAN	60" DIA MAX	INCLUDES LIGHTING	-

FOR WINDOW & DOOR SCHEDULES: SEE SHEET A4.3
PREFERENCE SHALL BE GIVEN TO LOCALLY PRODUCED OR SALVAGED ANTIQUE MATERIALS



OPEN-SOURCE
ARCHITECTURAL
DRAWING SET

A DESIGN BY JAY OSBORNE
AMERICAN FARMHOUSE
FREE FILES AVAILABLE AT FREEFARMHOUSE.COM

REVISIONS
02-14-2015
FIRST ONLINE RELEASE
12-31-2019
MINOR GRAPHIC EDITS
12-25-2020
RENAMED & REFINED

DATE
12-25-2020

SHEET TITLE
SCHEDULES

SHEET NO.
A5.0