



NO.	EXTERIOR MATERIALS
1	BLACK ASPHALT SHINGLES
2	WHITE 6" FASCIA
3	BEIGE VINYL SIDING
4	NATURAL FINISH CEDAR SHAKES
5	PRESSURE TREATED DECK LEDGER

 EAST ELEVATION
SCALE: 3/16"=1'-0"

This drawing set is intended to act as an example of drawing standards and may not be reproduced without permission. Any similarities with actual buildings and or locations is coincidental. Refer to the requirements list for complete drawing requirements.

Revisions:	


Issued For:	

Consultants/Seals:	

MUNICIPAL ADDRESS:
3615 4 ST SW
LEGAL ADDRESS:
4647GU; A; 7,8

Drawing Name:
EAST ELEVATION (FRONT)

Drawn:	Checked:
Date:	
Drawing Scale:	3/16"=1'-0"
Consultant Project Number:	
Project Number:	Sheet:
	4 OF 23
Consultant File Number:	
File Number:	

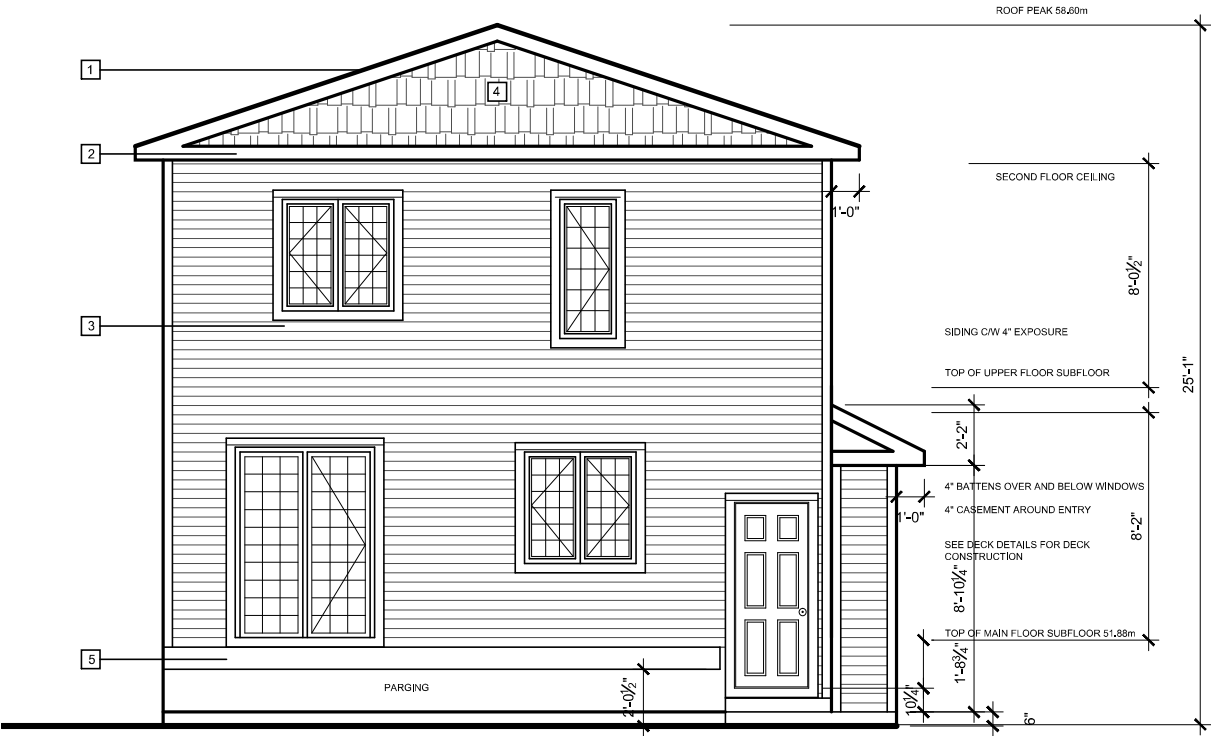

NO.	EXTERIOR MATERIALS
1	BLACK ASPHALT SHINGLES
2	WHITE 6" FASCIA
3	BEIGE VINYL SIDING
4	NATURAL FINISH CEDAR SHAKES
5	PRESSURE TREATED DECK LEDGER

 **WEST ELEVATION**
SCALE: 3/16"=1'-0"

This drawing set is intended to act as an example of drawing standards and may not be reproduced without permission. Any similarities with actual buildings and or locations is coincidental. Refer to the requirements list for complete drawing requirements.

Revisions:	

Issued For:	

Consultants/Seals:	

MUNICIPAL ADDRESS:
3615 4 ST SW
LEGAL ADDRESS:
4647GU; A; 7,8

Drawing Name:
WEST ELEVATION

Drawn: _____ Checked: _____

Date: _____


Drawing Scale: **3/16"=1'-0"**

Consultant Project Number: _____

Project Number: _____ Sheet: **5 OF 23**

Consultant File Number: _____

File Number: _____

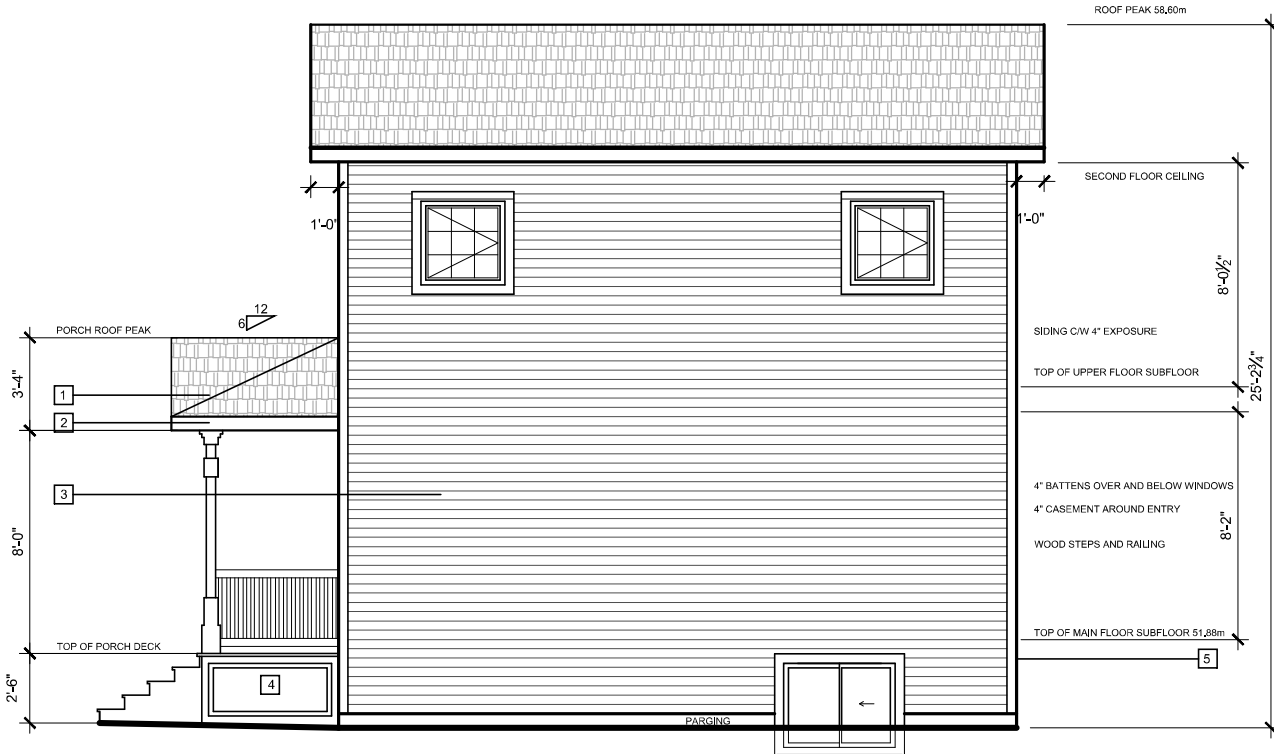

NO.	EXTERIOR MATERIALS
1	BLACK ASPHALT SHINGLES
2	WHITE 6" FASCIA
3	BEIGE VINYL SIDING
4	NATURAL FINISH CEDAR SHAKES
5	PRESSURE TREATED DECK LEDGER

SPATIAL CALCULATION	
WALL AREA	494,27 ft2
WINDOW AREA	27,25 ft2
TOTAL %	5,51%
ALLOWABLE %	23,5%

 NORTH ELEVATION
SCALE: 3/16"=1'-0"

This drawing set is intended to act as an example of drawing standards and may not be reproduced without permission. Any similarities with actual buildings and or locations is coincidental. Refer to the requirements list for complete drawing requirements.

Revisions:	
RIGHT SIDE	


Issued For:	


Consultants/Seals:	

MUNICIPAL ADDRESS:
3615 4 ST SW
LEGAL ADDRESS:
4647GU; A; 7,8

Drawing Name:
NORTH ELEVATION
RIGHT SIDE

Drawn:	Checked:
Date:	
Drawing Scale:	3/16"=1'-0"
Consultant Project Number:	
Project Number:	Sheet:
	6 OF 23
Consultant File Number:	
File Number:	

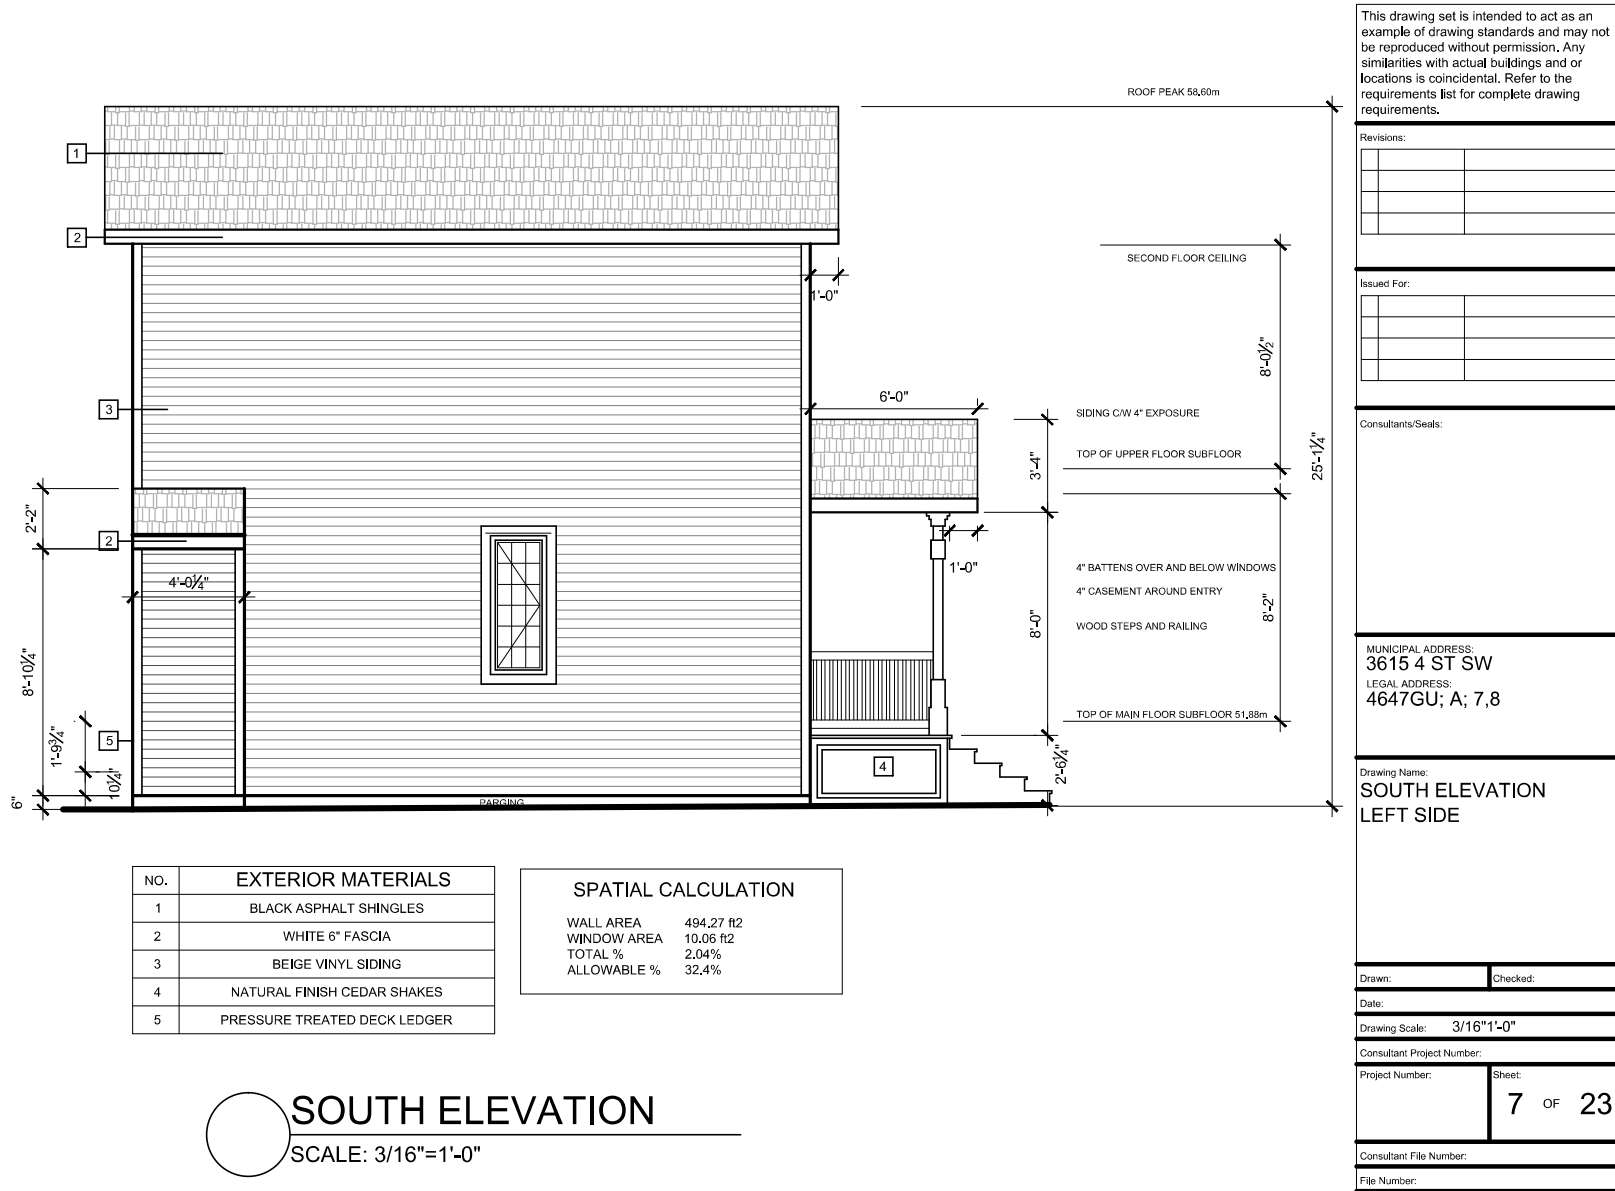

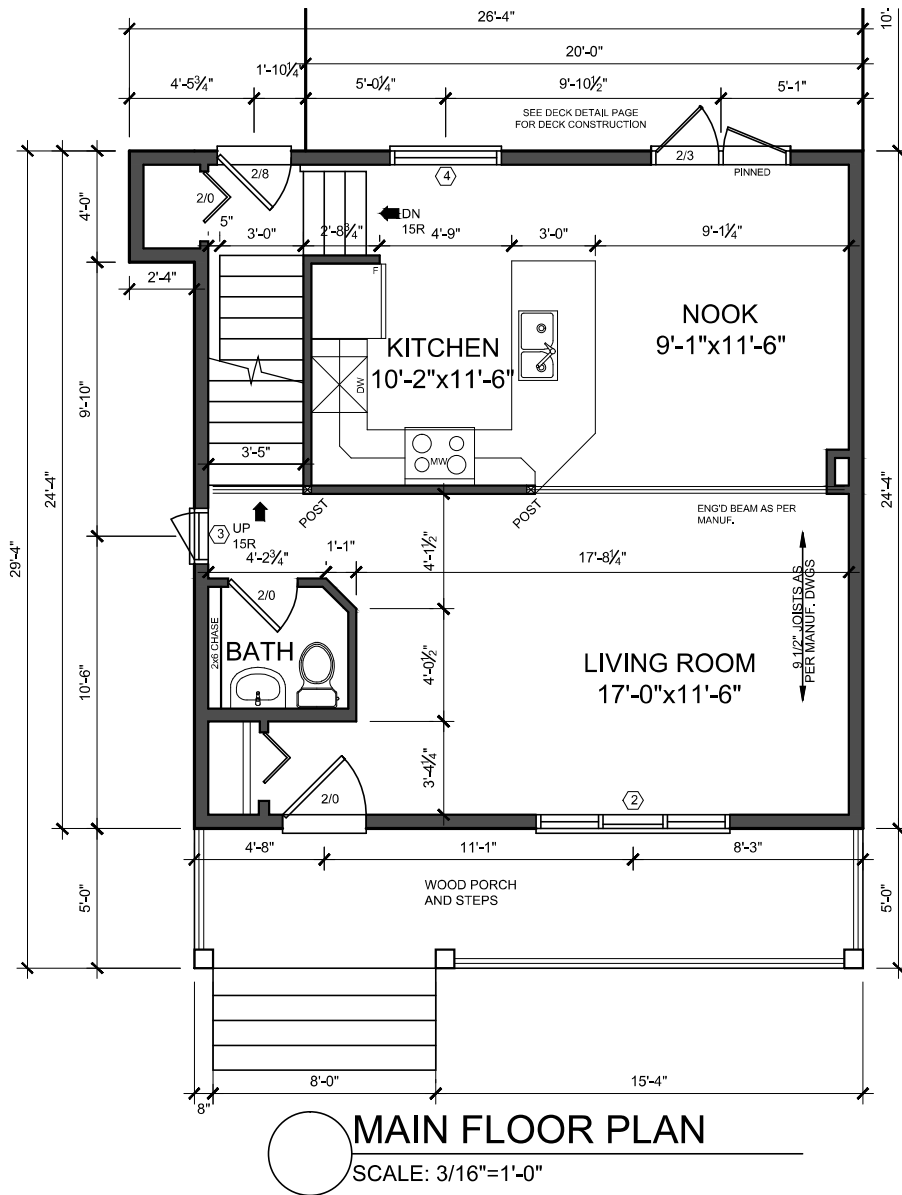

This drawing set is intended to act as an example of drawing standards and may not be reproduced without permission. Any similarities with actual buildings and or locations is coincidental. Refer to the requirements list for complete drawing requirements.

Revisions:	


Issued For:	

Consultants/Seals:

MUNICIPAL ADDRESS:
 3615 4 ST SW
 LEGAL ADDRESS:
 4647GU; A; 7,8

Drawing Name:
MAIN FLOOR PLAN

Drawn:	Checked:
Date:	
Drawing Scale:	3/16"=1'-0"
Consultant Project Number:	
Project Number:	Sheet:
	9 OF 23
Consultant File Number:	
File Number:	

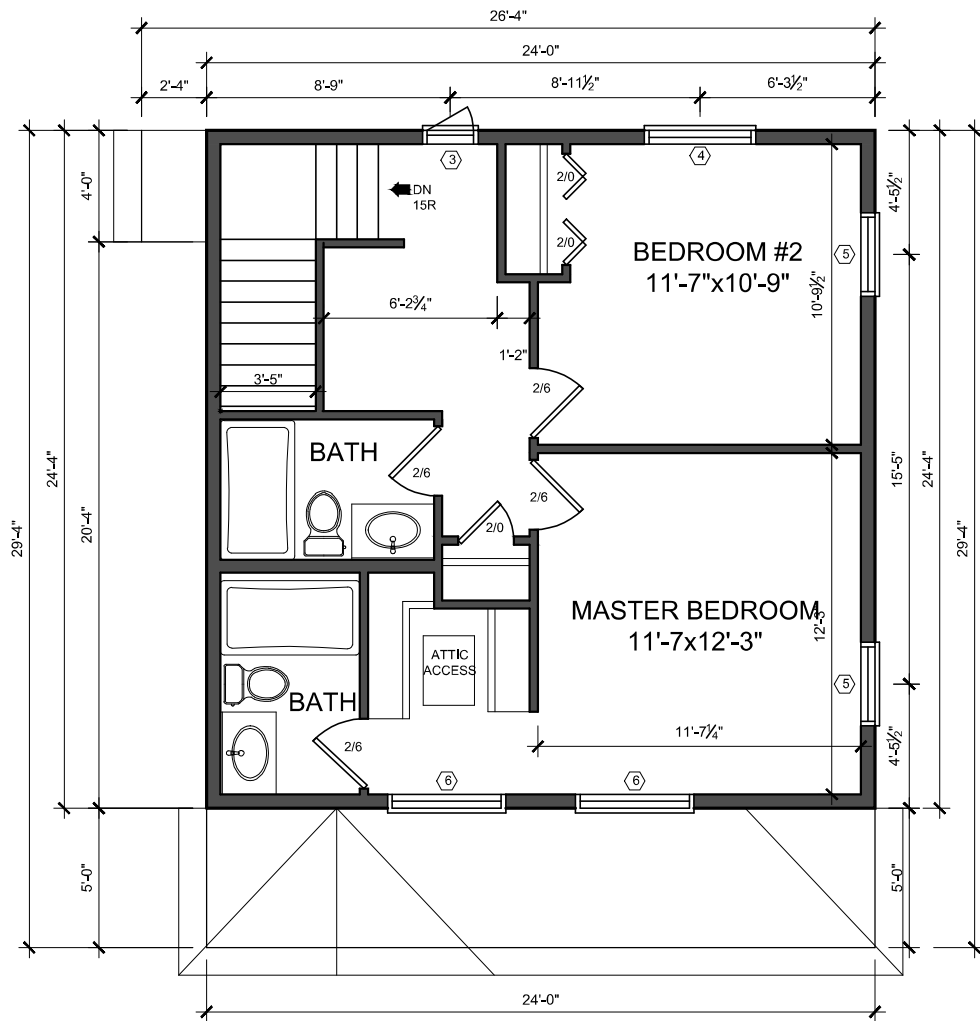

UPPER FLOOR PLAN
 SCALE: 3/16"=1'-0"

This drawing set is intended to act as an example of drawing standards and may not be reproduced without permission. Any similarities with actual buildings and or locations is coincidental. Refer to the requirements list for complete drawing requirements.

Revisions:	


Issued For:	

Consultants/Seals:	

MUNICIPAL ADDRESS:
 3615 4 ST SW
 LEGAL ADDRESS:
 4647GU; A; 7,8

Drawing Name:
 UPPER FLOOR PLAN

Drawn:	Checked:
Date:	
Drawing Scale:	3/16"=1'-0"
Consultant Project Number:	
Project Number:	Sheet:
	10 OF 23
Consultant File Number:	
File Number:	

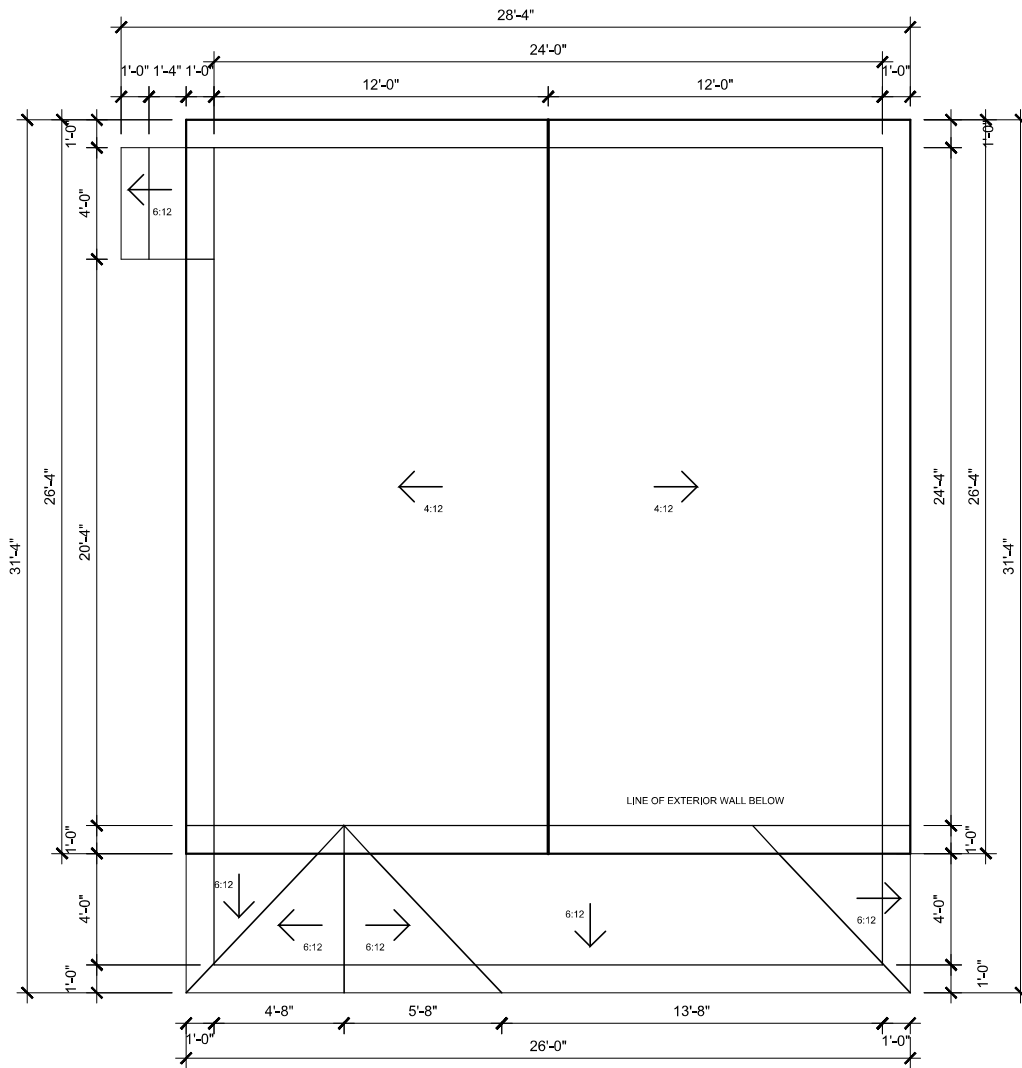

ROOF PLAN
SCALE: 3/16"=1'-0"

This drawing set is intended to act as an example of drawing standards and may not be reproduced without permission. Any similarities with actual buildings and or locations is coincidental. Refer to the requirements list for complete drawing requirements.

Revisions:	


Issued For:	

Consultants/Seals:	

MUNICIPAL ADDRESS:
3615 4 ST SW
LEGAL ADDRESS:
4647GU; A; 7,8

Drawing Name:
ROOF PLAN

Drawn:	Checked:
Date:	
Drawing Scale:	3/16"=1'-0"
Consultant Project Number:	
Project Number:	Sheet:
	11 OF 23
Consultant File Number:	
File Number:	

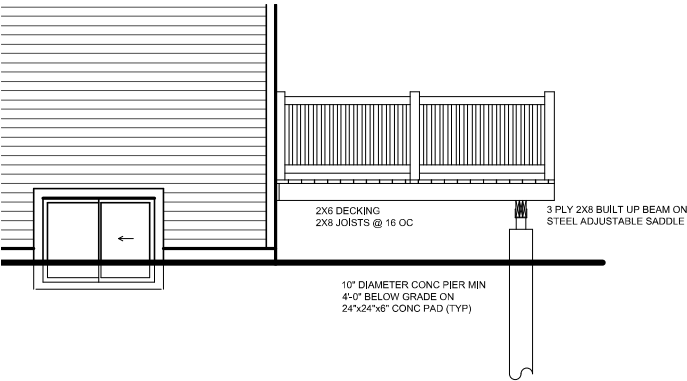

DECK SECTION
SCALE: 3/16"=1'-0"

This drawing set is intended to act as an example of drawing standards and may not be reproduced without permission. Any similarities with actual buildings and or locations is coincidental. Refer to the requirements list for complete drawing requirements.

Revisions:		


Issued For:		

Consultants/Seals:		


MUNICIPAL ADDRESS:
3615 4 ST SW
LEGAL ADDRESS:
4647GU; A; 7,8

Drawing Name:
DECK PLAN AND SECTION

Drawn:		Checked:	
Date:			
Drawing Scale:		3/16"1'-0"	
Consultant Project Number:			
Project Number:		Sheet:	
		12 OF 23	
Consultant File Number:			
File Number:			

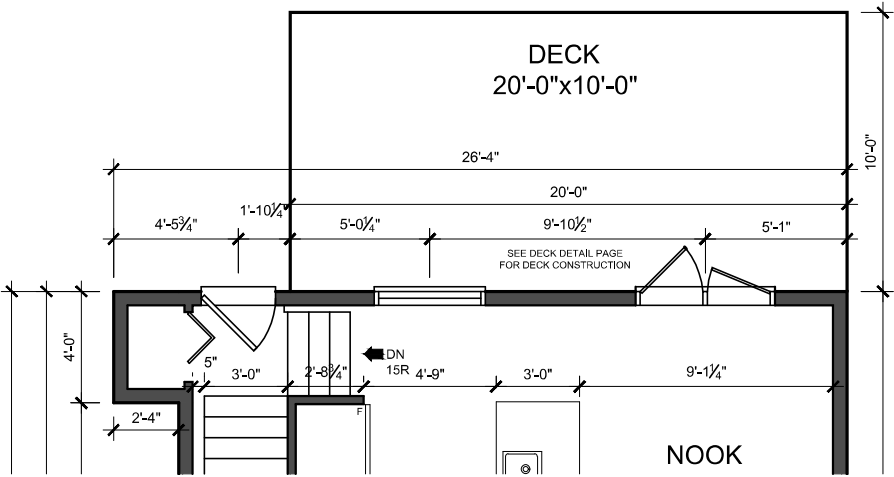

ELECTRICAL LEGEND			
	CEILING LIGHT		GFI OUTLET
	WALL MOUNT LIGHT		WEATHER PROTECTED OUTLET
	PULL CHAIN		ELEC. OUTLET
	BATHROOM FAN		SWITCHED OUTLET
	TELEPHONE		SWITCH
	TELEVISION		3-WAY SWITCH
	THERMOSTAT		4-WAY SWITCH
	DOOR CHIME		SMOKE/CO ALARM
	240V OUTLET		240V GFI OUTLET

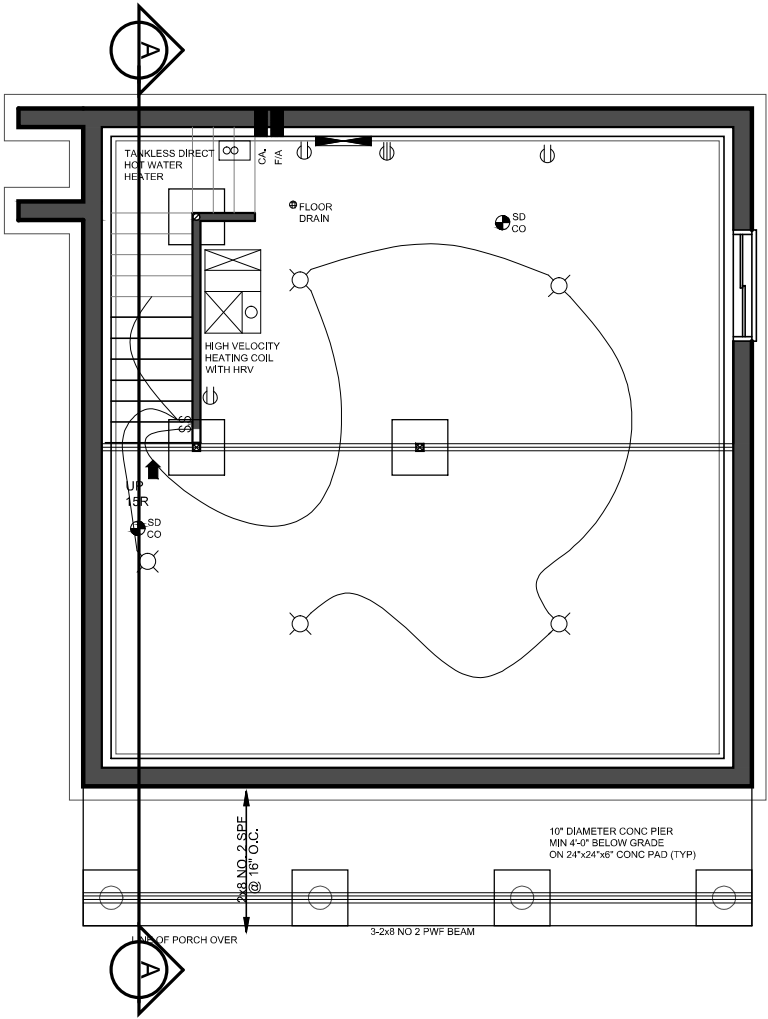

FOUNDATION PLAN
SCALE: 3/16"=1'-0"

This drawing set is intended to act as an example of drawing standards and may not be reproduced without permission. Any similarities with actual buildings and or locations is coincidental. Refer to the requirements list for complete drawing requirements.

Revisions:		


Issued For:		

Consultants/Seals:	

MUNICIPAL ADDRESS:
3615 4 ST SW
LEGAL ADDRESS:
4647GU; A; 7,8

Drawing Name:
FOUNDATION PLAN
ELECTRICAL

Drawn:	Checked:
Date:	
Drawing Scale:	3/16"=1'-0"
Consultant Project Number:	
Project Number:	Sheet:
	13 OF 23
Consultant File Number:	
File Number:	

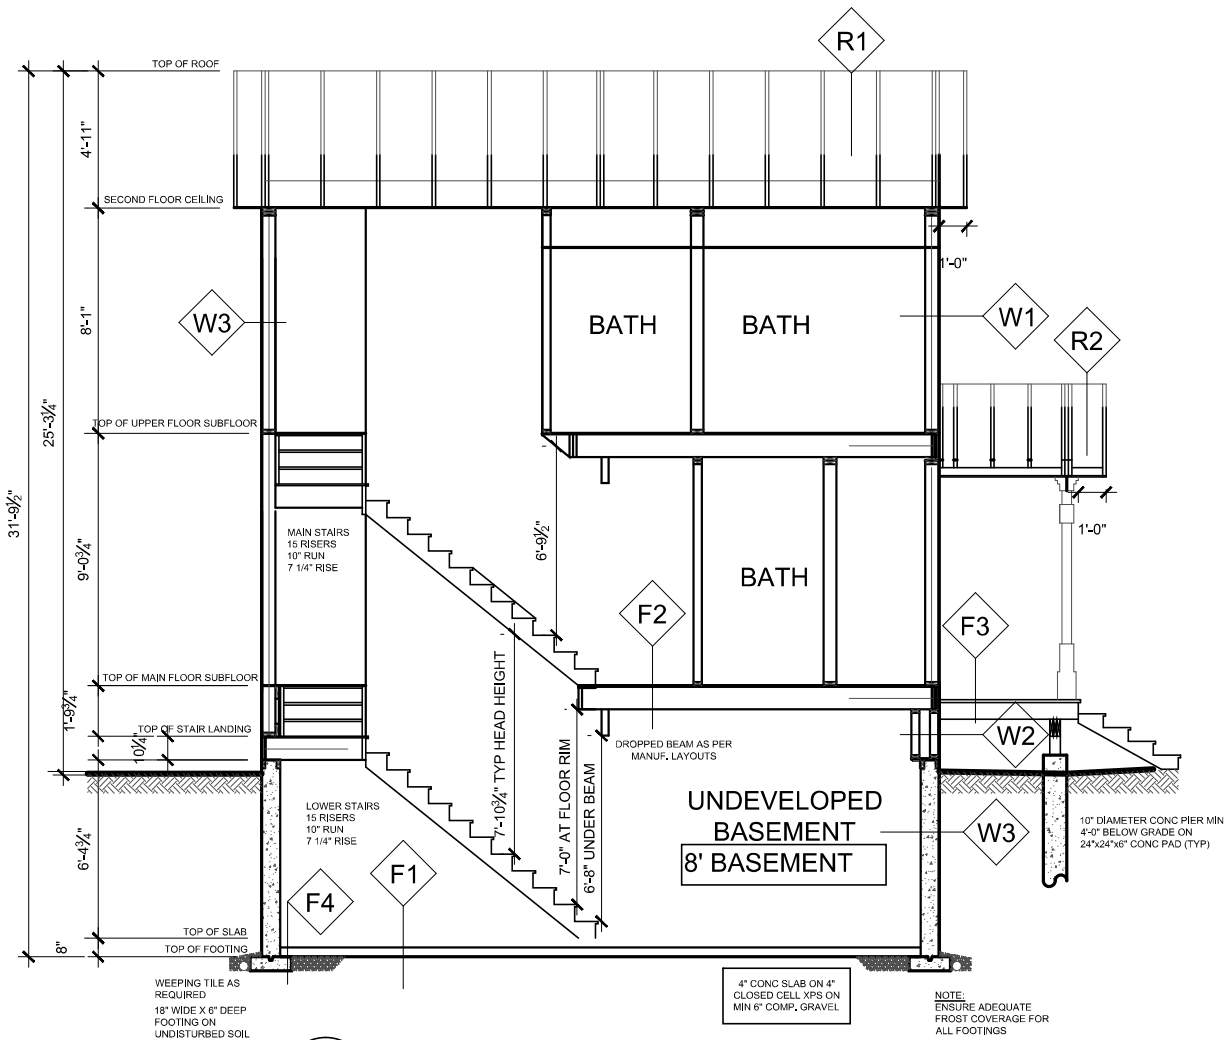

SECTION A-A
SCALE: 3/16"=1'-0"

This drawing set is intended to act as an example of drawing standards and may not be reproduced without permission. Any similarities with actual buildings and or locations is coincidental. Refer to the requirements list for complete drawing requirements.

Revisions:		

Issued For:		

Consultants/Seals:	

MUNICIPAL ADDRESS:
3615 4 ST SW
LEGAL ADDRESS:
4647GU; A; 7,8

Drawing Name:
SECTION A-A

Drawn: _____ Checked: _____

Date: _____

Drawing Scale: 3/16"=1'-0"

Consultant Project Number: _____

Project Number: _____	Sheet: 16 OF 23
-----------------------	---------------------------

Consultant File Number: _____

File Number: _____

GENERAL NOTES

DRAWINGS ARE INTENDED FOR INFORMATIONAL PURPOSES ONLY AND ARE INTENDED TO PRESENT A TYPICAL DRAWINGS SET SUCH AS REQUIRED BY THE CITY OF CALGARY COMPLETE APPLICATION REQUIREMENT LISTS. THIS SET MAY OR MAY NOT FULFILL ALL ASPECTS AND/OR REQUIREMENTS OF ANY APPLICABLE REQUIREMENT LIST AND SHOULD ONLY BE USED TO DEMONSTRATE A PROFESSIONAL LEVEL OF DRAFTING STANDARDS AS REQUIRED FOR THE SUBMISSION OF AN APPLICATION TO THE CITY OF CALGARY. USE OF THESE DRAWINGS FOR DUPLICATION AND OR SUBMISSION IN WHOLE OR IN PART IS PROHIBITED.

UNLESS OTHERWISE NOTED, ALL DETAILS, SECTIONS AND NOTES SHOWN ON THE CONTRACT DRAWINGS ARE INTENDED TO BE TYPICAL AND SHALL APPLY TO SIMILAR CONDITIONS ELSEWHERE.

ALL OMISSIONS OR CONFLICTS BETWEEN THE VARIOUS ELEMENTS OF THE CONTRACT DRAWINGS AND OR SPECIFICATIONS SHALL BE BROUGHT TO THE ATTENTION OF THE ENGINEER AND OR DESIGNER BEFORE PROCEEDING WITH ANY WORK INVOLVED.

THE CONTRACTOR SHALL VERIFY ALL JOB SITE CONDITIONS AND RELATED DIMENSIONS.

ALL CONSTRUCTION SHALL BE IN ACCORDANCE TO THE LATEST EDITION OF THE ALBERTA BUILDING CODE.

THE CONTRACTOR SHALL BE RESPONSIBLE FOR THE PROTECTION OF AND THE SAFETY IN AND AROUND THE JOB SITE AND OF ADJACENT PROPERTIES.

CONTRACTOR AND OR OWNER SHALL KEEP LOADS ON THE STRUCTURE WITHIN THE LIMITS OF THE DESIGN BOTH DURING AND AFTER CONSTRUCTION.

COMPLIANCE WITH APPLICABLE CODES, ORDINANCES AND BYLAWS GOVERNMING THE WORK SHALL BE MADE AND ENFORCED BY THE GENERAL CONTRACTOR.

GENERAL CONTRACTOR SHALL VERIFY ALL EXISTING CONDITIONS AND DIMENSIONS PRIOR TO CONSTRUCTION.

NOTE THAT ALL WRITTEN DIMENSIONS TAKE PRECEDENCE OVER SCALE.

MANUFACTURER'S SPECIFICATIONS FOR INSTALLATION OF MATERIALS SHALL BE FOLLOWED.

WORKMANSHIP THROUGHOUT SHALL BE OF THE BEST QUALITY OF THE TRADE INVOLVED AND THE GENERAL CONTRACTOR SHALL COORDINATE THE WORK OF THE VARIOUS TRADES TO EXPEDITE THE JOB IN A SMOOTH AND CONTINUOUS PROCESS.

CONSTRUCTION ASSEMBLY NOTES

WALL TYPES

- W1

TYPICAL EXTERIOR WALL ASSEMBLY
VINYL SIDING
TYVEK HOUSE WRAP
½" OSB EXTERIOR SHEATHING
2X6 STUDS @ 16" O.C.
R-25 BATT INSULATION
6 MIL POLY VAPOUR BARRIER
½" GYPSUM DRYWALL
- W2

DOUBLE WALL ASSEMBLY AT PONY WALL
VINYL SIDING
TYVEK HOUSE WRAP
½" OSB EXTERIOR SHEATHING
2X4 STUD WALL @ 16 O.C.
5" CAVITY
LOOSE FILL BLOWN INSULATION R-50 MIN
2X4 STUD WALL @ 16 O.C.
6 MIL POLY VAPOUR BARRIER
- W3

FOUNDATION WALL ASSEMBLY
DRAINAGE BOARD
DAMP-PROOFING
8" CONCRETE FOUNDATION WALL
4" CLOSED CELL XPS INSULATION

FLOOR TYPES

- F1

FOUNDATION SLAB
4" CONCRETE SLAB
6 MIL POLY AIR BARRIER
MIN 6" COMPACTED GRAVEL BASE
- F2

TYPICAL FLOOR ASSEMBLY
¾" PLYWOOD SUBFLOOR
9 ½" TJI ENGINEERED JOISTS @ 16 O.C.
½" GYPSUM DRYWALL
- F3

PORCH DECK ASSEMBLY
¾" DECKING
2X8 JOISTS @ 16 O.C.
- F4

FOOTING ASSEMBLY
20" x 6" CONC. STRIP FOOTINGS

ROOF ASSEMBLY TYPES

- R1

MAIN ROOF ASSEMBLY
ASPHALT SHINGLES
ICE AND WEATHER SHIELD
½" PLYWOOD C/W H CLIPS AT JOINS
ENGINEERED TRUSSES @ 24 O.C. PER LAYOUTS
BLOWN IN LOOSE FILL INSULATION TO MEET R-50
BATT INSULATION R-21 BETWEEN TRUSSES
6 MIL POLY VAPOUR BARRIER
½" GYPSUM DRYWALL
- R2

PORCH ROOF ASSEMBLY
ASPHALT SHINGLES
ICE AND WEATHER SHIELD
½" PLYWOOD C/W H CLIPS AT JOINS
ENGINEERED TRUSSES @ 24 O.C. PER LAYOUT
PAINTED EXTERIOR GRADE MDF SHEATHING
VENTING PER ABC

This drawing set is intended to act as an example of drawing standards and may not be reproduced without permission. Any similarities with actual buildings and or locations is coincidental. Refer to the requirements list for complete drawing requirements.

Revisions:

Issued For:

Consultants/Seals:

MUNICIPAL ADDRESS:
3615 4 ST SW
LEGAL ADDRESS:
4647GU; A; 7,8


Drawing Name:
GENERAL NOTES & CONSTRUCTION ASSEMBLIES

Drawn:	Checked:
Date:	
Drawing Scale:	NTS
Consultant Project Number:	
Project Number:	Sheet: 17 OF 23
Consultant File Number:	
File Number:	

NORTH AMERICAN FENESTRATION STANDARDS

TERRAIN - OPEN
PERFORMANCE CLASS -R
PERFORMANCE GRADE - PG30
POSITIVE DESIGN PRESSURE 1440 Pa
NEGATIVE DESIGN PRESSURE - 1440 Pa
WATER PENETRATION RESISTANCE TEST
PRESSURE - 330 Pa
CANADIAN AIR INFILTRATION/EXFILTRATION - A2
LEVEL
U-VALUE - MAXIMUM OF 1.6 FOR DOORS AND
WINDOWS, MAXIMUM OF 2.7 FOR SKYLIGHTS PER
9.7.3.3

WINDOW SCHEDULE				
NO.	TYPE (H X W)	NOTES	LEVEL	COUNT
①	48" X 36 1/2" SL	XO, 185 SERIES OR EQUIV.	FDN	1
②	83 1/2" X 59 7/8" TRI-WINDOW	LPR CASEMENT, 260 SERIES OR EQUIV.	MAIN	1
③	24 3/8" X 59 7/8" CASEMENT	R, 260 SERIES OR EQUIV.	MAIN & 2	2
④	48" X 48" DUAL CASEMENT	LR, 260 SERIES OR EQUIV.	MAIN & 2	2
⑤	36" X 36" CASEMENT	R, 260 SERIES OR EQUIV.	2ND	2
⑥	51" X 48" SINGLE HUNG	XO, 260 SERIES OR EQUIV.	2ND	2

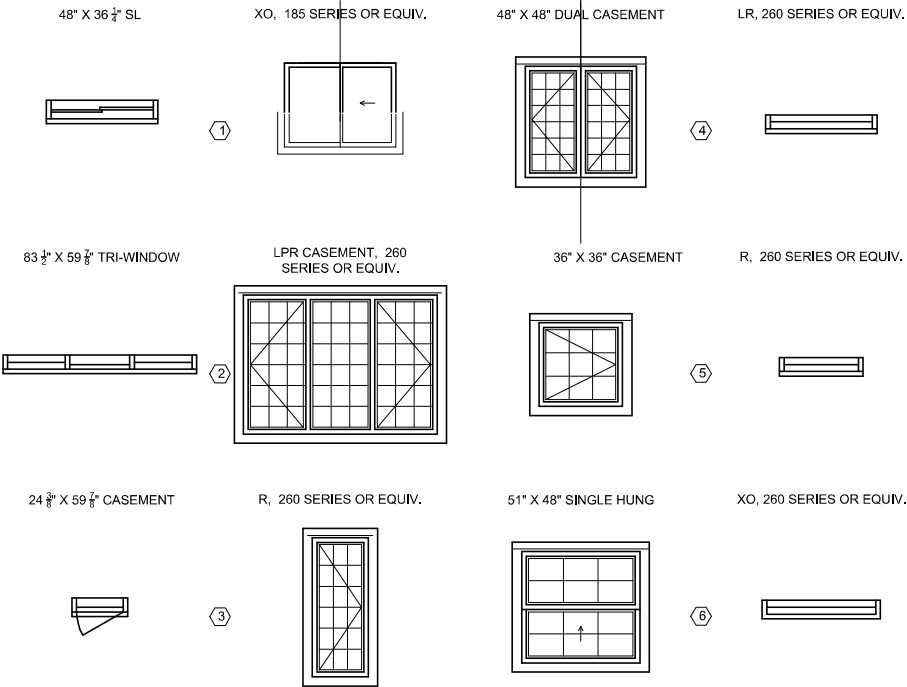

This drawing set is intended to act as an example of drawing standards and may not be reproduced without permission. Any similarities with actual buildings and or locations is coincidental. Refer to the requirements list for complete drawing requirements.

Revisions:

Issued For:

Consultants/Seals:

MUNICIPAL ADDRESS:
3615 4 ST SW
LEGAL ADDRESS:
4647GU; A; 7,8

Drawing Name:
WINDOW SCHEDULE

Drawn: Checked:

Date:

Drawing Scale: NTS

Consultant Project Number:

Project Number: Sheet:


18 OF 23

Consultant File Number:

File Number:

WINDOW INSTALLATION

WEATHER RESISTIVE BARRIER (WRB) APPLIED PRIOR TO THE WINDOW INSTALLATION.
FLASHING APPLIED BEHIND THE MOUNTING FLANGE.

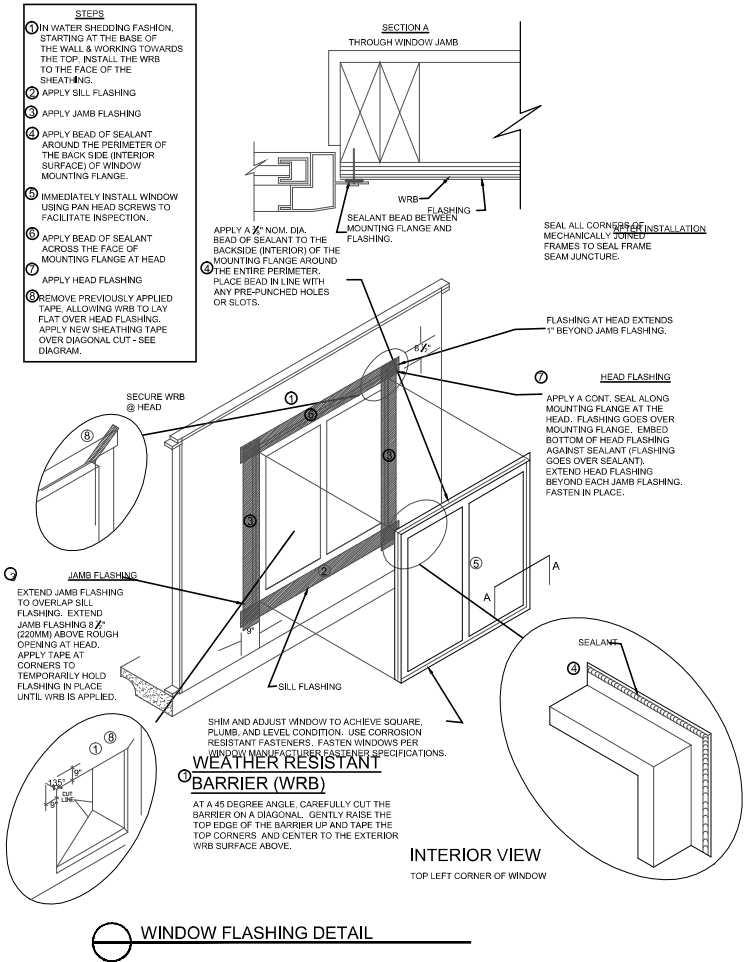

This drawing set is intended to act as an example of drawing standards and may not be reproduced without permission. Any similarities with actual buildings and or locations is coincidental. Refer to the requirements list for complete drawing requirements.

Revisions:	


Issued For:	

Consultants/Seals:	

MUNICIPAL ADDRESS:
3615 4 ST SW
LEGAL ADDRESS:
4647GU; A; 7,8

Drawing Name:
**WINDOW FLASHING
DETAIL**


Drawn:	Checked:
Date:	
Drawing Scale:	NTS
Consultant Project Number:	
Project Number:	Sheet:
	19 OF 23
Consultant File Number:	
File Number:	

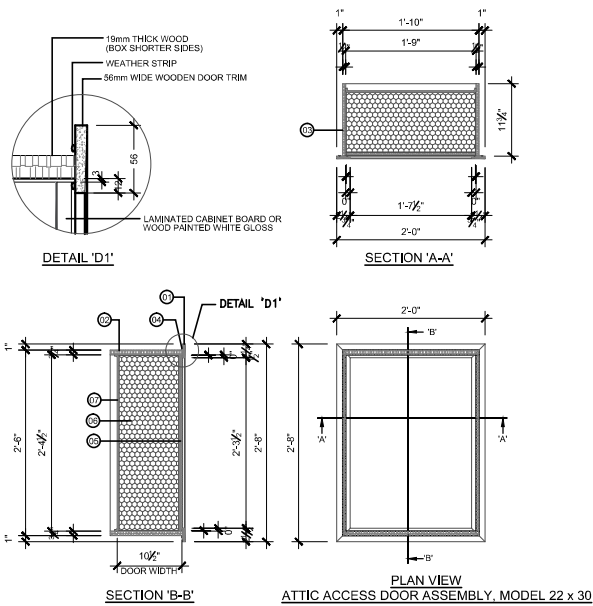


ITEM	DESCRIPTION	DRAWING NO.
01	56mm WIDE WOODEN DOOR TRIM ASSEMBLY	AAD-M 22-30-002
02	19mm THICK WOOD (BOX SHORTER SIDES)	AAD-M 22-30-002
03	12mm THICK WOOD (BOX LONGER SIDES)	AAD-M 22-30-002
04	WEATHER STRIP	AAD-M 22-30-002
05	LAMINATED CABINET BOARD OR WOOD PAINTED WHITE GLOSS	AAD-M 22-30-003
06	250mm THICK EXPANDED POLYSTYRENE	AAD-M 22-30-003
07	SEALING GASKET- 6mm THK RUBBER PIPE/DUCT INSULATION	AAD-M 22-30-003

ATTIC ACCESS DOOR, MODEL 22 x 30
GENERAL ARRANGEMENT

ATTIC HATCH DETAIL

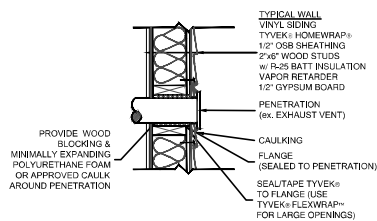

WALL PENETRATION DETAIL

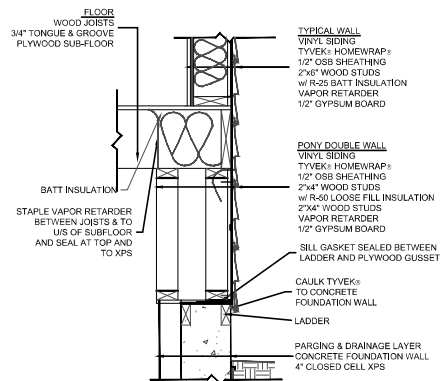

BASE OF WALL AT PONY WALL DETAIL

This drawing set is intended to act as an example of drawing standards and may not be reproduced without permission. Any similarities with actual buildings and or locations is coincidental. Refer to the requirements list for complete drawing requirements.

Revisions:

Issued For:

Consultants/Seals:

MUNICIPAL ADDRESS:
3615 4 ST SW
LEGAL ADDRESS:
4647GU; A; 7,8

Drawing Name:
9.36 DETAILS

Drawn:	Checked:
Date:	
Drawing Scale:	NTS
Consultant Project Number:	
Project Number:	Sheet: 21 OF 23
Consultant File Number:	
File Number:	



This drawing set is intended to act as an example of drawing standards and may not be reproduced without permission. Any similarities with actual buildings and or locations is coincidental. Refer to the requirements list for complete drawing requirements.

Revisions:

Issued For:

Consultants/Seals:

MUNICIPAL ADDRESS:
3615 4 ST SW
LEGAL ADDRESS:
4647GU; A; 7,8

Drawing Name:
DETAILS

Drawn:	Checked:
--------	----------

Date:

Drawing Scale: NTS

Consultant Project Number:

Project Number:

Sheet:

22 OF 23

Consultant File Number:

File Number: