

1 MOUNTING HEIGHTS
C-301 SCALE: 1/2" = 1'0"

- NOTE:
- HEIGHT AS PER 2017 ICC A117.1 WITH SUPPLEMENT 1 ACCESSIBLE AND USABLE BUILDINGS AND FACILITIES, SECTION 602


FITTINGS AND ACCESSORIES SCHEDULE			
S.N.	TAG	ACCESSORY	ITEM SPECIFICATION
1.	AC-1	TOILET PAPER DISPENSER	BOBRICK MODEL: B2888 OR EQUAL
2.	AC-2	TOILET SEAT COVER DISPENSER	KIMBERLY-CLARK MODEL: 09505 OR EQUAL
3.	AC-3	DIAPER CHANGING STATION	ASI MODEL: 10-9012 OR EQUAL
4.	AC-4	SOAP DISPENSER	SAON MODEL: 4034 OR EQUAL
5.	AC-5	HAND DRYER	ASI MODEL: 10-0192-1-93 OR EQUAL
6.	AC-6	PAPER TOWEL DISPENSER W/ TRASH CAN	HARDWARE RESOURCES MODEL: CAN-35GRY OR EQUAL
7.	AC-7	SANITARY NAPKIN DISPENSER	SEACHROME MODEL: SCAL-170 OR EQUAL
8.	AC-8	PAPER TOWEL DISPENSER	ASI MODEL: 10-0210-41 OR EQUAL
9.	AC-9	COMMERCIAL WALL RACK	ROHL MODEL: ROT10APC OR EQUAL
10.	G-1	GRAB BAR VERTICAL	SYSTEM MODEL: 3570.001.10 OR EQUAL
11.	G-2	GRAB BAR HORIZONTAL	POLO MODEL: 0770.001.30 OR EQUAL
12.	G-3	TOWEL BAR	NORM MODEL: WSBC 268610-12 CR OR EQUAL
13.	L-1	LAVATORY TYPE-1	SIMPLE 60.50A MODEL: 60.50A.01 OR EQUAL
14.	L-2	LAVATORY TYPE -2	SLOAN MODEL: ELRF-83000 OR EQUAL
15.	HS-1	HAND SINK -1	SERV-WARE MODEL:HS15-CWP OR EQUAL
16.	M-1	MIRROR TYPE-1	SPECI MODEL:SPECI 5676 OR EQUAL
17.	M-2	MIRROR TYPE-2	Elan Model: 84171 OR EQUAL
18.	M-3	MIRROR TYPE-3	MODO BATH MODEL: T5 T5-R OR EQUAL
19.	MS-1	MOP SINK	PROFLO MODEL: PFMB2424 OR EQUAL
20.	P-1	SS PARTITION WALL UPTO 8'	GLOBAL PARTITIONS MODEL: PCSBW OR EQUAL
21.	P-2	SS PARTITION WALL UPTO 4'-4"	GLOBAL PARTITIONS MODEL: 9SFCSEX OR EQUAL
22.	P-3	SS PARTITION WALL UPTO 8'	GLOBAL PARTITIONS MODEL: PCSBW OR EQUAL
23.	S-1	SHOWER HEAD	KOHLER MODEL: K-22170-CP OR EQUAL
24.	U-1	URINAL,STD	TOTO MODEL: UT104E#01 OR EQUAL
25.	U-2	URINAL,ACC	TOTO MODEL: UT104E#01 OR EQUAL
26.	U-3	UTILITY HOOKS	IVES MODEL: 581A92 OR EQUAL
27.	WC-1	WATER CLOSET,STD	SLOAN MODEL: 20231001 OR EQUAL
28.	WC-2	WATER CLOSET,ACC	SLOAN MODEL: 20231001 OR EQUAL
29.	WH-1	WATER HEATER	CYCLONER MXI MODULATING MODEL: BTH-120 MXI OR EQUAL
30.	WF-1	WATER FOUNTAIN	ELKAY MODEL: EZSTL8LC OR EQUAL

MATERIAL AND FINISHES SCHEDULE		LOBBY				SHOWER ROOM				FAMILY RESTROOM				MEN'S RESTROOM				WOMEN'S RESTROOM				UTILITY ROOM				SEATING AREA					
		FLOOR	CEILING	WALL-NORTH	WALL-SOUTH	WALL-EAST	WALL-WEST	FLOOR	CEILING	WALL-NORTH	WALL-SOUTH	WALL-EAST	WALL-WEST	FLOOR	CEILING	WALL-NORTH	WALL-SOUTH	WALL-EAST	WALL-WEST	FLOOR	CEILING	WALL-NORTH	WALL-SOUTH	WALL-EAST	WALL-WEST	FLOOR	CEILING	WALL-NORTH	WALL-SOUTH	WALL-EAST	WALL-WEST
CEILING	EXTERIOR PVC PLANK		X																												
	MOISTURE RESISTANT TILE																														
FLOOR	CERAMIC TILE (ANTI SLIP)																														
	SEALED CONCRETE	X																													
WALL	CERAMIC TILE																														
	PAINT																														
	EXTERIOR BOARD			X	X	X	X																								
	BRICK CLADDING																														X

MATERIALS AND FINISHES LEGEND			
TAG	PRODUCT DESCRIPTION	BRAND / MANUFACTURER	TYPE / COLOR
1	SEALED CONCRETE FLOORING	NA	LIGHT GREY OR APPROVED EQUAL
2	CERAMIC FLOOR TILE (ANTI-SLIP)	TRAFFICMASTER	BAJA GRAY - MATTE FINISH 12" X 12" OR APPROVED EQUAL
4	MOISTURE RESISTANT CEILING TILE	ARMSTRONG	FINE FISSURED - IVORY 24" X 48" OR APPROVED EQUAL
5	FIBER CEMENT BOARD	ALLURA	WHITE 12' X 16" OR APPROVED EQUAL
6	METAL ROOF PANEL	NA	STANDING SEAM - GALVALUME COATED - REGAL BLUE OR APPROVED EQUAL
7	METAL BOX GUTTER WITH DOWNSPOUT	NA	GALVALUME COATED - BLACK POWDER COATED FINISH OR APPROVED EQUAL
8	METAL FASCIA TRIM BOARD	NA	REGAL BLUE OR APPROVED EQUAL
9	EXTERIOR FIBER CEMENT PANEL SIDING	JAMES HARDIE	CEDARMILL TEXTURE - PTD TO SILVER HERRING OR APPROVED EQUAL
10	EXTERIOR FIBER GLASS COLUMN WRAP	RESINART	DURACRAFT - WHITE OR APPROVED EQUAL
11	BRICK MASONRY ANCHORED CLADDING	BRICKWORKS GLEN-GERY	MOUNTAIN SHADOW SMOOTH OR APPROVED EQUAL
12	EXTERIOR FIBER CEMENT TRIM	JAMES HARDIE	SMOOTH TEXTURE - PRIMED FINISH - PTD TO SW - EXTRA WHITE OR APPROVED EQUAL
13	METAL SOFFIT (PERFORATED)	NA	REGAL BLUE OR APPROVED EQUAL
14	EXTERIOR FIBER CEMENT ARTISAN SIDING	JAMES HARDIE	V-GROOVE - PRIMED FINISH - PTD TO SW - OLYMPUS WHITE OR APPROVED EQUAL
15	INTERIOR LATEX WALL PAINT	SHERWIN WILLIAMS	SW-1668 (PINEAPPLE CREAM) OR APPROVED EQUAL
16	CERAMIC WALL TILE	DALTILE	GLACIER WHITE - GLOSSY FINISH 6" X 6" OR APPROVED EQUAL
17	RUBBER COVE BASE	ROPPE	PINNACLE DARK GRAY MATTE - 6" OR APPROVED EQUAL

MATERIALS AND FINISHES NOTES:

- A. ROOF COVERING MATERIAL TO BE A, B OR C CLASSIFICATION PER NCBC SECTION 603.1.
- B. THERMAL AND ACOUSTIC INSULATION TO HAVE A FLAME SPREAD INDEX NOT MORE THAN 25, PER NCBC SECTION 603.1.
- C. INTERIOR FINISHES COMPLIANCE AS PER NCBC CHAPTER 8:
1. ALL INTERIOR WALLS AND CEILING FINISHES SHALL BE CLASS-C WITH FLAME SPREAD INDEX RANGE 76-200 AND SMOKE DEVELOPED INDEX RANGE 0-450. (SECTION 803.1.1.)
2. ALL INTERIOR FLOOR FINISHES AND WALL-BASE FINISHES SHALL BE CLASS-II, 0.22 WATTS/SQ.CM. MINIMUM CRITICAL RADIANT FLUX. (SECTION 804.2, 806.8)

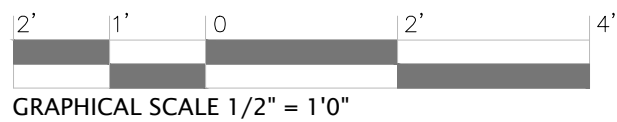

RESTROOMS

CAROLINA MURUGAN TEMPLE - PHASE 1

CLIENT: CAROLINA MURUGAN TEMPLE
100 MURUGAN CIR, MONCURE, NC 27559

DATE: 6/13/2025
SSN JOB ID: 1021-02-2024
DESIGNED BY: MK
DRAWN BY: BM
CHECKED BY: MK
REVIEWED BY: MN



#	REVISIONS	DATE
1	REV-1	6/11/2025

FINISHES, FITTINGS AND ACCESSORIES SCHEDULE


C - 301

DOOR AND WINDOW SCHEDULE


DOOR NO.	NO. OF DOORS	DOOR			PANEL		FRAME			HARDWARE
		W.	H.	T.	MAT'L	TYPE	MAT'L	TYPE	FINISH	
D1	4	3'-0"	7'-0"	0'-1 $\frac{3}{4}$ "	STL	P1	HM	DF1	PTD - PTM1	SATIN CHROME FINISH
D2	1	3'-6"	8'-0"	0'-1 $\frac{3}{4}$ "	STL	P2	HM	DF2	PTD - PTM1	SATIN CHROME FINISH
WINDOW NO.	NO. OF WINDOWS	WINDOW				FRAME			HARDWARE	
		W.	H.	T.	MAT'L	TYPE	MAT'L	TYPE	FINISH	(FIXED GLASS WINDOW HARDWARE PER MANUFACTURER'S REQUIREMENTS)
W1	2	2'-6"	3'-0"	0'-2"	GLASS	W1	ALUM	W1	POWDER COATED	
W2	4	4'-0"	3'-0"	0'-2"	GLASS	W2	ALUM	W2	POWDER COATED	

NOTES


- A. REFER TO FLOOR PLANS FOR LOCATION OF DOORS AND WINDOWS.
- B. ALL WINDOWS AND DOORS SHALL BE SECURELY SHIMMED INTO ROUGH OPENINGS AND SHALL BE TRUE TO LINE, LEVEL, AND PLUMB.
- C. WINDOW HEIGHT SHALL BE SET AT THE SAME HEIGHT THROUGHOUT, FOR PROPER TRIM ALIGNMENT, UNO.
- D. ALL WINDOW FRAMES TO BE POWDER COAT FINISHED TO BLACK OR APPROVED EQUAL.
- E. ALL DOOR FRAMES TO BE PAINTED BLACK (PTM1) OR APPROVED EQUAL.
- F. JAMB WIDTH VARIES. COORDINATE WITH WALL WIDTH AS SHOWN ON FLOOR PLAN.

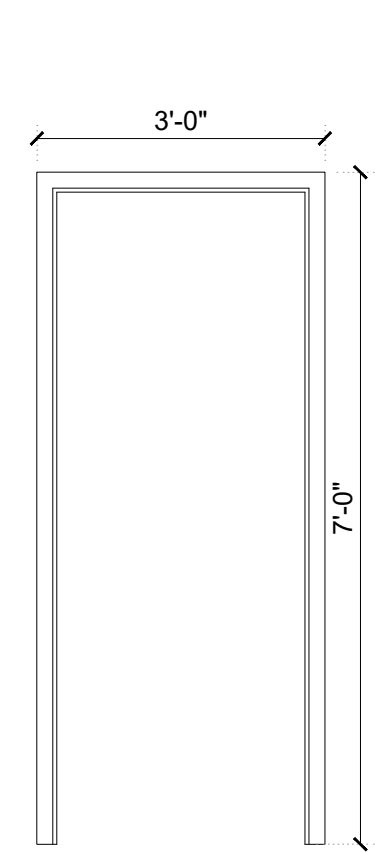


DOOR FRAME TYPE: DF1

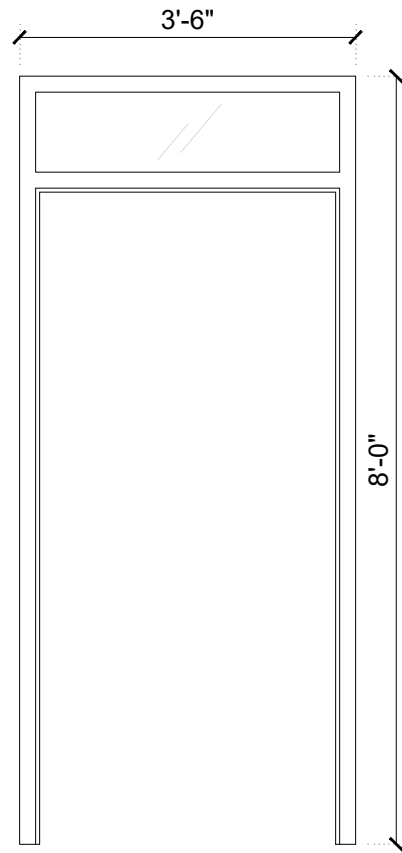


DOOR FRAME TYPE: DF2

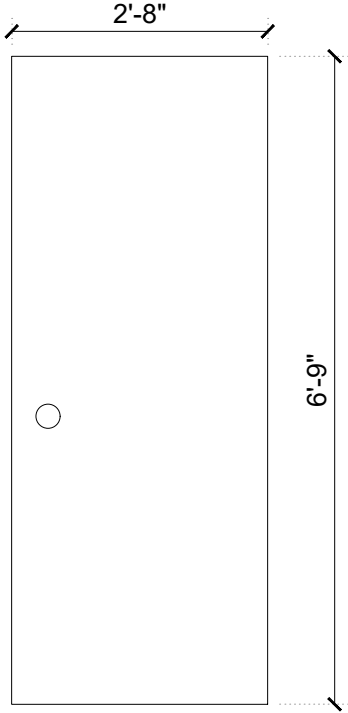


PANEL TYPE: P1

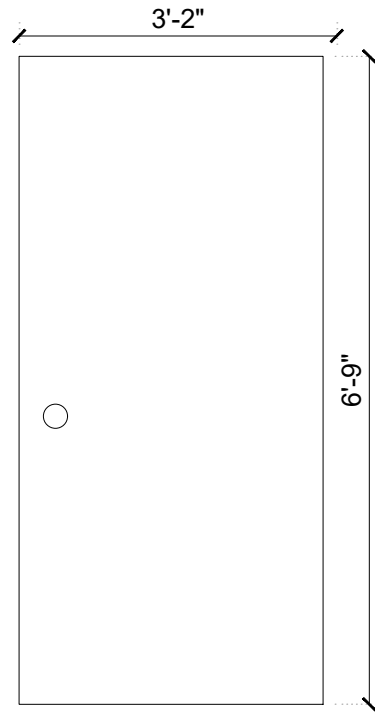


PANEL TYPE: P2

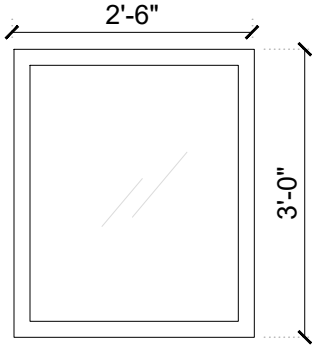

FIXED WINDOW TYPE: W1

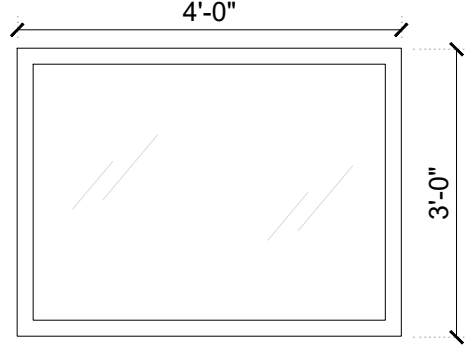

FIXED WINDOW TYPE: W2

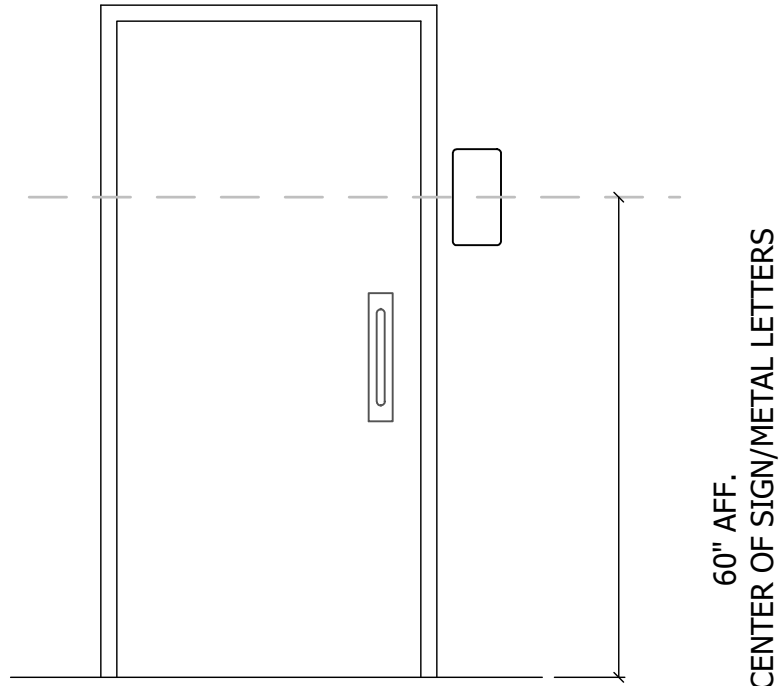

ROOM SIGNS

DOOR FRAME TYPES
SCALE: 1/2"=1'-0"

DOOR PANEL TYPES
SCALE: 1/2"=1'-0"


WINDOW FRAME TYPES
SCALE: 1/2"=1'-0"

PARTITION SCHEDULE


PARTITION WALL TYPE	DESCRIPTION
A1	3 5/8" METAL STUD WITH ONE LAYER OF 5/8" CEMENTITIOUS BACKER BOARD AND CERAMIC TILE UPTO 72" FROM FFL (UNO ON INTERIOR ELEVATIONS) AND PAINTED FINISH ABOVE, ON BOTH SIDE.
A2	3 5/8" METAL STUD WITH ONE LAYER OF 5/8" GYPSUM WALLBOARD WITH PAINTED FINISH ON ONE SIDE AND 5/8" CEMENTITIOUS BACKER BOARD WITH CERAMIC TILE UPTO 72" FROM FFL (UNO ON INTERIOR ELEVATIONS) AND PAINTED FINISH ABOVE, ON OTHER SIDE
B1	6" METAL STUD WITH ONE LAYER OF 5/8" CEMENTITIOUS BACKER BOARD AND CERAMIC TILE UPTO 72" FROM FFL (UNO ON INTERIOR ELEVATIONS) AND PAINTED FINISH ABOVE, ON ONE SIDE AND OTHER SIDE WITH EXTERIOR SHEATHING WITH BRICK CLADDING UPTO BOTTOM OF WINDOW OPENING AND REMAINING HEIGHT OF WALL WITH EXTERIOR SIDING PANEL
B2	6" METAL STUD WITH ONE LAYER OF 5/8" GYPSUM WALLBOARD WITH PAINTED FINISH ON ONE SIDE AND OTHER SIDE WITH EXTERIOR SHEATHING WITH BRICK CLADDING UPTO 5' AND REMAINING HEIGHT OF WALL WITH EXTERIOR SIDING PANEL
B3	6" METAL STUD WITH ONE LAYER OF 5/8" CEMENTITIOUS BACKER BOARD AND CERAMIC TILE UPTO 72" FROM FFL (UNO ON INTERIOR ELEVATIONS) AND PAINTED FINISH ABOVE, ON ONE SIDE AND EXTERIOR SHEATHING WITH EXTERIOR SIDING PANEL ON OTHER SIDE

PARTITION NOTES


- A. EXTEND ALL PARTITION WALLS 10" MIN. ABOVE FALSE CEILING.
- B. PROVIDE ABUSE-RESISTIVE GYPSUM BOARD AND PROVIDE ALL GYPSUM DRYWALL PARTITIONS WITH 3 1/2" SOUND ATTENUATION BATTS.
- C. PROVIDE 5/8" THICK GYPSUM BOARD, UNO.
- D. PROVIDE CONTROL JOINTS AT DRYWALL PARTITIONS LONGER THAN 30 FEET FOR STRAIGHT AND CONTINUOUS WALLS, AND AT OPENING LOCATIONS. WHERE NOT SPECIFICALLY INDICATED ON THE DRAWINGS, CONTRACTOR TO SUBMIT PROPOSED CONTROL JOINT LOCATIONS TO ENGINEER FOR APPROVAL.
- E. PROVIDE 1/2" WIDE SOFT JOINT AT ALL INTERSECTION OF INTERIOR PARTITIONS WITH EXTERIOR WALLS.
- F. DO NOT PLACE MECHANICAL AND/OR ELECTRICAL DEVICES BACK TO BACK IN SOUND BARRIER PARTITIONS. ALL DEVICES TO BE PLACED IN SEPARATE STUD SPACES WITH MINIMUM OF 8" SEPARATION.
- G. PROVIDE PERIMETER SOUND SEAL BETWEEN DUCT AND WALL FRAME ON BOTH SIDES OF PARTITION WALLS WHERE DUCT PENETRATES THROUGH SOUND BARRIER PARTITION WALLS.
- H. PROVIDE CEMENTITIOUS BACKER BOARD OR EQUAL AS THE SUBSTRATE TO RECEIVE CERAMIC TILE.
- I. PROVIDE WATER RESISTANT GYPSUM BOARD OR EQUAL AS THE SUBSTRATE WHERE GYPSUM BOARD IS ADJACENT OR EXPOSED TO HUMID CONDITIONS. PROVIDE THE SUBSTRATE TO RECEIVE HIGH PERFORMANCE PAINT FINISHES. ALL RESTROOM AND KITCHEN INTERIOR WALLS ARE CONSIDERED TO BE HUMID SPACES.
- J. FINISH ALL EXPOSED GYPSUM BOARD CONSTRUCTION. ALL EXPOSED GYPSUM BOARD SHALL BE TAPED, FLOATED AND SANDED SMOOTH TO REMOVE ALL INDICATION OF THE JOINT WITH A VISUAL INSPECTION. FINISH WALL IN ACCORDANCE WITH THE ROOM FINISH SCHEDULE.
- K. PROVIDE 20 GAUGE METAL BLOCKING OR MANUFACTURER RECOMMENDED ATTACHMENT FOR WALL MOUNTED HARDWARE AND TOILET ACCESSORIES.
- L. PROVIDE SOUND ATTENUATION BATTS ABOVE CEILING 4'-0" WIDE ON BOTH SIDES OF WALL.

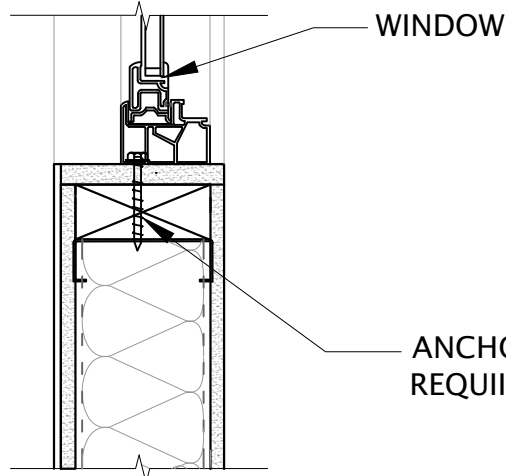


DETAIL- WINDOW (HEAD/JAMB)
SCALE: NA

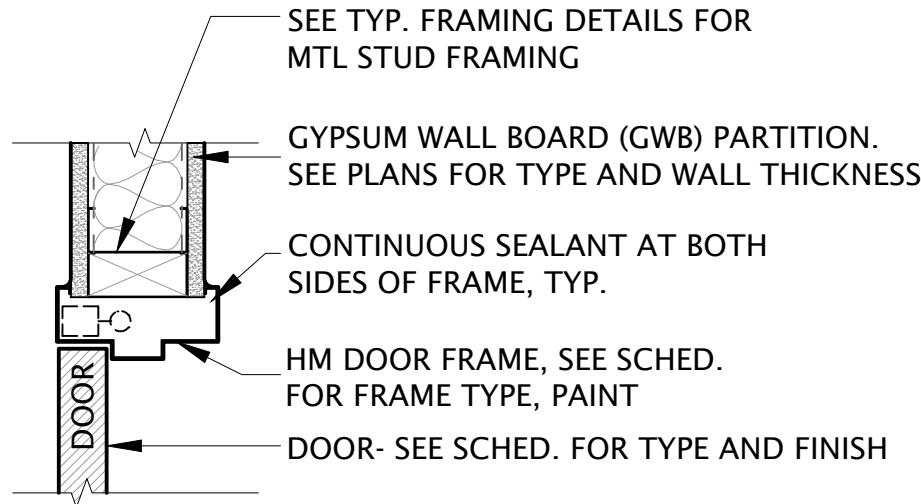


TYP. HM DOOR HEAD
SCALE: NA

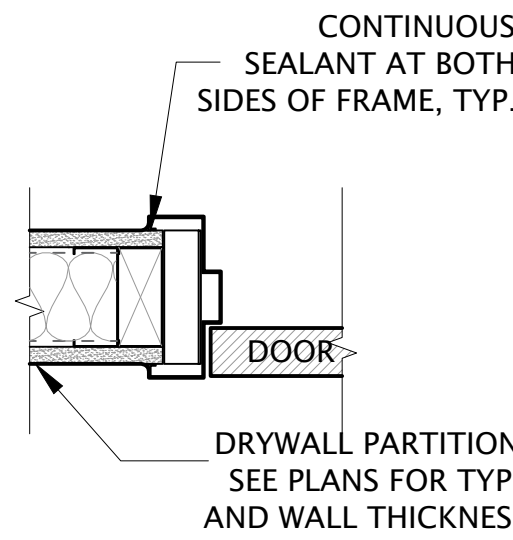


TYP. HM DOOR JAMB
SCALE: NA

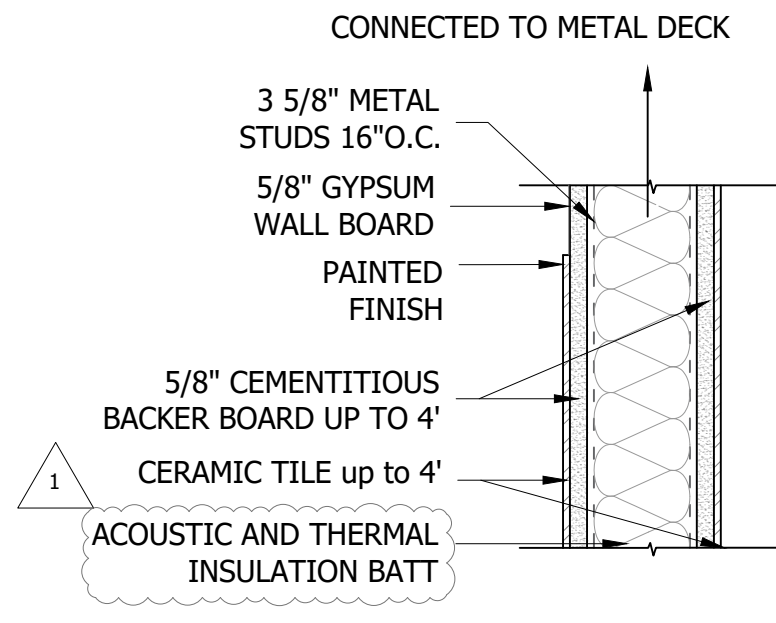


4" PARTITION WALL TYPE A3
SCALE: NTS

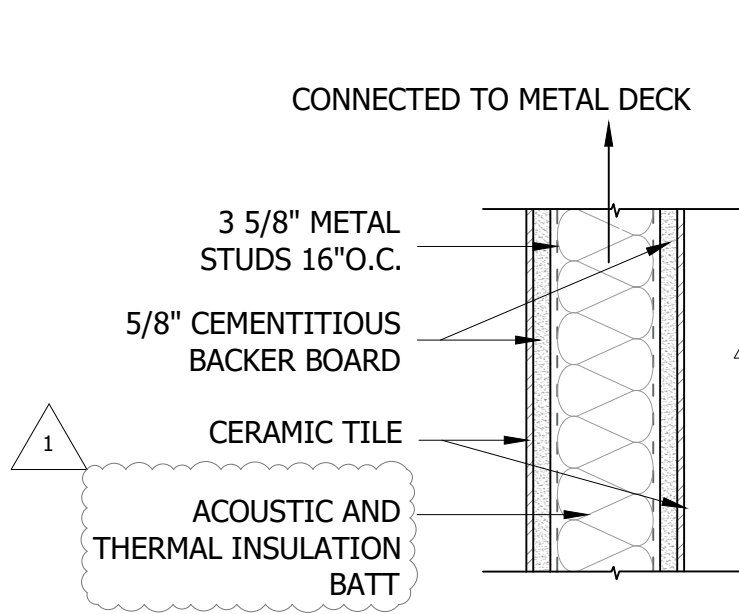


4" PARTITION WALL TYPE A1
SCALE: NTS

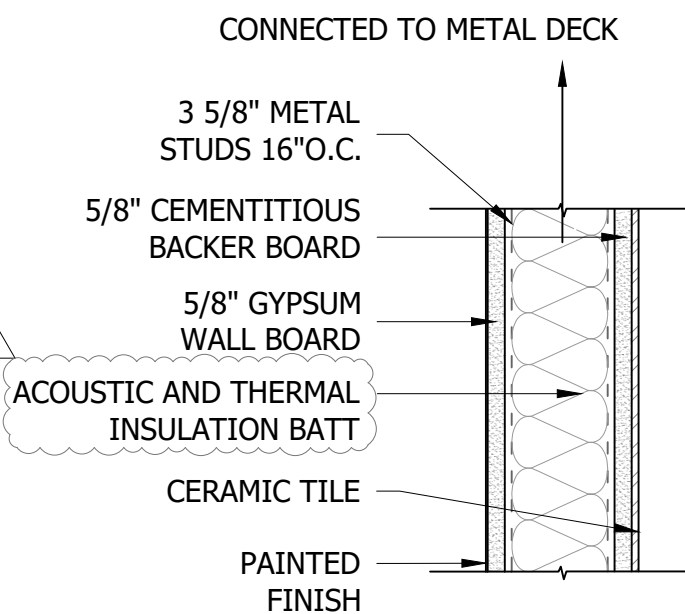


4" PARTITION WALL TYPE A2
SCALE: NTS

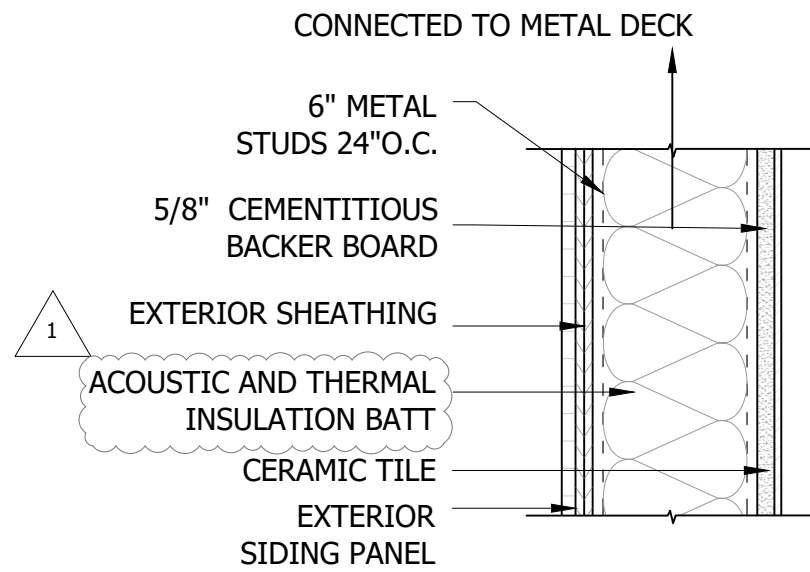

6" PARTITION WALL TYPE B3
SCALE: NTS

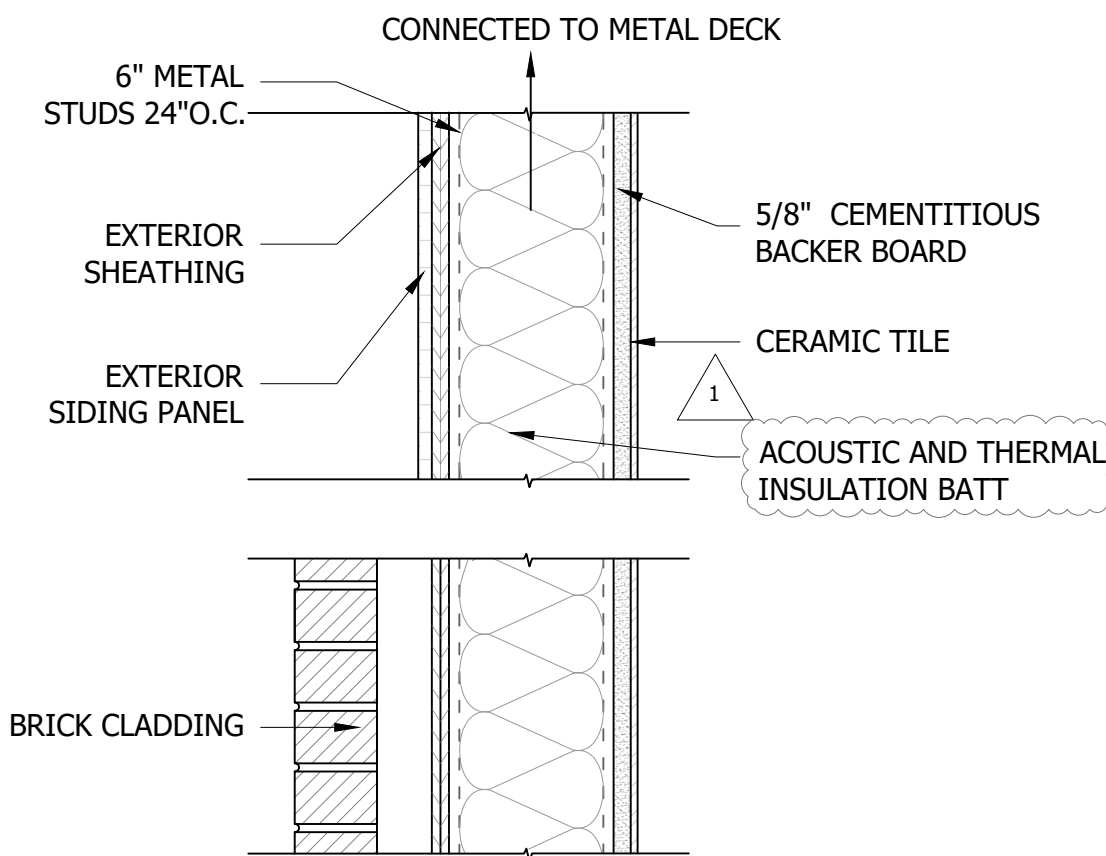

6" PARTITION WALL TYPE B1
SCALE: NTS

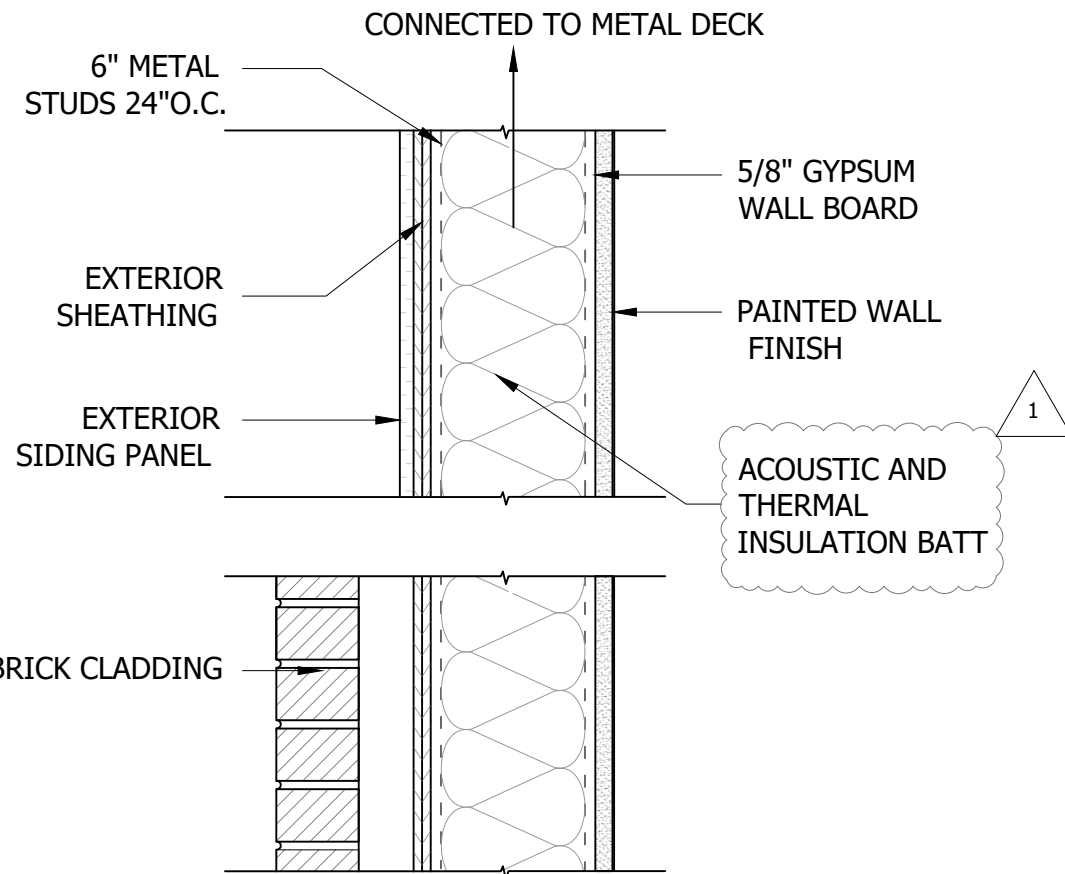

6" PARTITION WALL TYPE B2
SCALE: NTS

RESTROOMS

CAROLINA MURUGAN TEMPLE - PHASE 1

CLIENT: CAROLINA MURUGAN TEMPLE
100 MURUGAN CIR, MONCURE, NC 27559

DATE: 6/13/2025

SSN JOB ID: 1021-02-2024

DESIGNED BY: MK

DRAWN BY: BM

CHECKED BY: MK

REVIEWED BY: MN



#	REVISIONS	DATE
1	REV-1	6/11/2025

DOOR AND WINDOW DETAILS AND
PARTITION TYPE DETAILS

C - 302