

H:\Dropbox\SouthDesigns_CADS Transfer\Triple A Homes\Chapel Ridge Lot 574\CH Lot 574_Alt Elev dwg_9-19-2024 1-47 13.PML DWFX.ePlot (NYS Compatible).pc3

B2M



P.O. Box 688
Wake Forest, NC 27588
(O) 919-556-2226
(F) 919-556-2228
www.southdesigns.com

Drawn By: SDI

Checked By: SDI

Date: 06-26-2024

Revision No.	Revision Date

Designer Signature

This plan is the property of South Designs, Inc. and may not be used or reproduced without the expressed written consent of South Designs, Inc. These drawings are offered to the named client for a conditional one time use. The conditional use is limited to the lot or property as specified herein, and only for said location.

South Designs, Inc. assumes no liability for any home constructed from these plans. Contractor or builder shall verify all dimensions and conditions prior to construction. Caution must be exercised when making changes to these drawings. If changes are made to these drawings, contact South Designs.

Client: Chapel Ridge
Lot 574

Title:

ELEVATIONS

Plan No.

EL-1

Sheet No. _____ of _____



1 FRONT ELEVATION
SCALE: 1/4" = 1'-0"

SCALE: 1/4" = 1'-0"

384

© COPYRIGHT 2024 SOUTH DESIGNS, INC.



**SOUTH
DESIGNS**

P.O. Box 688
Wake Forest, NC 27588
(O) 919-556-2226
(F) 919-556-2228
www.southdesigns.com

Drawn By:	SDI
Checked By:	SDI
Date:	06-26-2024
Revision No.	Revision Date

Designer Signature

This plan is the property of South Designs, Inc. and may not be used or reproduced without the expressed written consent of South Designs, Inc. These drawings are offered to the named client for a conditional use time only. The conditional use is limited to the lot or property as specified herein, and only for said location.


South Designs, Inc. assumes no liability for any home constructed from these plans. Contractor or builder shall verify all dimensions and conditions prior to construction. Caution must be exercised when making changes to these drawings. If changes are made to these drawings, contact South Designs.

Client:
**Chapel Ridge
Lot 574**


Title:
ELEVATIONS

Plan No.
EL-2

Sheet No. Of

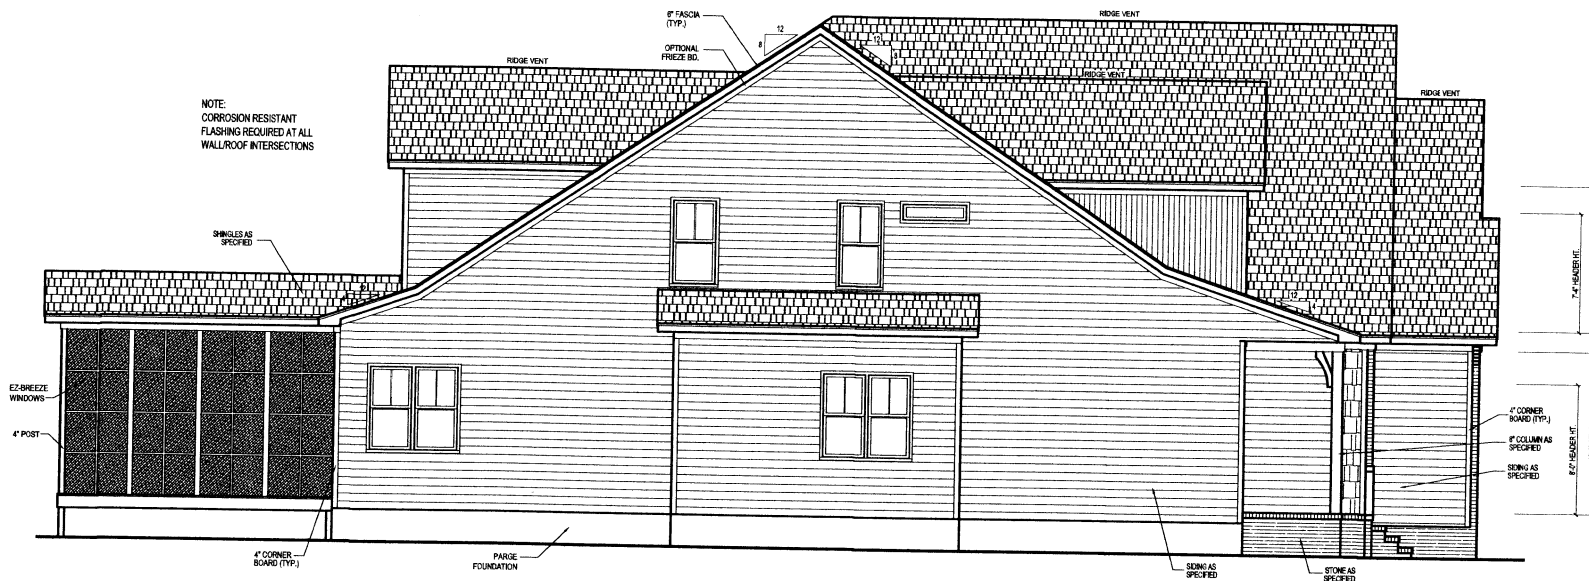


3 RIGHT ELEVATION
SCALE: 3/16" = 1'-0"

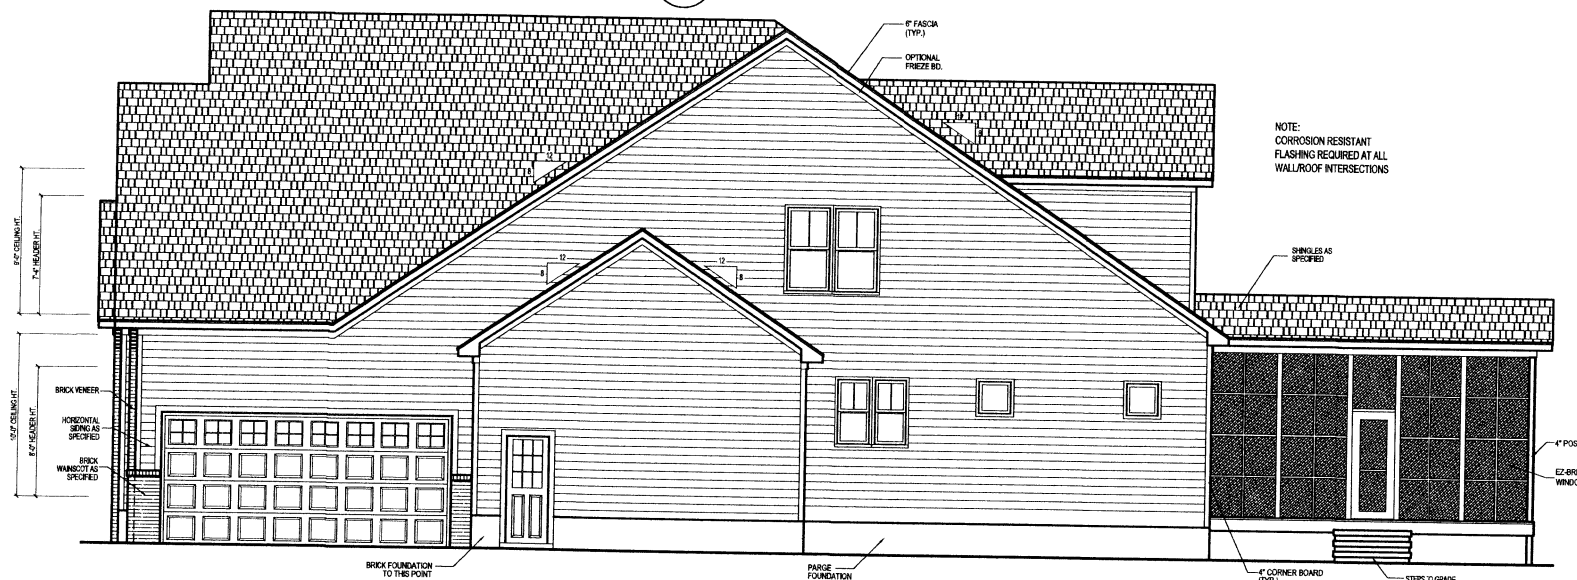

2 LEFT ELEVATION
SCALE: 3/16" = 1'-0"

© COPYRIGHT 2024 SOUTH DESIGNS, INC.

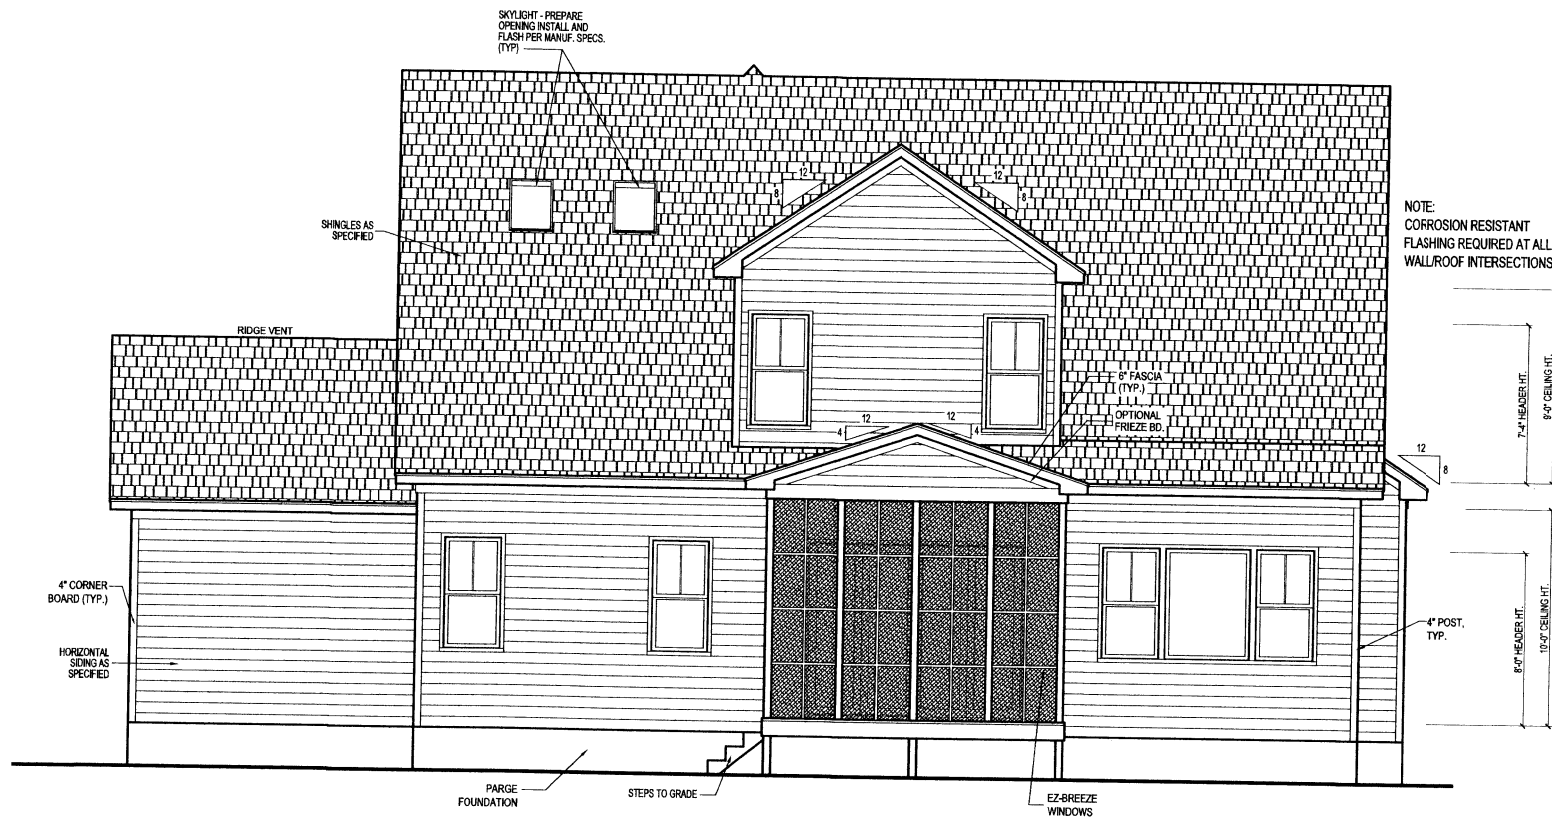

4 REAR ELEVATION
SCALE: 1/4" = 1'-0"



**SOUTH
DESIGNS**

P.O. Box 688
Wake Forest, NC 27588
(O) 919-556-2226
(F) 919-556-2228
www.southdesigns.com

Drawn By:	SDI
Checked By:	SDI
Date:	06-26-2024
Revision No.	Revision Date

Designer Signature

This plan is the property of South Designs, Inc. and may not be used or reproduced without the expressed written consent of South Designs, Inc. These drawings are offered in the named client for a conditional one time use. The conditional use is limited to the lot or property as specified herein, and only for that location.

South Designs, Inc. assumes no liability for any home constructed from these plans. Contractor or builder shall verify all dimensions and conditions prior to construction. Client must be contacted when making changes to these drawings. If changes are made to these drawings, contact South Designs.

Client:
**Chapel Ridge
Lot 574**

Title:
ELEVATIONS

Plan No.
EL-3
Sheet No. Of

