



SAMPLE SINGLE DETACHED DWELLING

DP/BP COMBINED PLAN SET

3615 4 ST SW

THIS DRAWING SET IS INTENDED TO REPRESENT A TYPICAL
DEVELOPMENT PERMIT AND BUILDING PERMIT DRAWING SET. THESE
PLANS REMAIN THE PROPERTY OF THE CITY OF CALGARY AND
REPRODUCTION WITHOUT PERMISSION IS EXPRESSLY PROHIBITED.

DRAWING INDEX

SITE INFORMATION

BLOCK PLAN & STREETScape	1
SITE PLAN	2
SITE CROSS SECTION	3

ELEVATIONS

EAST ELEVATION (FRONT)	4
WEST ELEVATION	5
NORTH ELEVATION	6
SOUTH ELEVATION	7

FLOOR PLANS

FOUNDATION PLAN	8
MAIN FLOOR PLAN	9
UPPER FLOOR PLAN	10
ROOF PLAN	11
DECK DETAILS AND PLAN	12

ELECTRICAL PLANS

FOUNDATION PLAN	13
MAIN FLOOR PLAN	14
UPPER FLOOR PLAN	15

SECTION, NOTES AND DETAILS

SECTION A-A	16
GENERAL NOTES	17
CONSTRUCTION ASSEMBLIES	17
WINDOW SCHEDULE	18
WINDOW FLASHING DETAIL	19
9.36 GENERAL NOTES	20
DETAILS	21-23



NO.	EXTERIOR MATERIALS
1	BLACK ASPHALT SHINGLES
2	WHITE 6" FASCIA
3	BEIGE VINYL SIDING
4	NATURAL FINISH CEDAR SHAKES
5	PRESSURE TREATED DECK LEDGER

 EAST ELEVATION
SCALE: 3/16"=1'-0"

This drawing set is intended to act as an example of drawing standards and may not be reproduced without permission. Any similarities with actual buildings and or locations is coincidental. Refer to the requirements list for complete drawing requirements.

Revisions:

Issued For:

Consultants/Seals:

MUNICIPAL ADDRESS:
3615 4 ST SW
LEGAL ADDRESS:
4647GU; A; 7,8

Drawing Name:
EAST ELEVATION (FRONT)

Drawn: _____ Checked: _____

Date: _____


Drawing Scale: **3/16"=1'-0"**

Consultant Project Number: _____

Project Number: _____ Sheet: **4 OF 23**

Consultant File Number: _____

File Number: _____

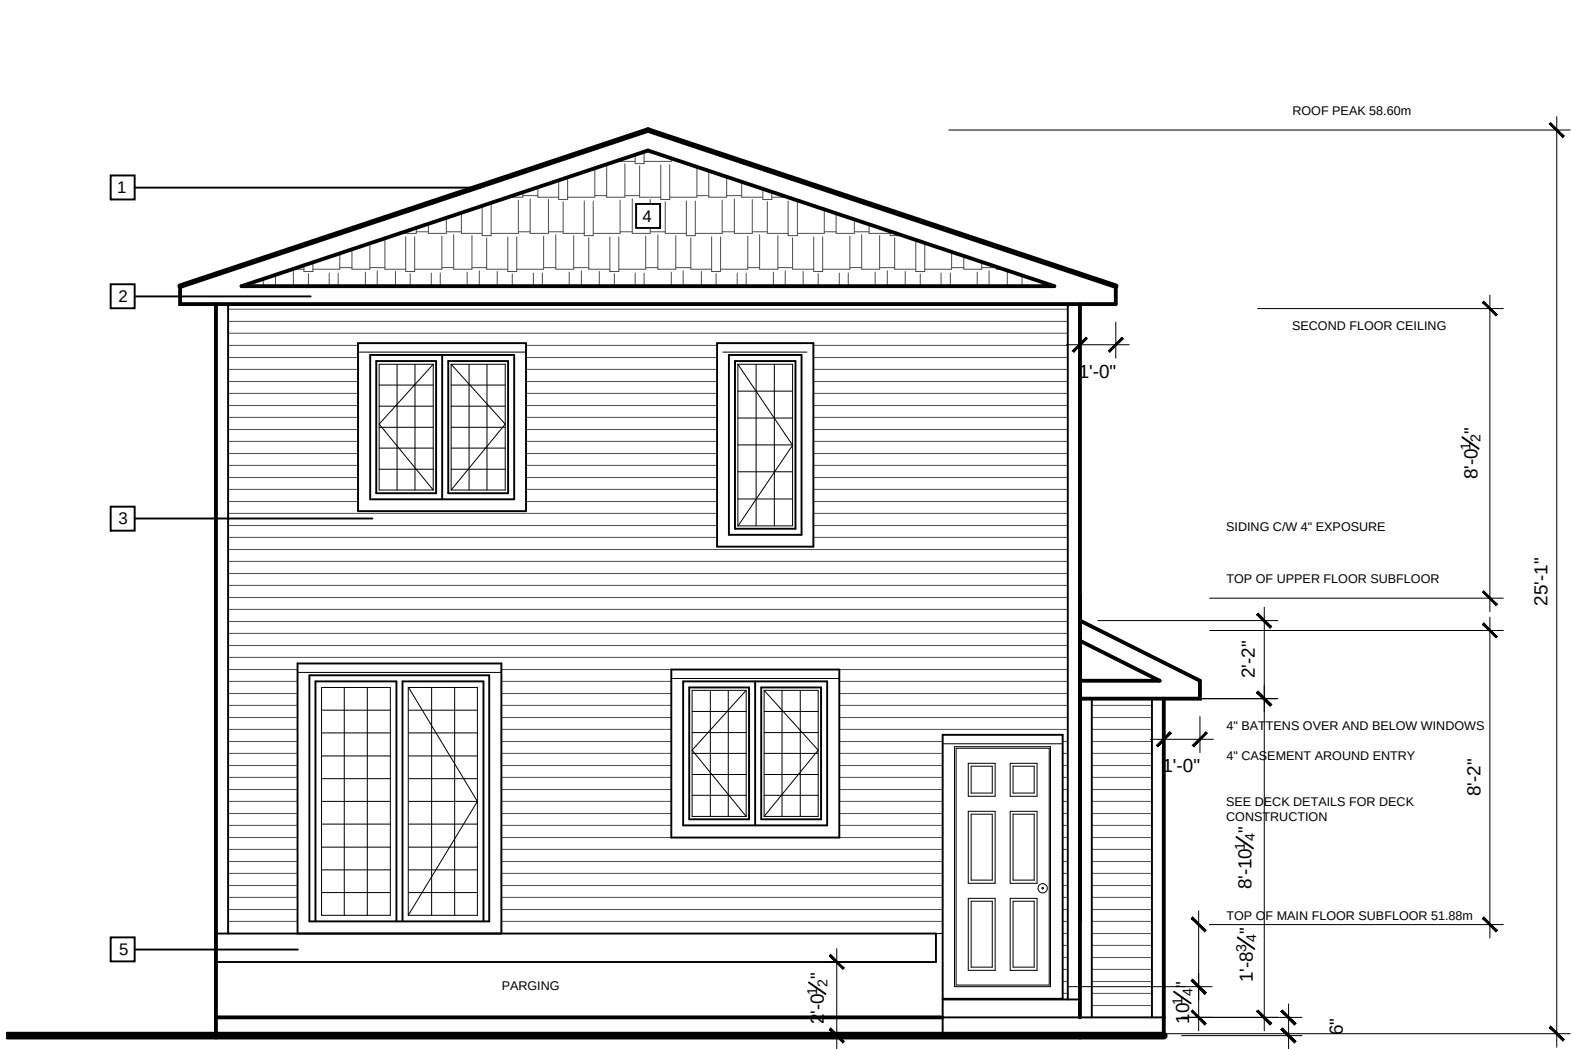

NO.	EXTERIOR MATERIALS
1	BLACK ASPHALT SHINGLES
2	WHITE 6" FASCIA
3	BEIGE VINYL SIDING
4	NATURAL FINISH CEDAR SHAKES
5	PRESSURE TREATED DECK LEDGER

WEST ELEVATION
SCALE: 3/16"=1'-0"

This drawing set is intended to act as an example of drawing standards and may not be reproduced without permission. Any similarities with actual buildings and or locations is coincidental. Refer to the requirements list for complete drawing requirements.

Revisions:		

Issued For:		

Consultants/Seals:	

MUNICIPAL ADDRESS:
3615 4 ST SW
LEGAL ADDRESS:
4647GU; A; 7,8

Drawing Name:
WEST ELEVATION

Drawn: _____ Checked: _____

Date: _____


Drawing Scale: **3/16"=1'-0"**

Consultant Project Number: _____

Project Number: _____ Sheet: **5 OF 23**

Consultant File Number: _____

File Number: _____

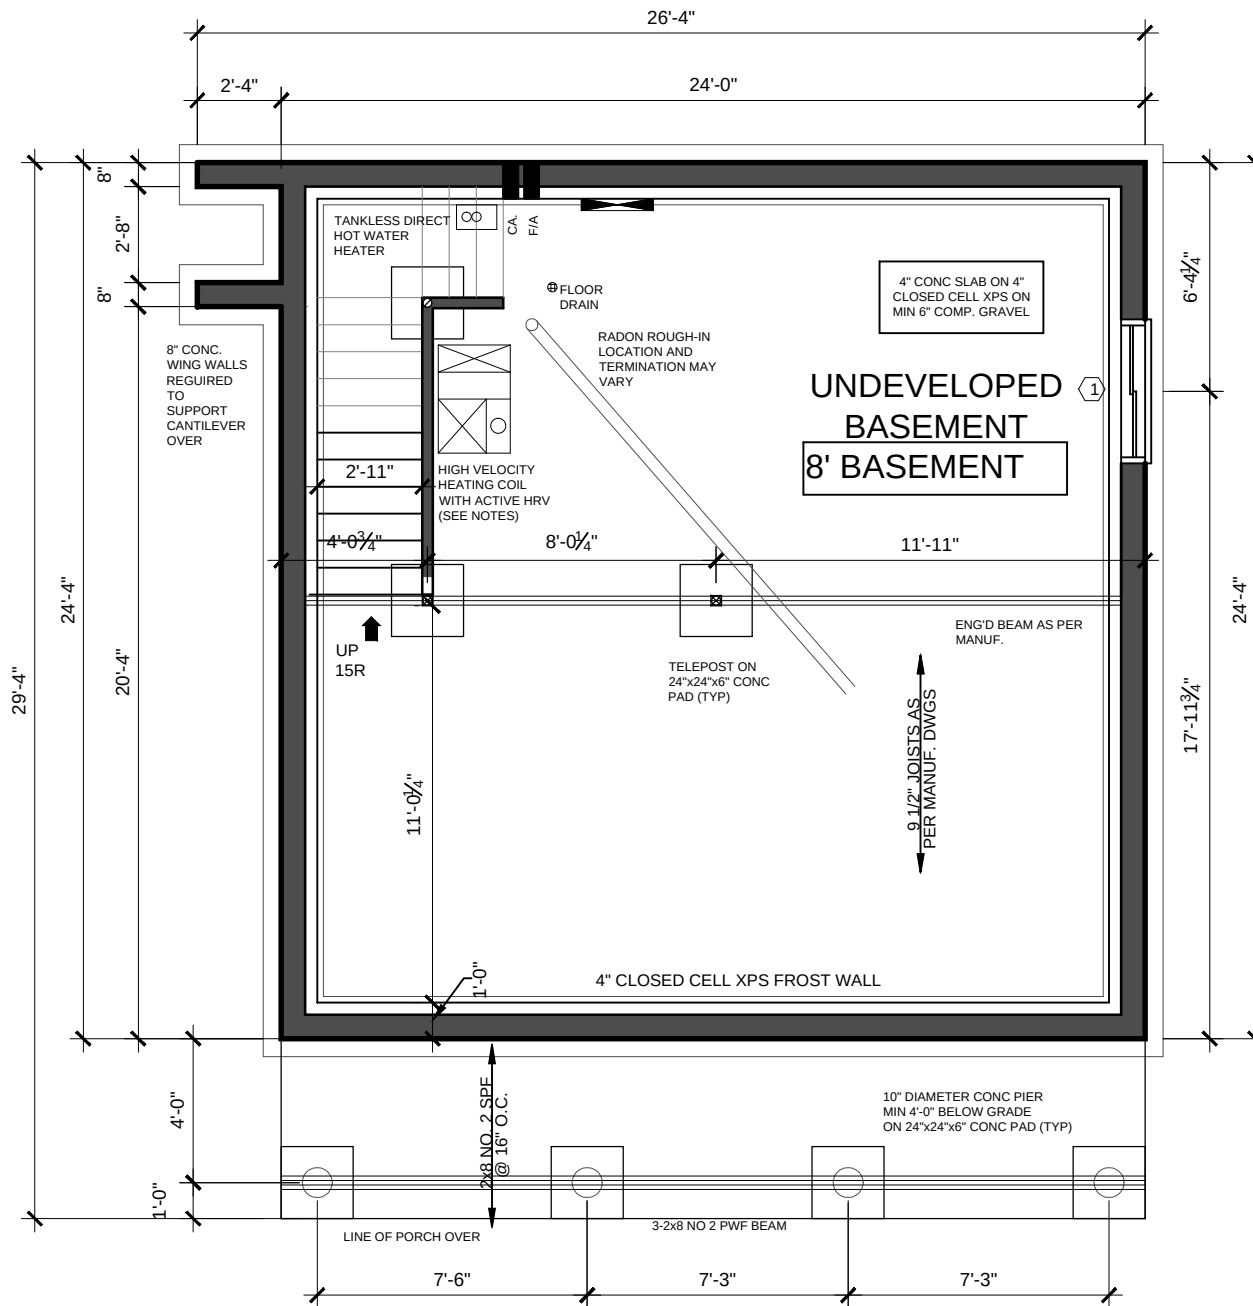

FOUNDATION PLAN
SCALE: 3/16"=1'-0"

This drawing set is intended to act as an example of drawing standards and may not be reproduced without permission. Any similarities with actual buildings and or locations is coincidental. Refer to the requirements list for complete drawing requirements.

Revisions:

Issued For:

Consultants/Seals:

MUNICIPAL ADDRESS:
3615 4 ST SW
LEGAL ADDRESS:
4647GU; A; 7,8

Drawing Name:
FOUNDATION PLAN

Drawn: _____ Checked: _____

Date: _____

Drawing Scale: **3/16"=1'-0"**

Consultant Project Number: _____


Project Number: _____

Sheet:

8 OF 23

Consultant File Number: _____

File Number: _____

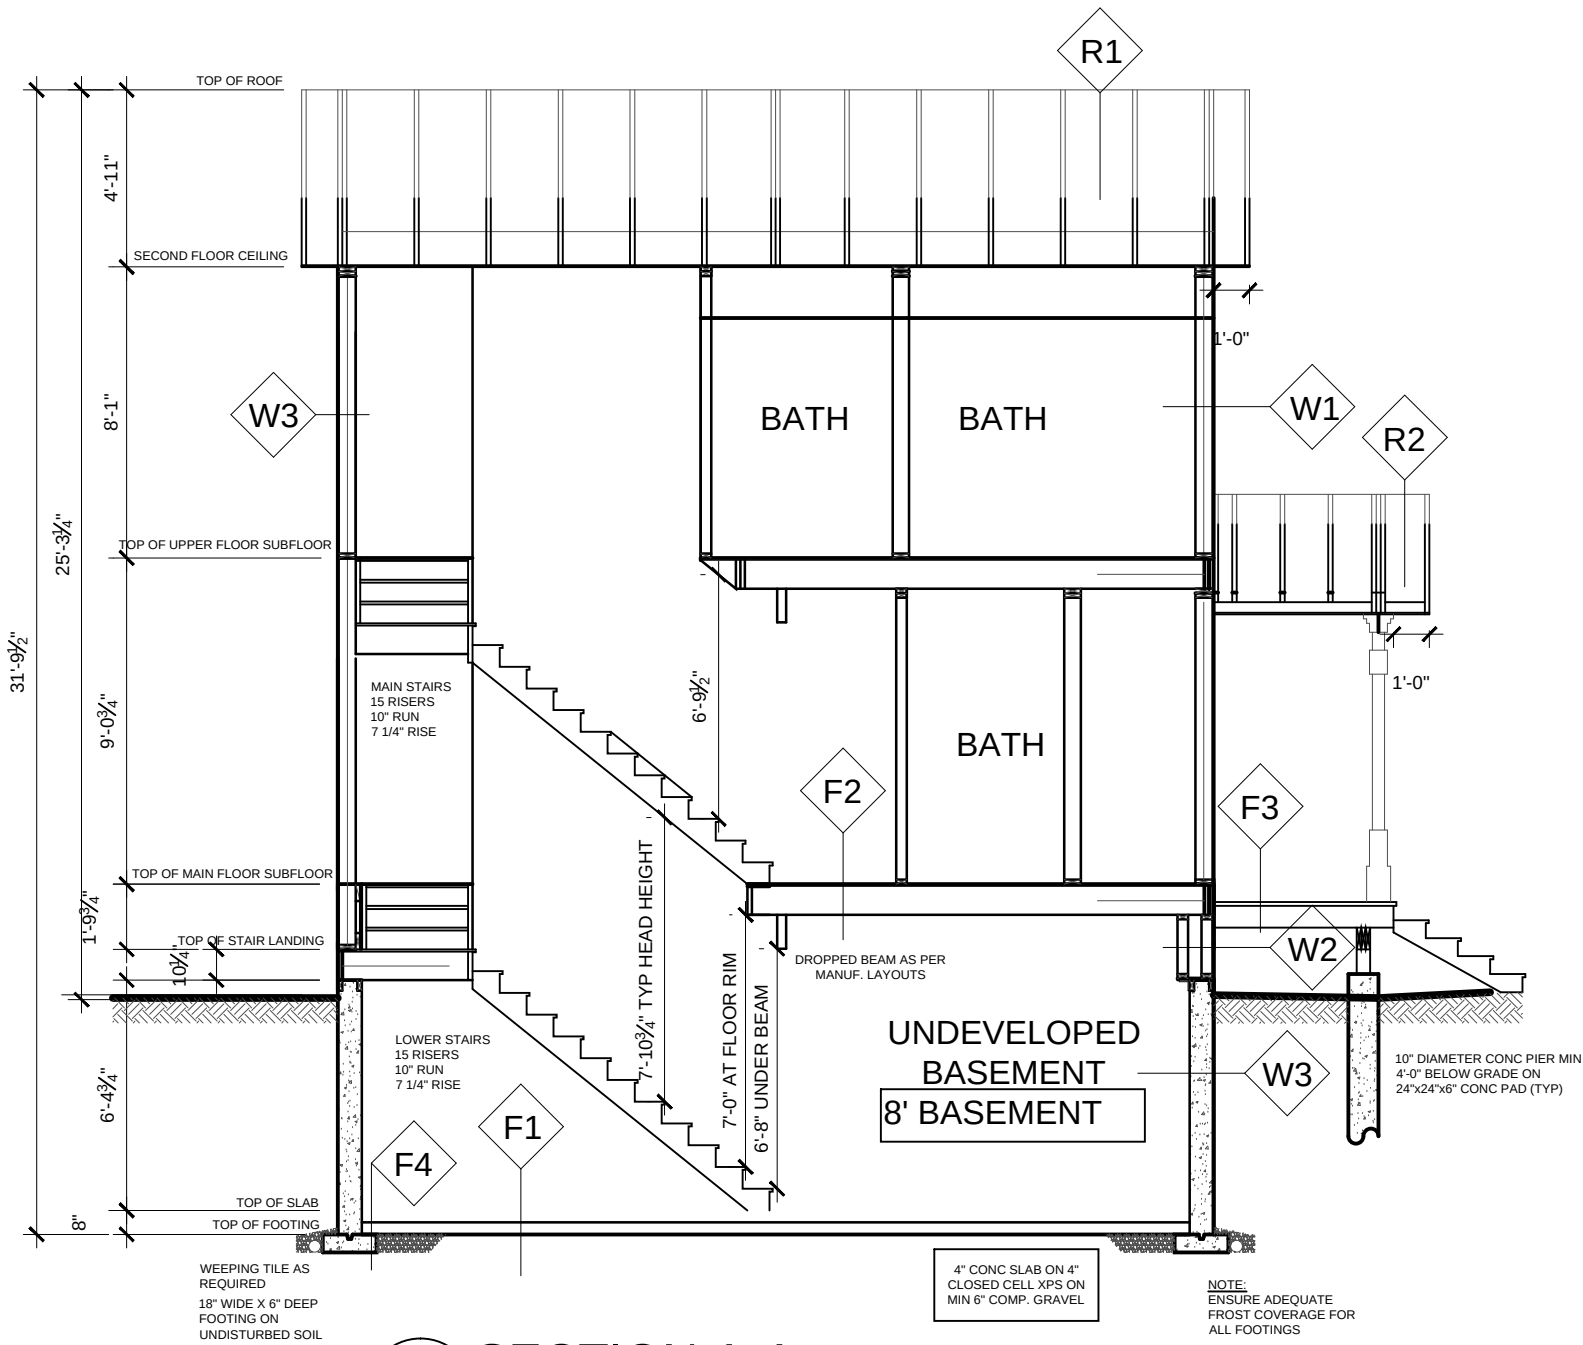

SECTION A-A

SCALE: 3/16"=1'-0"

This drawing set is intended to act as an example of drawing standards and may not be reproduced without permission. Any similarities with actual buildings and or locations is coincidental. Refer to the requirements list for complete drawing requirements.

Revisions:		

Issued For:		

Consultants/Seals:		

MUNICIPAL ADDRESS:
3615 4 ST SW
LEGAL ADDRESS:
4647GU; A; 7,8

Drawing Name:
SECTION A-A

Drawn: _____ Checked: _____

Date: _____

Drawing Scale: 3/16"=1'-0"

Consultant Project Number: _____

Project Number: _____ Sheet: 16 OF 23

Consultant File Number: _____

File Number: _____

GENERAL NOTES

DRAWINGS ARE INTENDED FOR INFORMATIONAL PURPOSES ONLY AND ARE INTENDED TO PRESENT A TYPICAL DRAWINGS SET SUCH AS REQUIRED BY THE CITY OF CALGARY COMPLETE APPLICATION REQUIREMENT LISTS. THIS SET MAY OR MAY NOT FULFILL ALL ASPECTS AND/OR REQUIREMENTS OF ANY APPLICABLE REQUIREMENT LIST AND SHOULD ONLY BE USED TO DEMONSTRATE A PROFESSIONAL LEVEL OF DRAFTING STANDARDS AS REQUIRED FOR THE SUBMISSION OF AN APPLICATION TO THE CITY OF CALGARY. USE OF THESE DRAWINGS FOR DUPLICATION AND OR SUBMISSION IN WHOLE OR IN PART IS PROHIBITED.

UNLESS OTHERWISE NOTED, ALL DETAILS, SECTIONS AND NOTES SHOWN ON THE CONTRACT DRAWINGS ARE INTENDED TO BE TYPICAL AND SHALL APPLY TO SIMILAR CONDITIONS ELSEWHERE.

ALL OMISSIONS OR CONFLICTS BETWEEN THE VARIOUS ELEMENTS OF THE CONTRACT DRAWINGS AND OR SPECIFICATIONS SHALL BE BROUGHT TO THE ATTENTION OF THE ENGINEER AND OR DESIGNER BEFORE PROCEEDING WITH ANY WORK INVOLVED.

THE CONTRACTOR SHALL VERIFY ALL JOB SITE CONDITIONS AND RELATED DIMENSIONS.

ALL CONSTRUCTION SHALL BE IN ACCORDANCE TO THE LATEST EDITION OF THE ALBERTA BUILDING CODE.

THE CONTRACTOR SHALL BE RESPONSIBLE FOR THE PROTECTION OF AND THE SAFETY IN AND AROUND THE JOB SITE AND OF ADJACENT PROPERTIES.

CONTRACTOR AND OR OWNER SHALL KEEP LOADS ON THE STRUCTURE WITHIN THE LIMITS OF THE DESIGN BOTH DURING AND AFTER CONSTRUCTION.

COMPLIANCE WITH APPLICABLE CODES, ORDINANCES AND BYLAWS GOVERNMING THE WORK SHALL BE MADE AND ENFORCED BY THE GENERAL CONTRACTOR.

GENERAL CONTRACTOR SHALL VERIFY ALL EXISTING CONDITIONS AND DIMENSIONS PRIOR TO CONSTRUCTION.

NOTE THAT ALL WRITTEN DIMENSIONS TAKE PRECEDENCE OVER SCALE.

MANUFACTURER'S SPECIFICATIONS FOR INSTALLATION OF MATERIALS SHALL BE FOLLOWED.

WORKMANSHIP THROUGHOUT SHALL BE OF THE BEST QUALITY OF THE TRADE INVOLVED AND THE GENERAL CONTRACTOR SHALL COORDINATE THE WORK OF THE VARIOUS TRADES TO EXPEDITE THE JOB IN A SMOOTH AND CONTINUOUS PROCESS.

CONSTRUCTION ASSEMBLY NOTES

WALL TYPES

- W1

TYPICAL EXTERIOR WALL ASSEMBLY
VINYL SIDING
TYVEK HOUSE WRAP
1/2" OSB EXTERIOR SHEATHING
2X6 STUDS @ 16" O.C.
R-25 BATT INSULATION
6 MIL POLY VAPOUR BARRIER
1/2" GYPSUM DRYWALL
- W2

DOUBLE WALL ASSEMBLY AT PONY WALL
VINYL SIDING
TYVEK HOUSE WRAP
1/2" OSB EXTERIOR SHEATHING
2X4 STUD WALL @ 16 O.C.
5" CAVITY
LOOSE FILL BLOWN INSULATION R-50 MIN
2X4 STUD WALL @ 16 O.C.
6 MIL POLY VAPOUR BARRIER
- W3

FOUNDATION WALL ASSEMBLY
DRAINAGE BOARD
DAMP-PROOFING
8" CONCRETE FOUNDATION WALL
4" CLOSED CELL XPS INSULATION

FLOOR TYPES

- F1

FOUNDATION SLAB
4" CONCRETE SLAB
6 MIL POLY AIR BARRIER
MIN 6" COMPACTED GRAVEL BASE
- F2

TYPICAL FLOOR ASSEMBLY
3/4" PLYWOOD SUBFLOOR
9 1/2" TJI ENGINEERED JOISTS @ 16 O.C.
1/2" GYPSUM DRYWALL
- F3

PORCH DECK ASSEMBLY
5/8" DECKING
2X8 JOISTS @ 16 O.C.
- F4

FOOTING ASSEMBLY
20" x 6" CONC. STRIP FOOTINGS

ROOF ASSEMBLY TYPES

- R1

MAIN ROOF ASSEMBLY
ASPHALT SHINGLES
ICE AND WEATHER SHIELD
1/2" PLYWOOD C/W H CLIPS AT JOINS
ENGINEERED TRUSSES @ 24 O.C. PER LAYOUTS
BLOWN IN LOOSE FILL INSULATION TO MEET R-50
BATT INSULATION R-21 BETWEEN TRUSSES
6 MIL POLY VAPOUR BARRIER
1/2" GYPSUM DRYWALL
- R2

PORCH ROOF ASSEMBLY
ASPHALT SHINGLES
ICE AND WEATHER SHIELD
1/2" PLYWOOD C/W H CLIPS AT JOINS
ENGINEERED TRUSSES @ 24 O.C. PER LAYOUT
PAINTED EXTERIOR GRADE MDF SHEATHING
VENTING PER ABC

This drawing set is intended to act as an example of drawing standards and may not be reproduced without permission. Any similarities with actual buildings and or locations is coincidental. Refer to the requirements list for complete drawing requirements.

Revisions:

Issued For:

Consultants/Seals:

MUNICIPAL ADDRESS:
3615 4 ST SW
LEGAL ADDRESS:
4647GU; A; 7,8

Drawing Name:
GENERAL NOTES &
CONSTRUCTION
ASSEMBLIES

Drawn: Checked:

Date:

Drawing Scale: NTS

Consultant Project Number:

Project Number: Sheet:

17 OF 23


Consultant File Number:

File Number:

NORTH AMERICAN FENESTRATION STANDARDS

TERRAIN - OPEN
PERFORMANCE CLASS -R
PERFORMANCE GRADE - PG30
POSITIVE DESIGN PRESSURE 1440 Pa
NEGATIVE DESIGN PRESSURE - 1440 Pa
WATER PENETRATION RESISTANCE TEST
PRESSURE - 330 Pa
CANADIAN AIR INFILTRATION/EXFILTRATION - A2
LEVEL
U-VALUE - MAXIMUM OF 1.6 FOR DOORS AND
WINDOWS. MAXIMUM OF 2.7 FOR SKYLIGHTS PER
9.7.3.3

WINDOW SCHEDULE				
NO.	TYPE (H X W)	NOTES	LEVEL	COUNT
①	48" X 36 1/4" SL	XO, 185 SERIES OR EQUIV.	FDN	1
②	83 1/2" X 59 7/8" TRI-WINDOW	LPR CASEMENT, 260 SERIES OR EQUIV.	MAIN	1
③	24 3/8" X 59 7/8" CASEMENT	R, 260 SERIES OR EQUIV.	MAIN & 2	2
④	48" X 48" DUAL CASEMENT	LR, 260 SERIES OR EQUIV.	MAIN & 2	2
⑤	36" X 36" CASEMENT	R, 260 SERIES OR EQUIV.	2ND	2
⑥	51" X 48" SINGLE HUNG	XO, 260 SERIES OR EQUIV.	2ND	2

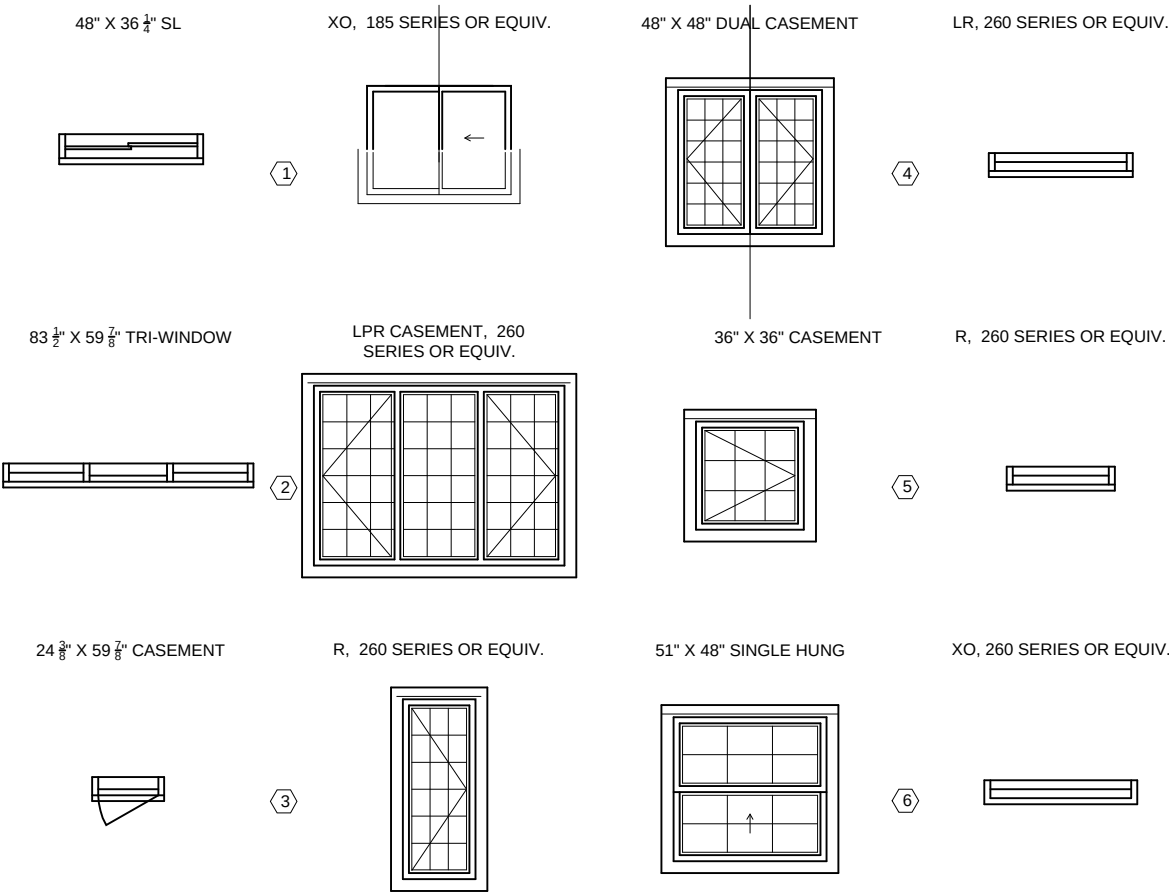

This drawing set is intended to act as an example of drawing standards and may not be reproduced without permission. Any similarities with actual buildings and or locations is coincidental. Refer to the requirements list for complete drawing requirements.

Revisions:		

Issued For:		

Consultants/Seals:		

MUNICIPAL ADDRESS:
3615 4 ST SW
LEGAL ADDRESS:
4647GU; A; 7,8

Drawing Name:
WINDOW SCHEDULE

Drawn: _____ Checked: _____

Date: _____

Drawing Scale: NTS

Consultant Project Number: _____

Project Number: _____ Sheet: 18 OF 23

Consultant File Number: _____

File Number: _____

9.36 NECB INFORMATION AND NOTES ON COMPLIANCE

PREScriptive COMPLIANCE PATH PER ABC 9.36

NOTES:
SEALED POLYETHELYNE APPROACH COMBINED WITH RIGID CLOSED CELL XPS

HEATING SYSTEM
NATURAL GAS FIRED HI VELOCITY HEATING SYSTEM 95% EFFICIENCY
ACTIVE HRV - 60% EFFICIENT AT 0 DEGREES C; 55% EFFICIENT AT -25 DEGREES C
NATURAL GAS FIRED ON DEMAND HOT WATER HEATING SYSTEM
ALL HOT WATER PIPES WRAPPED WITH 12MM PIPE INSULATION

EFFECTIVE RSI VALUES OF ASSEMBLIES COVERED BY 9.36

WALL TYPES

W1 TYPICAL EXTERIOR WALL ASSEMBLY
VINYL SIDING
TYVEK HOUSE WRAP
½" OSB EXTERIOR SHEATHING
2X6 STUDS @ 16" O.C.
R-25 BATT INSULATION
6 MIL POLY VAPOUR BARRIER
½" GYPSUM DRYWALL
EFFECTIVE RSI 3.72*

W2 DOUBLE WALL ASSEMBLY AT PONY WALL
VINYL SIDING
TYVEK HOUSE WRAP
½" OSB EXTERIOR SHEATHING
2X4 STUD WALL @ 16 O.C.
5" CAVITY
LOOSE FILL BLOWN INSULATION R-40 MIN
2X4 STUD WALL @ 16 O.C.
6 MIL POLY VAPOUR BARRIER
EFFECTIVE RSI 13.41

W3 FOUNDATION WALL ASSEMBLY
DRAINAGE BOARD
DAMP-PROOFING
8" CONCRETE FOUNDATION WALL
4" CLOSED CELL XPS INSULATION
EFFECTIVE RSI 3.72*

*NOTE: VALUE IS SOFTWARE DERIVED

FLOOR TYPES

F1 FOUNDATION SLAB
4" CONCRETE SLAB
4" CLOSED CELL XPS INSULATION
MIN 6" COMPACTED GRAVEL BASE
EFFECTIVE RSI 3.72*

ROOF ASSEMBLY TYPES

R1 MAIN ROOF ASSEMBLY
ASPHALT SHINGLES
ICE AND WEATHER SHIELD
½" PLYWOOD C/W H CLIPS AT JOINS
ENGINEERED TRUSSES @ 24 O.C. PER LAYOUTS
BLOWN IN LOOSE FILL INSULATION TO MEET R-50
BATT INSULATION R-21 BETWEEN TRUSSES
6 MIL POLY VAPOUR BARRIER
½" GYPSUM DRYWALL
EFFECTIVE RSI 11.62*

This drawing set is intended to act as an example of drawing standards and may not be reproduced without permission. Any similarities with actual buildings and or locations is coincidental. Refer to the requirements list for complete drawing requirements.

Revisions:

Issued For:

Consultants/Seals:

MUNICIPAL ADDRESS:
3615 4 ST SW
LEGAL ADDRESS:
4647GU; A; 7,8

Drawing Name:
9.36 NOTES AND
ASSEMBLY EFFECTIVE
RSI VALUES

Drawn:	Checked:
Date:	
Drawing Scale: NTS	
Consultant Project Number:	
Project Number:	Sheet: 20 OF 23
Consultant File Number:	
File Number:	

This drawing set is intended to act as an example of drawing standards and may not be reproduced without permission. Any similarities with actual buildings and or locations is coincidental. Refer to the requirements list for complete drawing requirements.

Revisions:		

Issued For:		

Consultants/Seals:		

MUNICIPAL ADDRESS:
3615 4 ST SW
LEGAL ADDRESS:
4647GU; A; 7,8

Drawing Name:
DETAILS

Drawn: Checked:

Date:


Drawing Scale: **NTS**

Consultant Project Number:


Project Number:	Sheet: 22 OF 23
-----------------	---------------------------

Consultant File Number:


File Number:

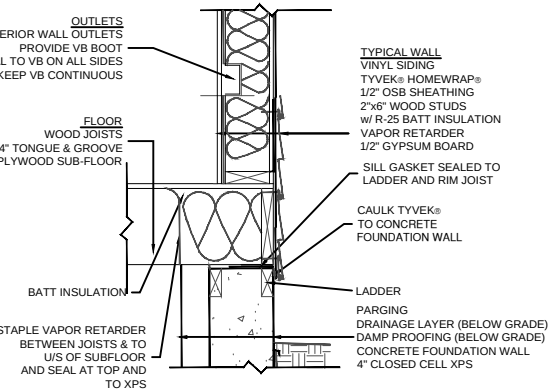


BASE OF WALL AT STAIR DETAIL

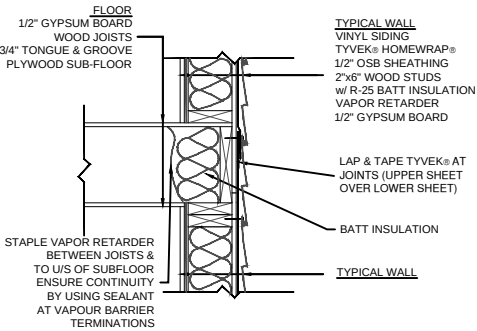


FLOOR/ WALL INTERFACE DETAIL

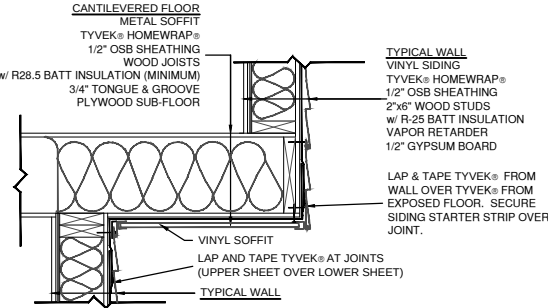


CANTILEVERED FLOOR DETAIL

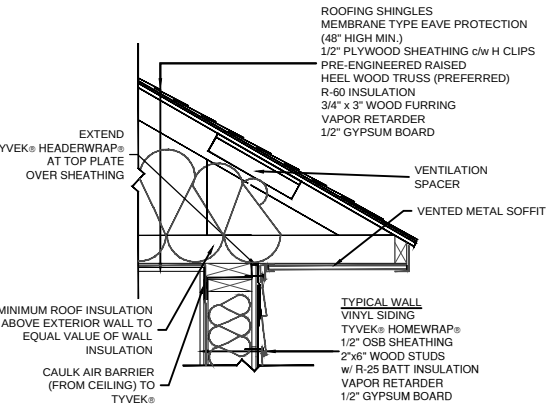

ROOF/ WALL INTERFACE DETAIL

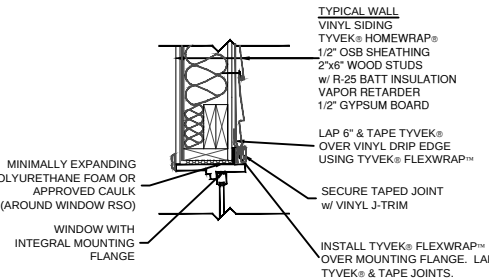

WINDOW HEAD DETAIL

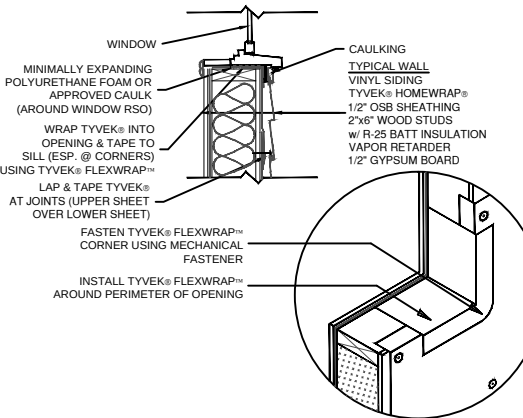

WINDOW SILL DETAIL

*SEAL ALL TYVEK® JOINTS AND PENETRATIONS WITH APPROVED TAPE.
(ex. DUPONT CONTRACTOR TAPE).
*FASTEN TYVEK® TO SHEATHING WITH LARGE HEAD NAILS
OR USE NAILS WITH LARGE PLASTIC WASHER HEADS (ex. DUPONT WRAPCAPS)
*LOCAL LAWS, ZONING, AND BUILDING CODES VARY AND
THEREFORE GOVERNS OVER MATERIAL SELECTION AND DETAILING SHOWN BELOW.